



Состав проекта.

№ листа	Наименование листа	Примечание
01	Состав проекта.	
02	Обмерный план цокольного этажа.	
03	Обмерный план 1го этажа.	
04	Обмерный план 2го этажа.	
05	Обмерный план мансардного этажа.	
06	Планировочное решение цокольного этажа.	
07	Планировочное решение 1 этажа.	
08	Планировочное решение 2 этажа.	
09	Сечение A1-A1	
10	Планировочное решение Мансардного этажа.	
11	План сносимых и возводимых стен цокольного этажа.	
12	План сносимых и возводимых стен 1го этажа.	
13	План сносимых и возводимых стен 2го этажа.	
14	План сносимых и возводимых стен мансардного этажа.	
15	Экспликация дверей и проёмов цокольного этажа.	
16	Экспликация дверей и проёмов 1го этажа.	
17	Экспликация дверей и проёмов 2го этажа.	
18	Экспликация дверей и проёмов мансардного этажа.	
19	Схема размещения сантехники цокольного этажа.	
20	Схема размещения сантехники 1го этажа.	
21	Схема размещения сантехники 2го этажа.	
22	Схема размещения сантехники мансардного этажа.	
23	Схема напольного покрытия и тёплых полов цокольного этажа.	
24	Схема напольного покрытия и тёплых полов 1го этажа.	
25	Схема напольного покрытия и тёплых полов 2го этажа.	
26	Схема напольного покрытия и тёплых полов мансардного этажа.	
27	План потолков цокольного этажа.	
28	План потолков 1го этажа.	
29	Сечение потолков 1го этажа.	
30	План потолков 2го этажа.	
31	Сечение потолков 2го этажа.	
32	План потолков мансардного этажа.	
33	Сечение потолков мансардного этажа.	
34	Схема размещения светильников цокольного этажа.	
35	Схема размещения светильников 1 этажа.	
36	Схема размещения светильников 2 этажа.	
37	Схема размещения светильников мансардного этажа.	
38	Схема размещения выключателей с привязкой к светильникам цокольного этажа.	
39	Схема размещения выключателей с привязкой к светильникам 1го этажа.	
40	Схема размещения выключателей с привязкой к светильникам 2го этажа.	
41	Схема размещения выключателей с привязкой к светильникам мансардного этажа.	
42	Схема размещения розеток и эл. выводов цокольного этажа.	
43	Схема размещения розеток и эл. выводов 1го этажа.	
44	Схема размещения розеток и эл. выводов 2го этажа.	
45	Схема размещения розеток и эл. выводов мансардного этажа.	
46	Развёртка лестницы.	

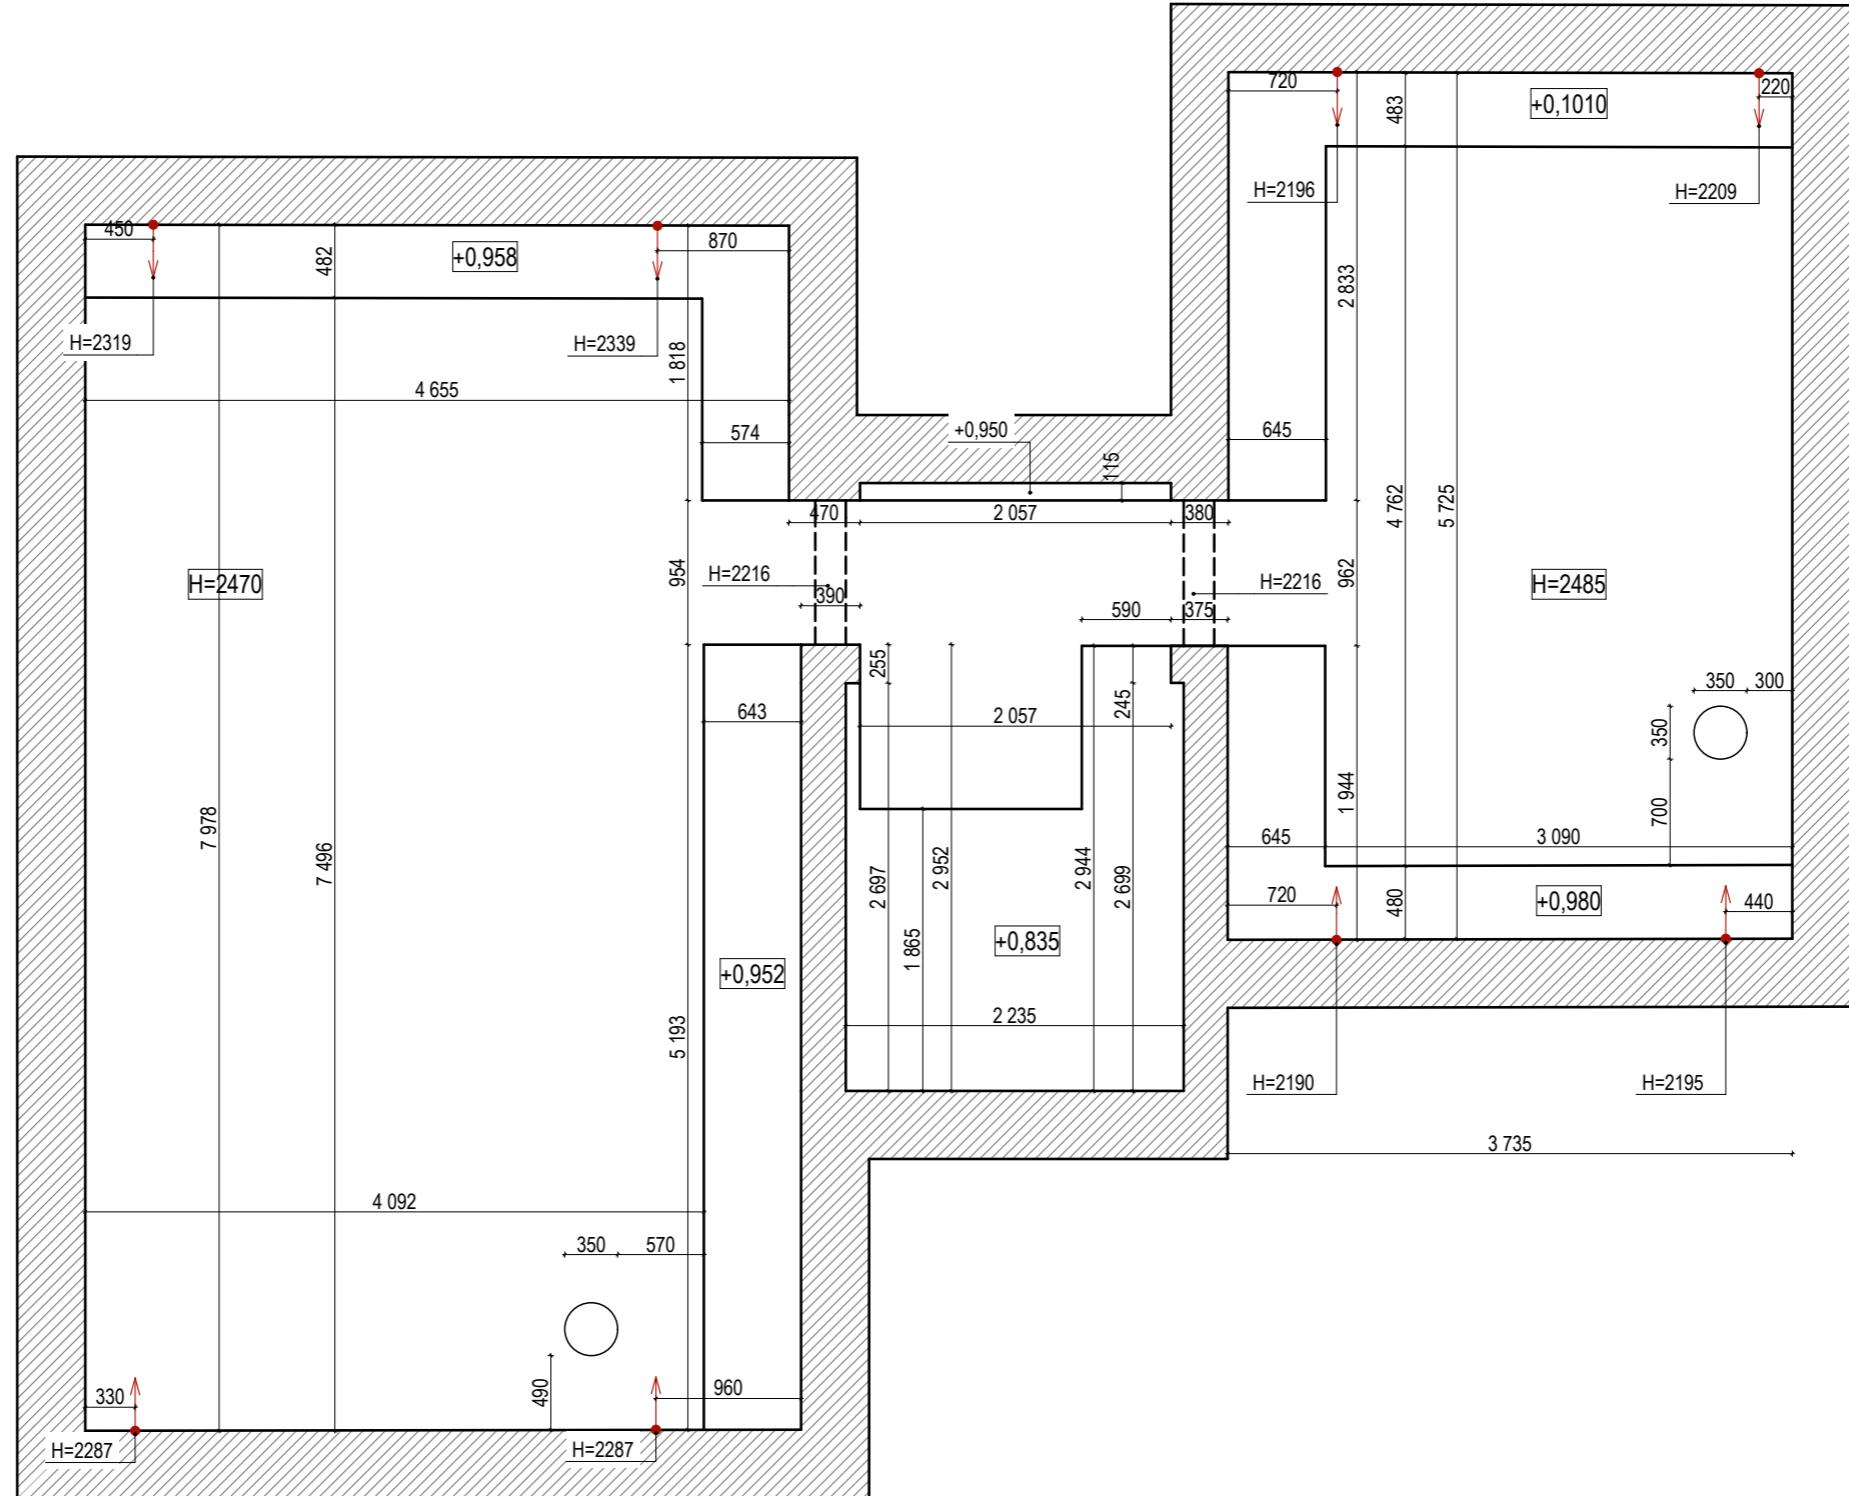


Обмерный план цокольного этажа.

Обмерный план цокольного этажа.	Масштаб	Лист	Листов
	1:50	2	46

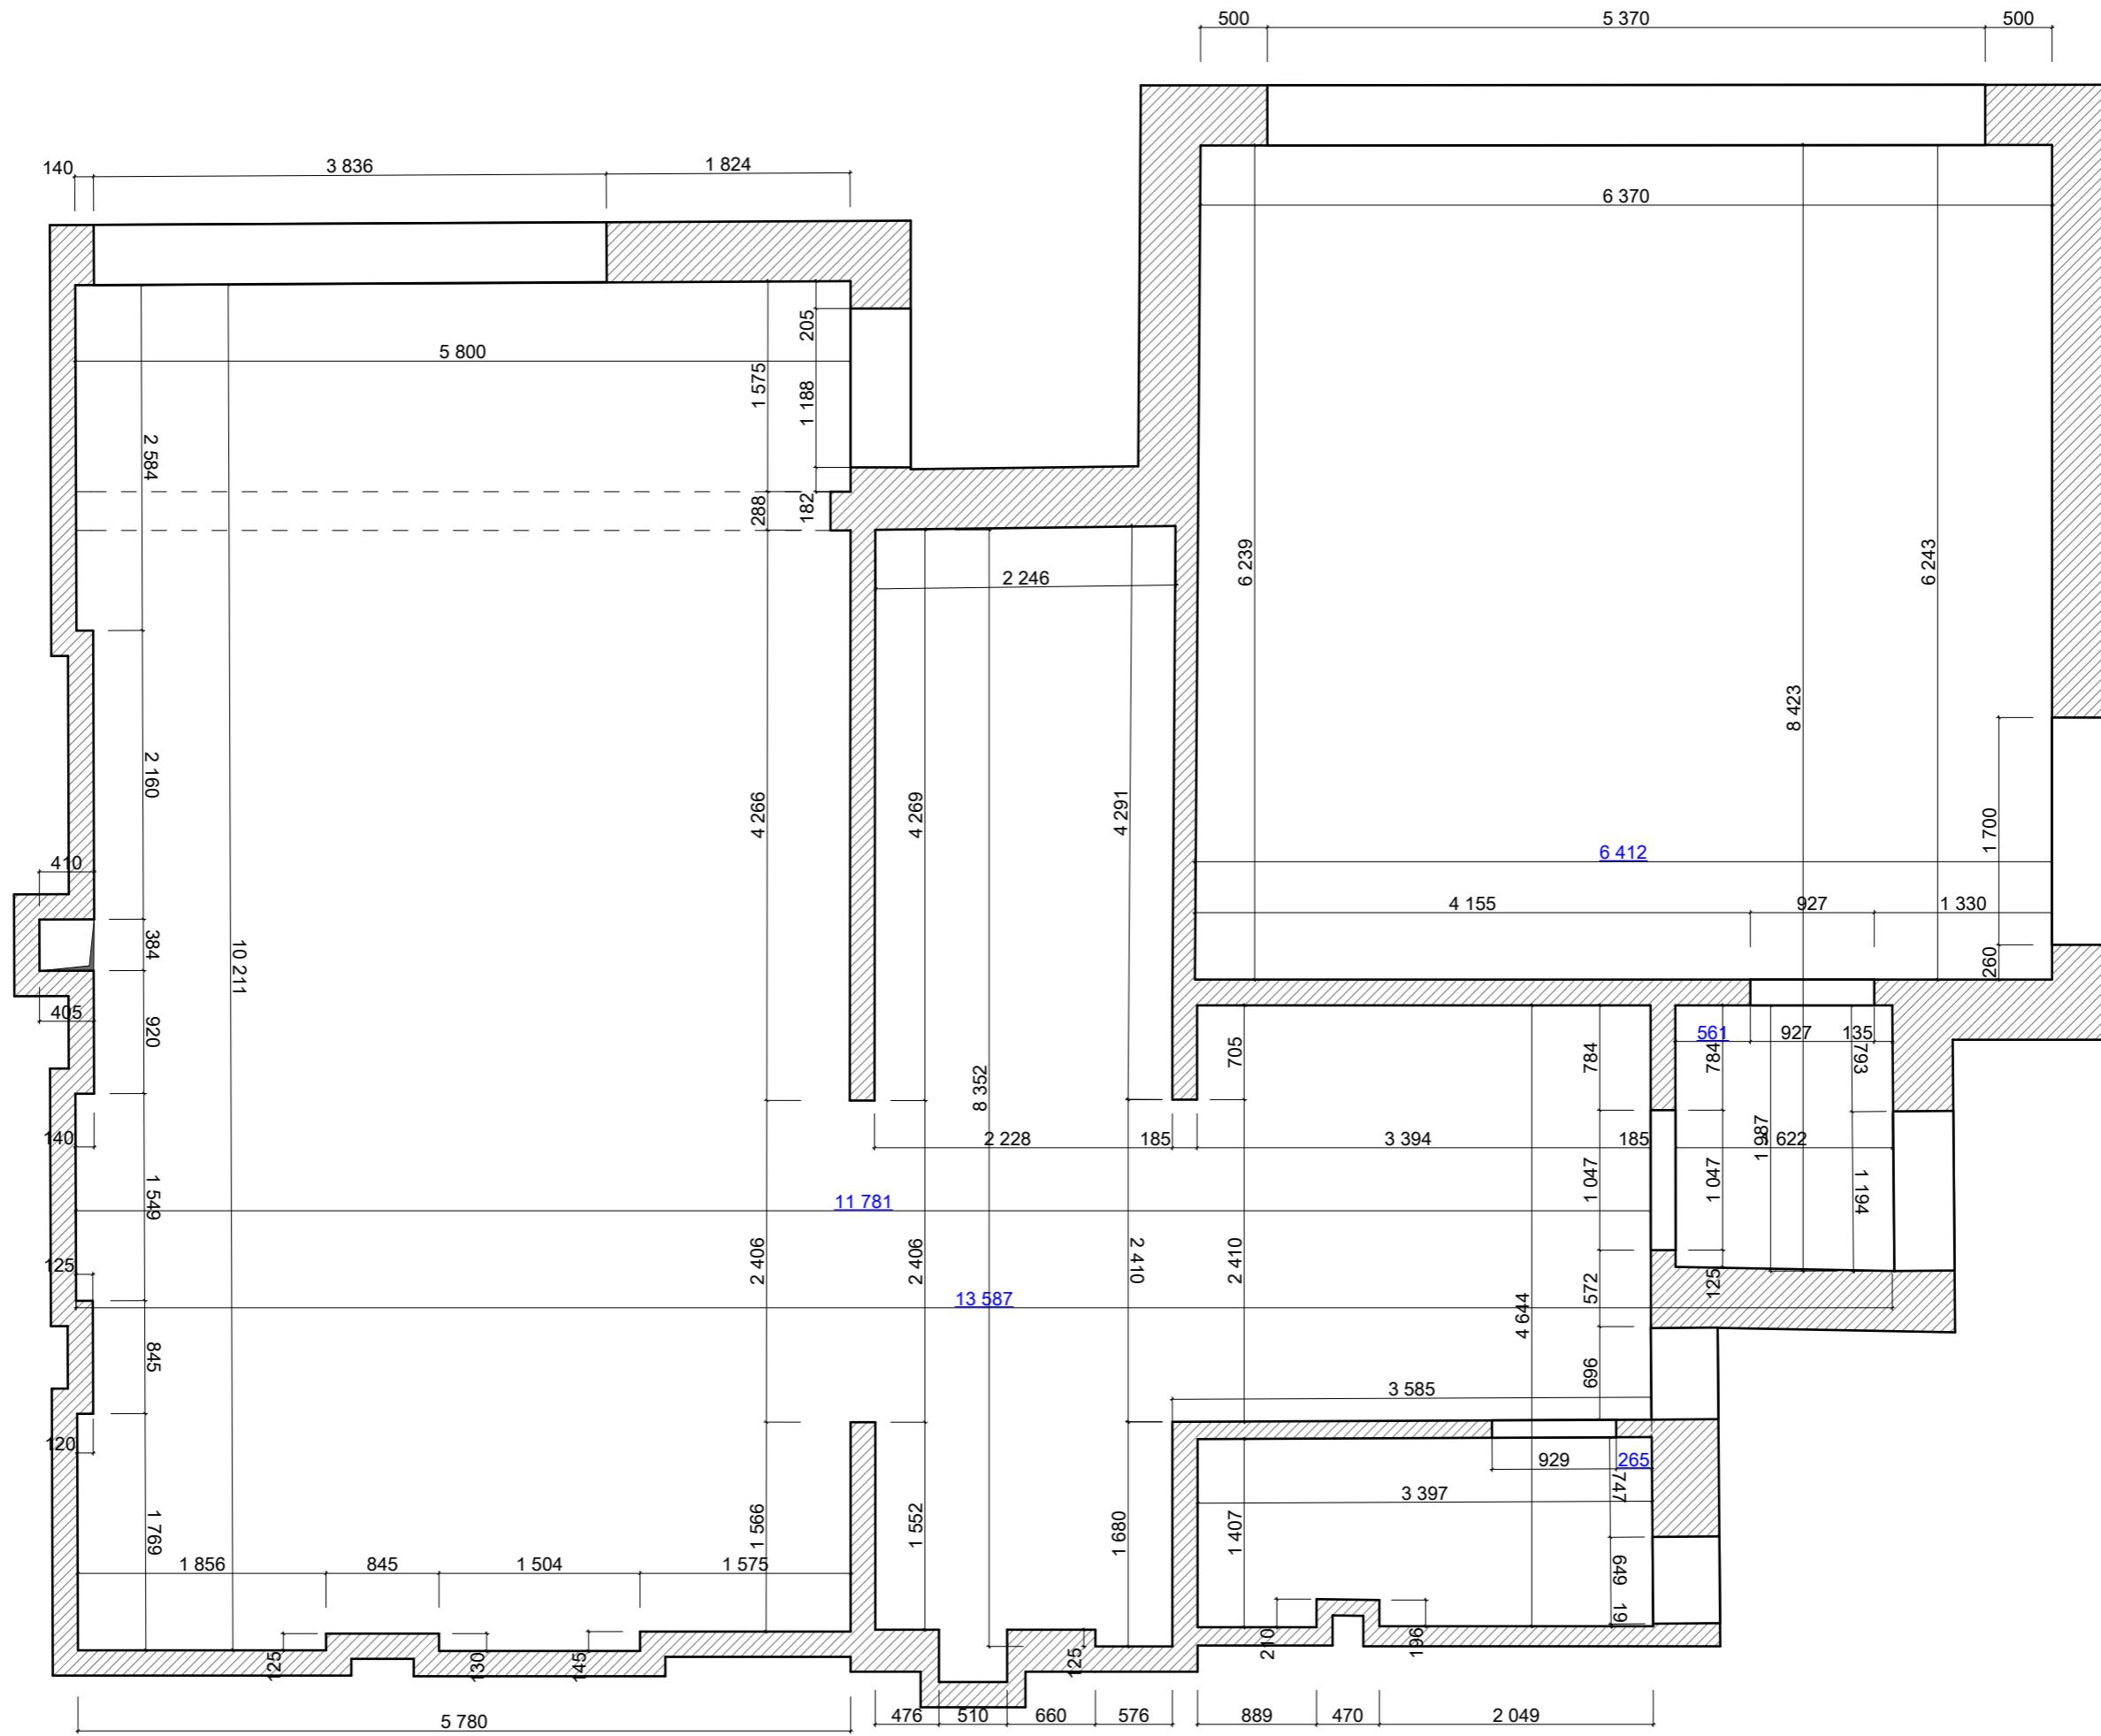


Обмерный план 1го этажа.

Обмерный план 1го этажа.	Масштаб	Лист	Листов
	1:50	3	46

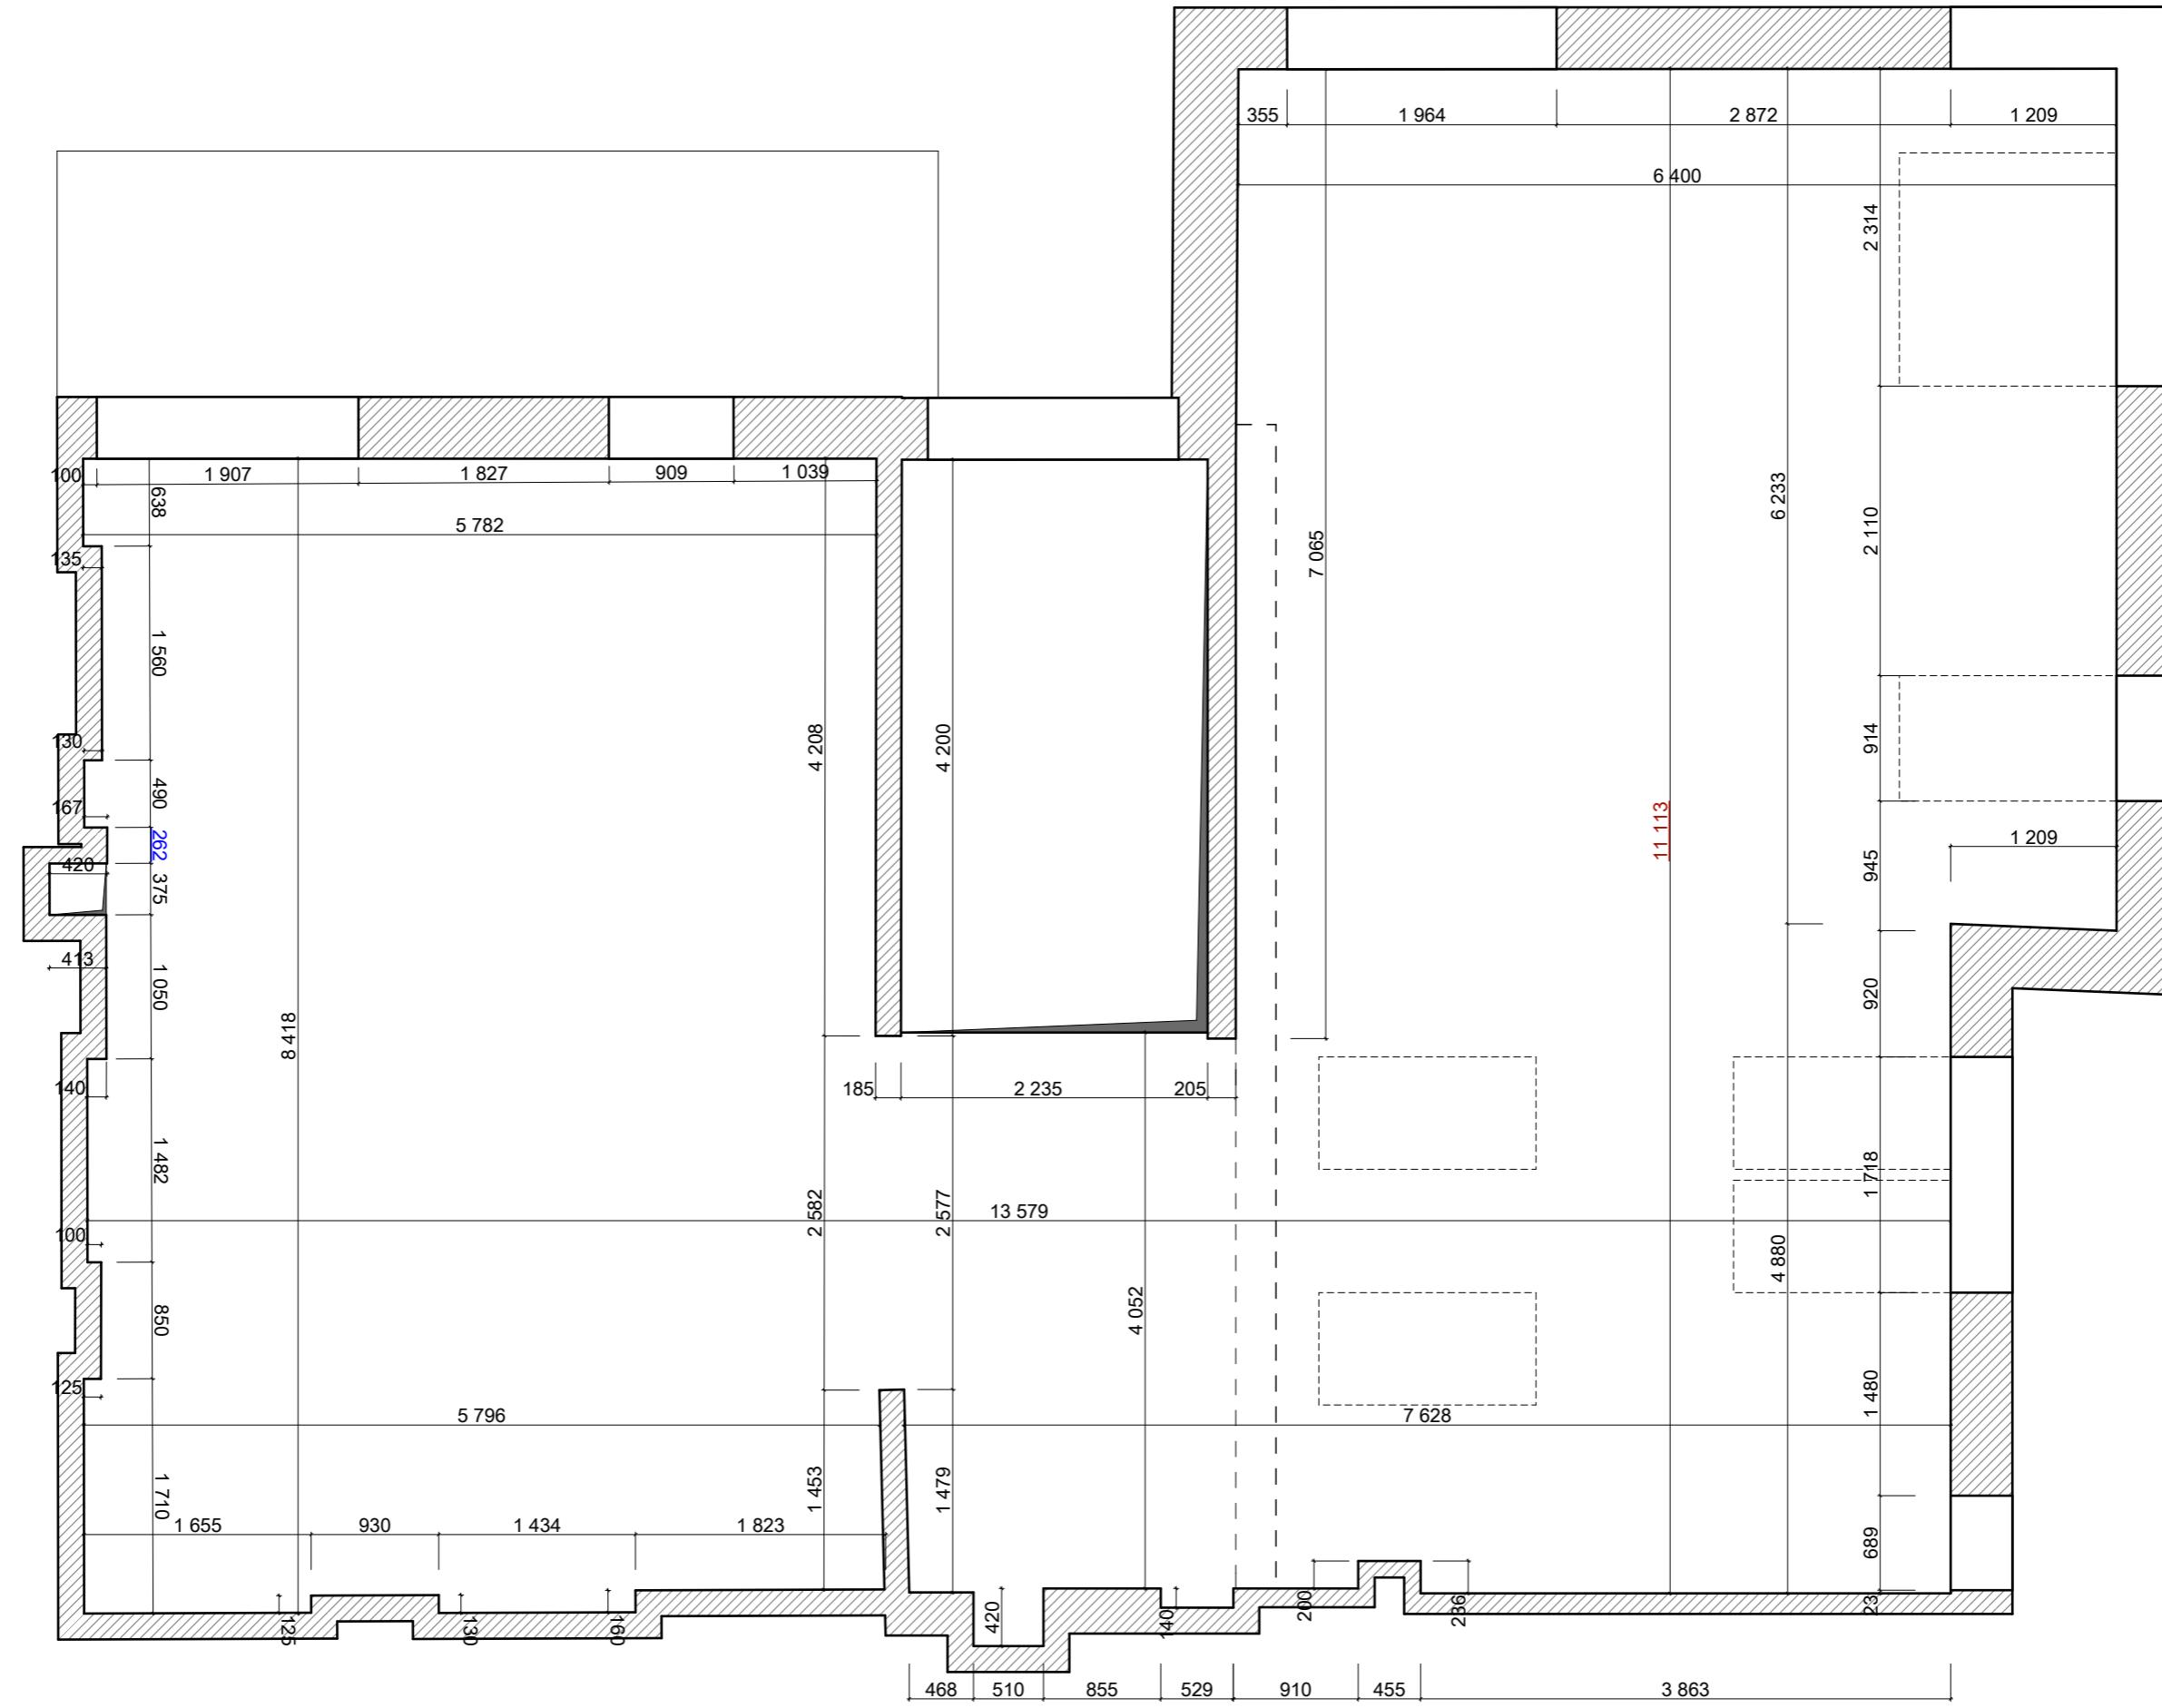


Обмерный план 2го этажа.

Масштаб	Лист	Листов
1:50	4	46

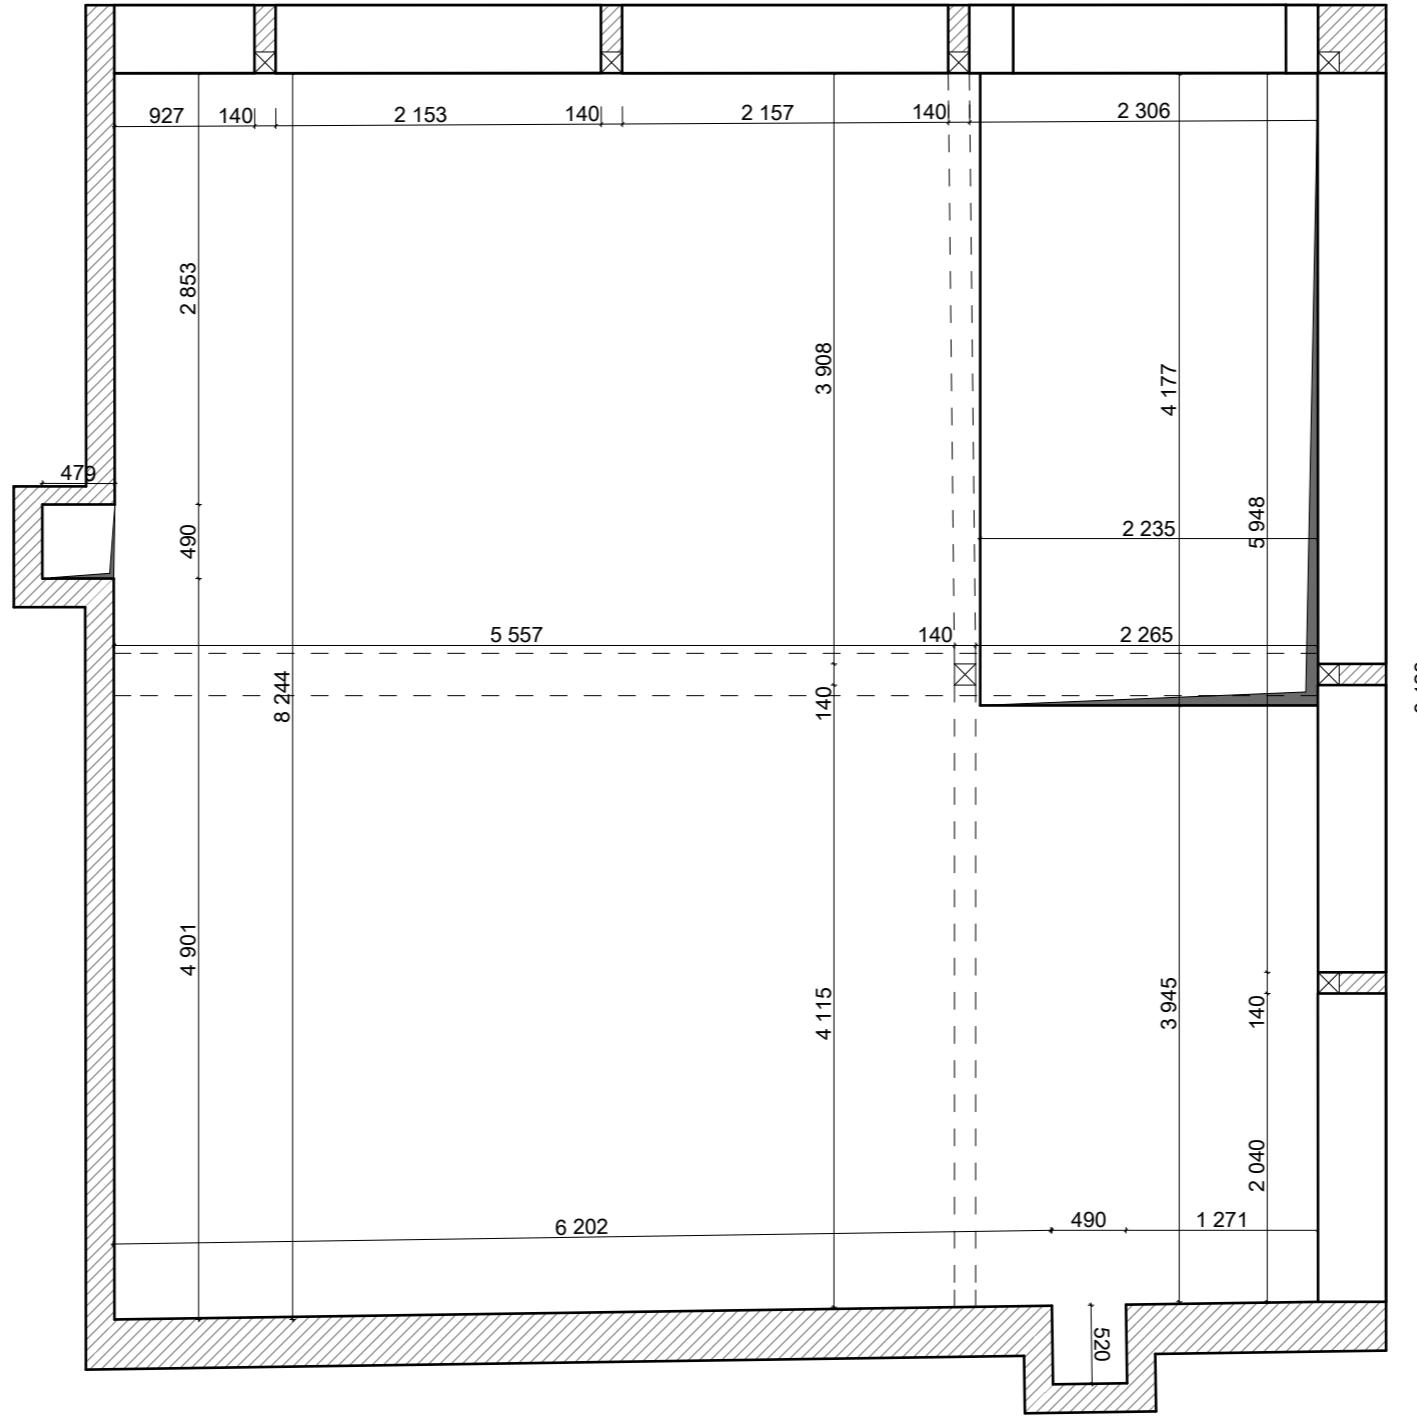

Обмерный план мансардного этажа.

Обмерный план мансардного этажа.	Масштаб	Лист	Листов
	1:50	5	46

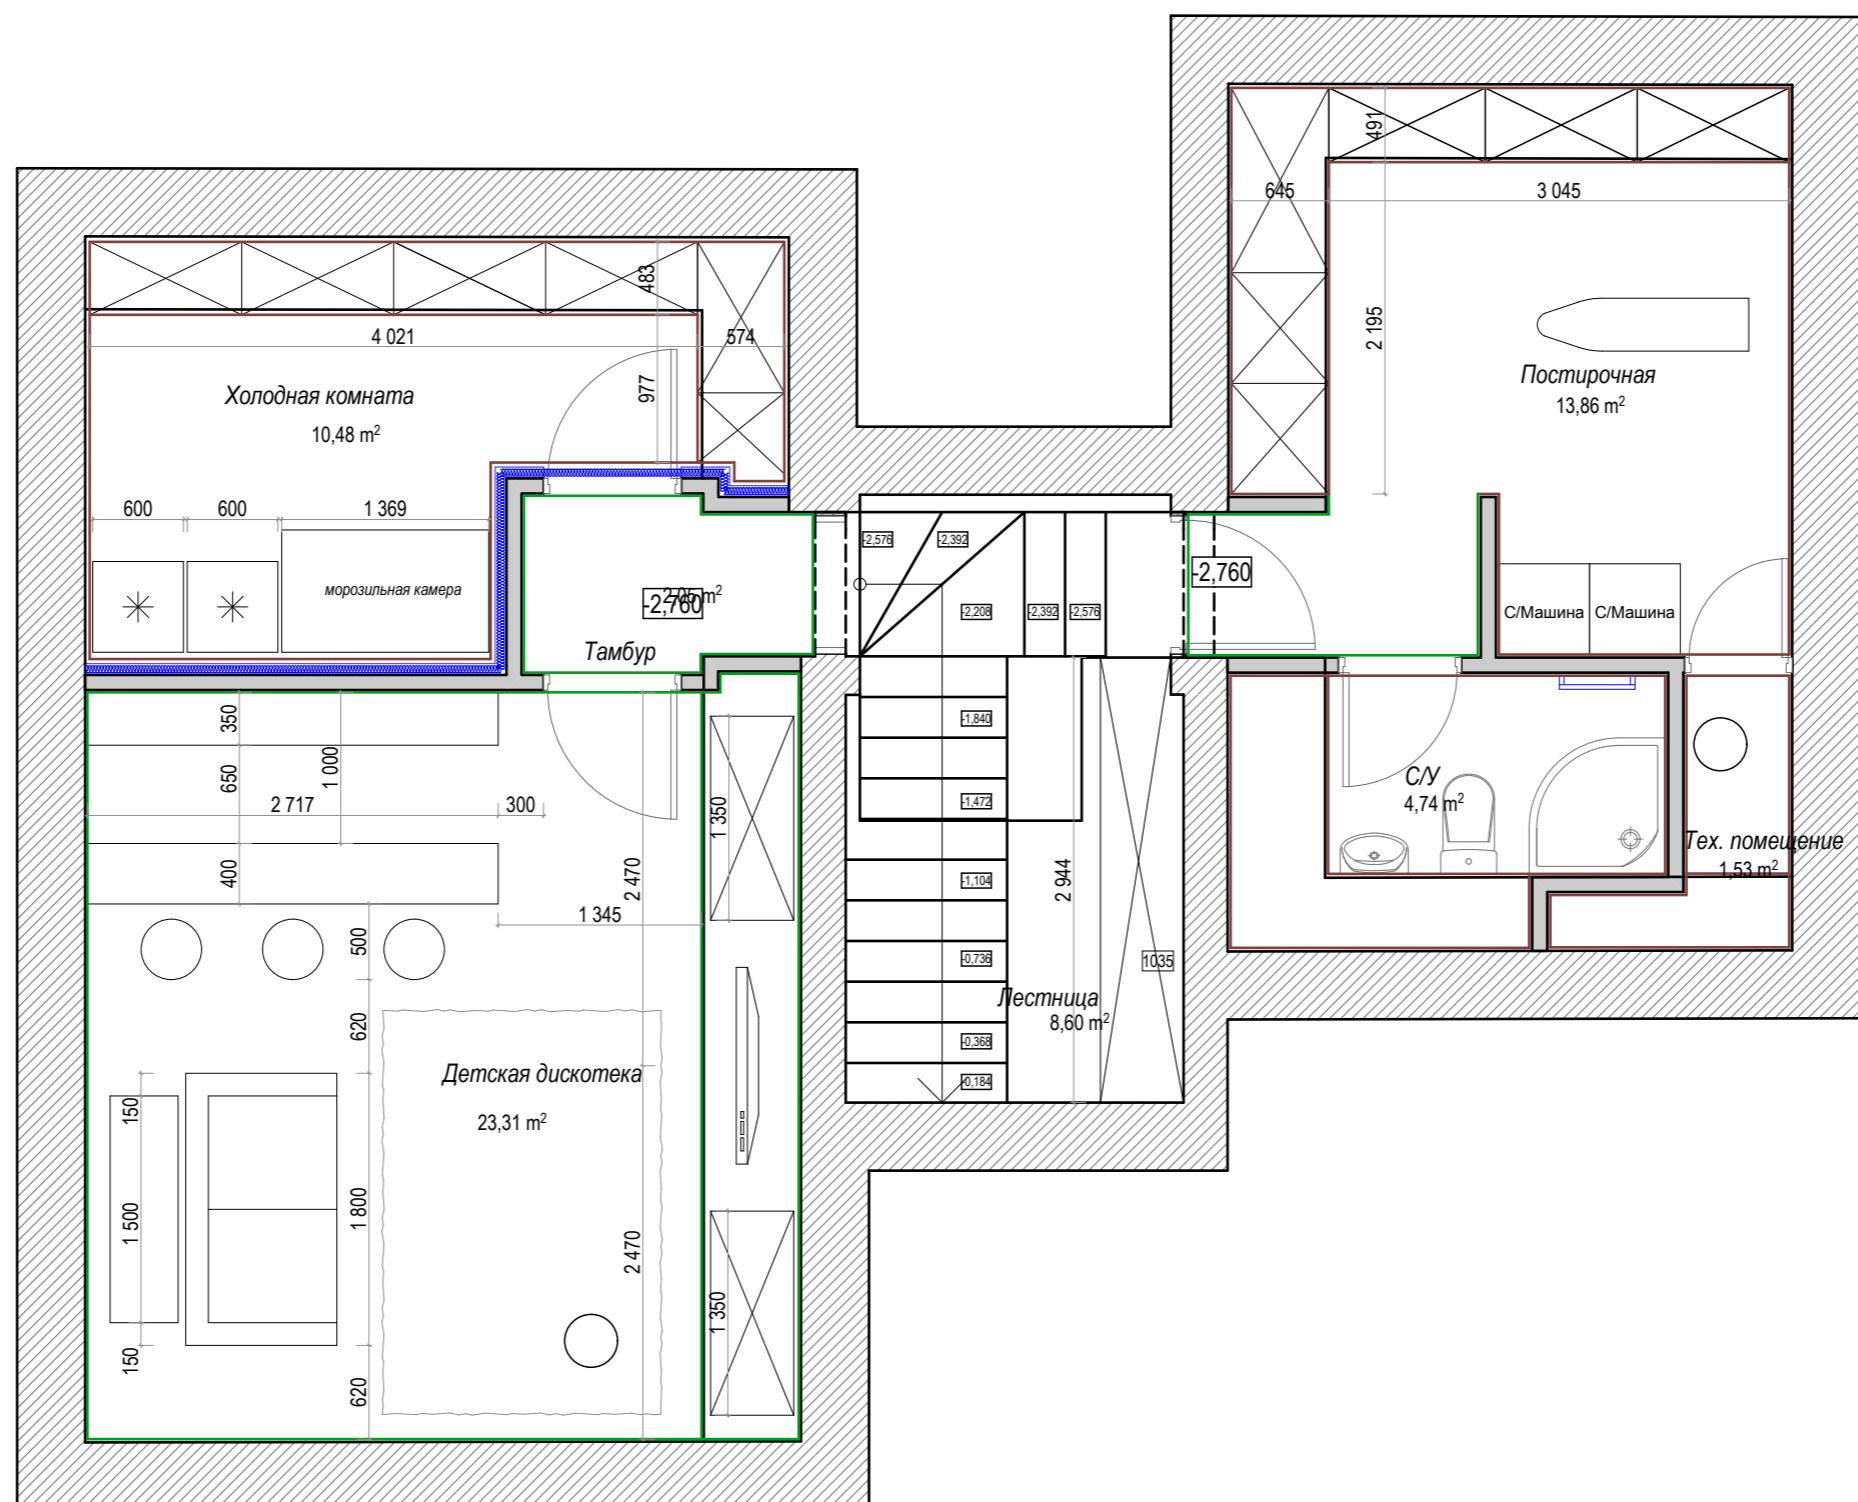



Экспликация помещений

№	Помещение	Площадь
1	Детская дискотека	23,31 m ²
2	Холодная комната	10,48 m ²
3	Тамбур	2,05 m ²
4	Постирочная	13,86 m ²
5	Лестница	8,60 m ²
6	С/У	4,74 m ²
7	Тех. помещение	1,53 m ²
Общая площадь		64,57 m²

Планировочное решение цокольного этажа.

Планировочное решение цокольного этажа.	Масштаб	Лист	Листов
	1:50	6	46

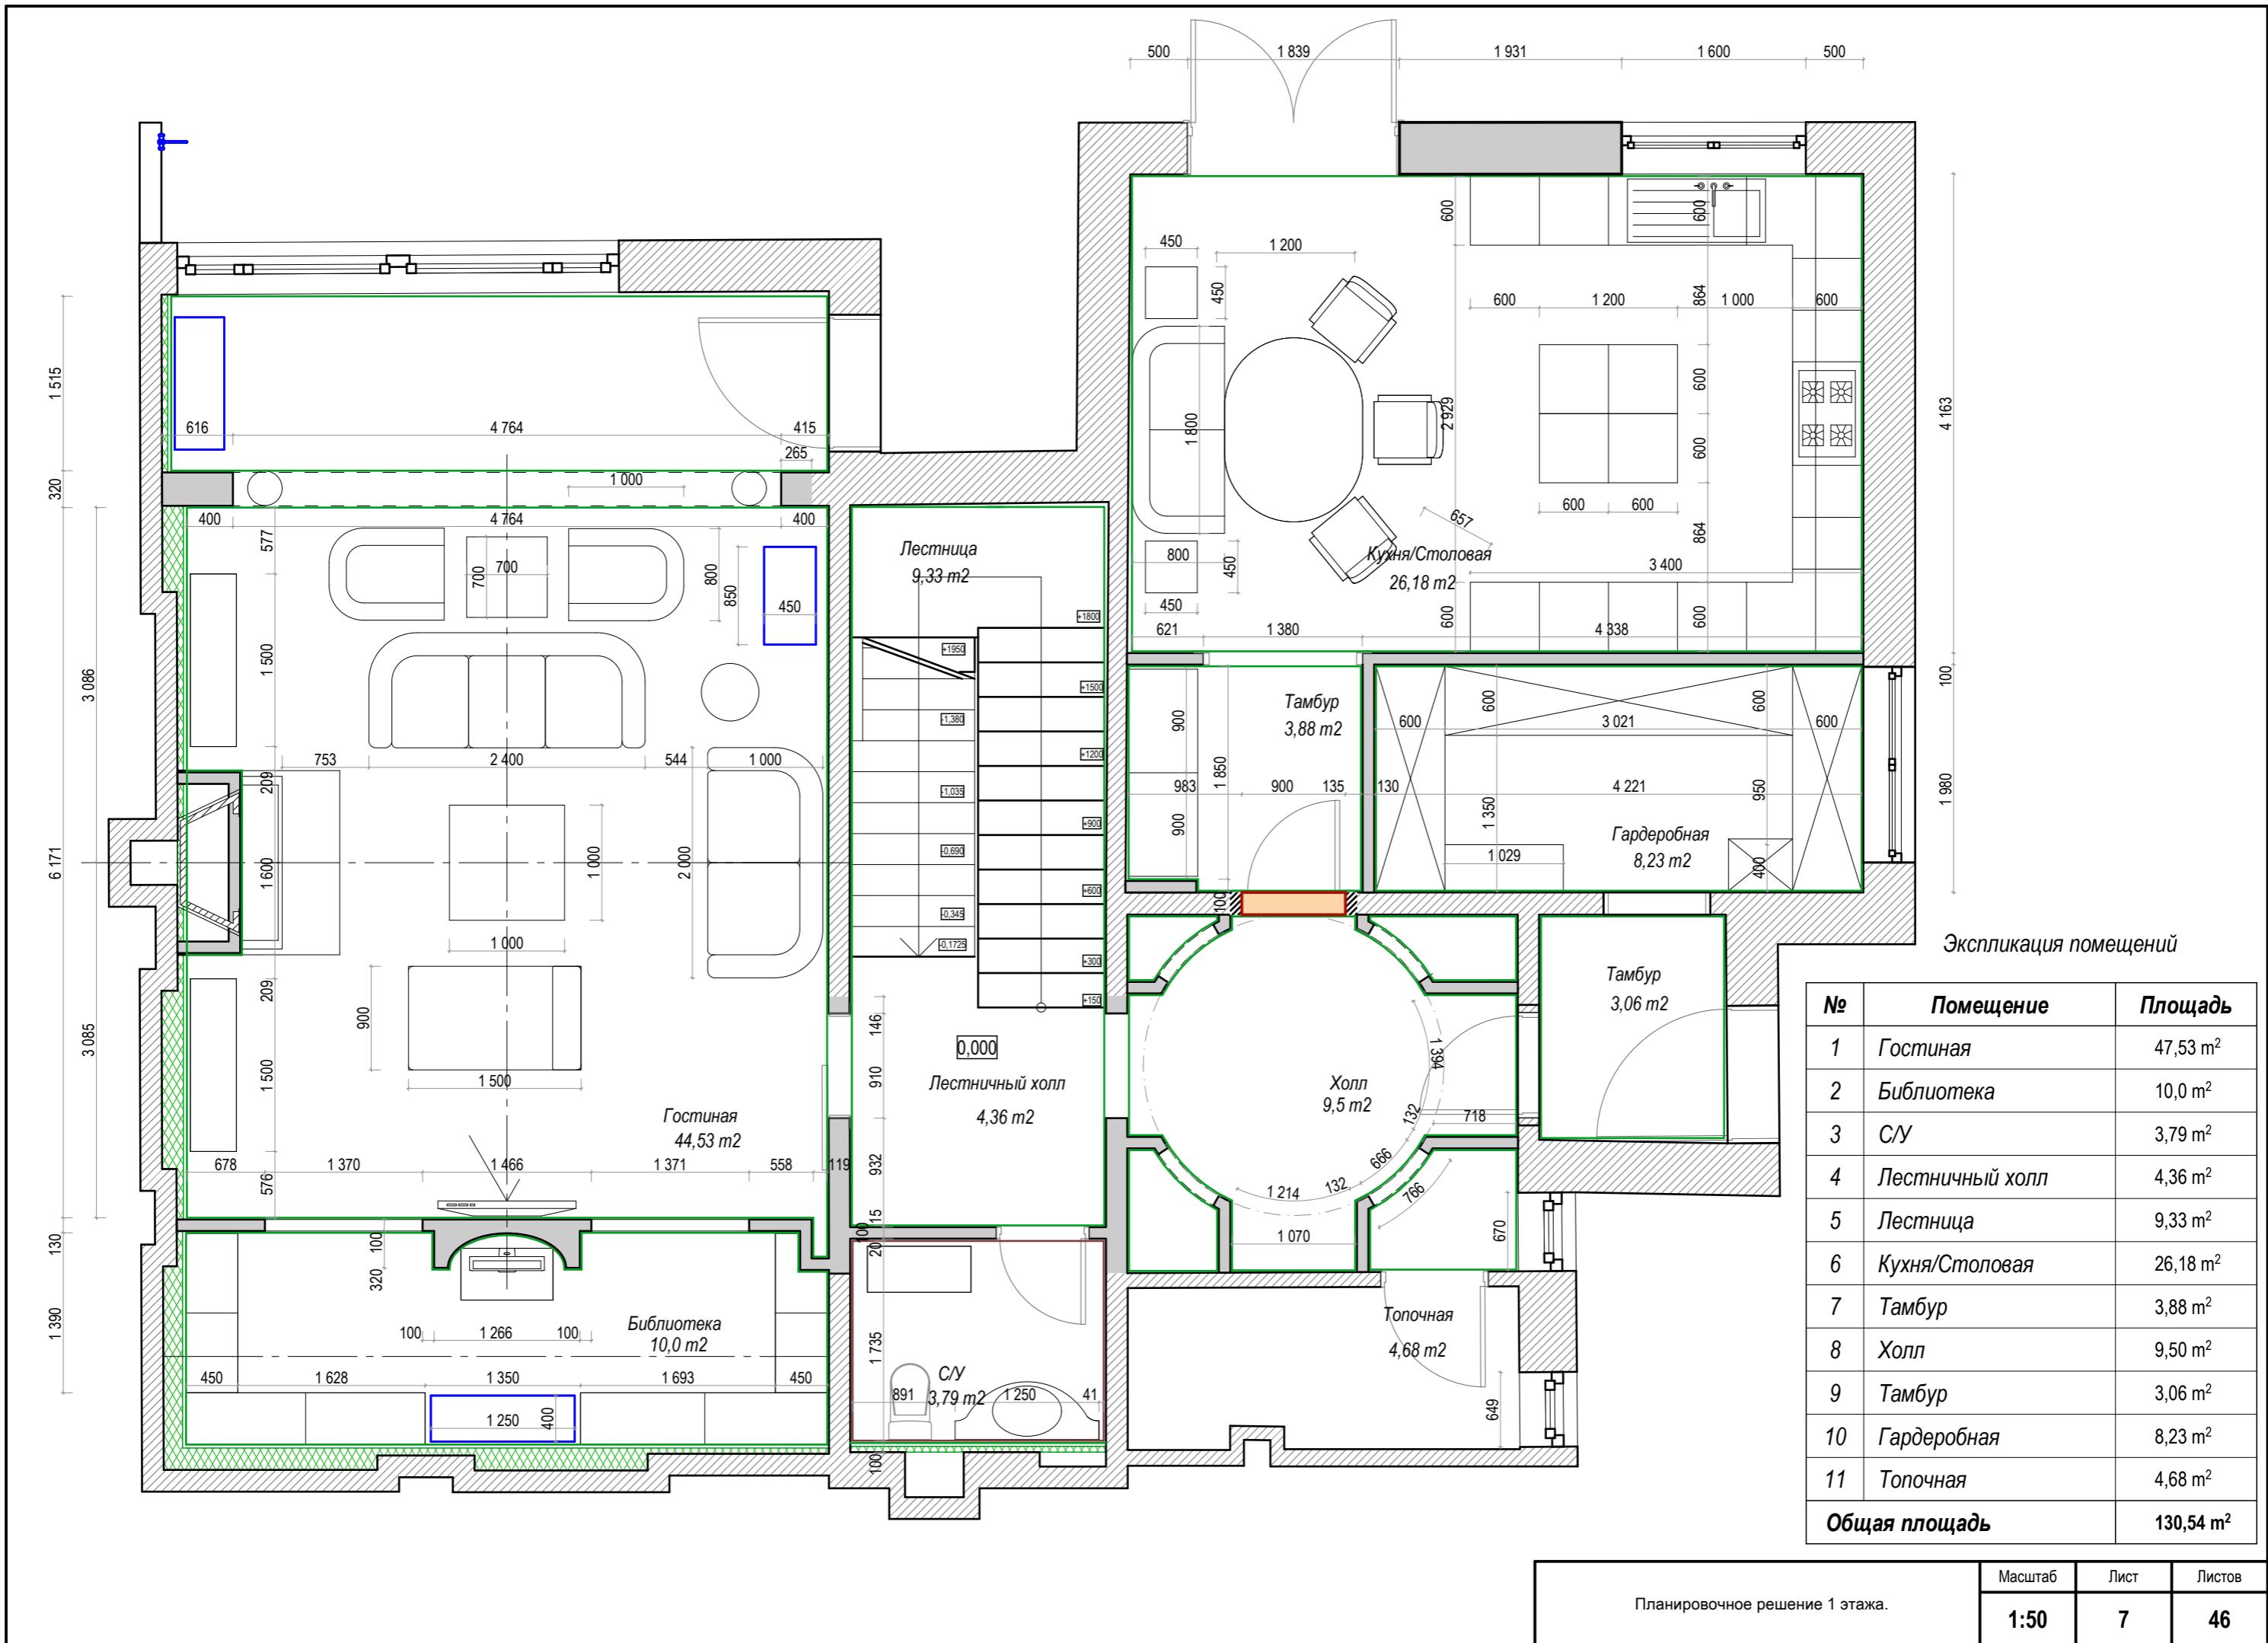

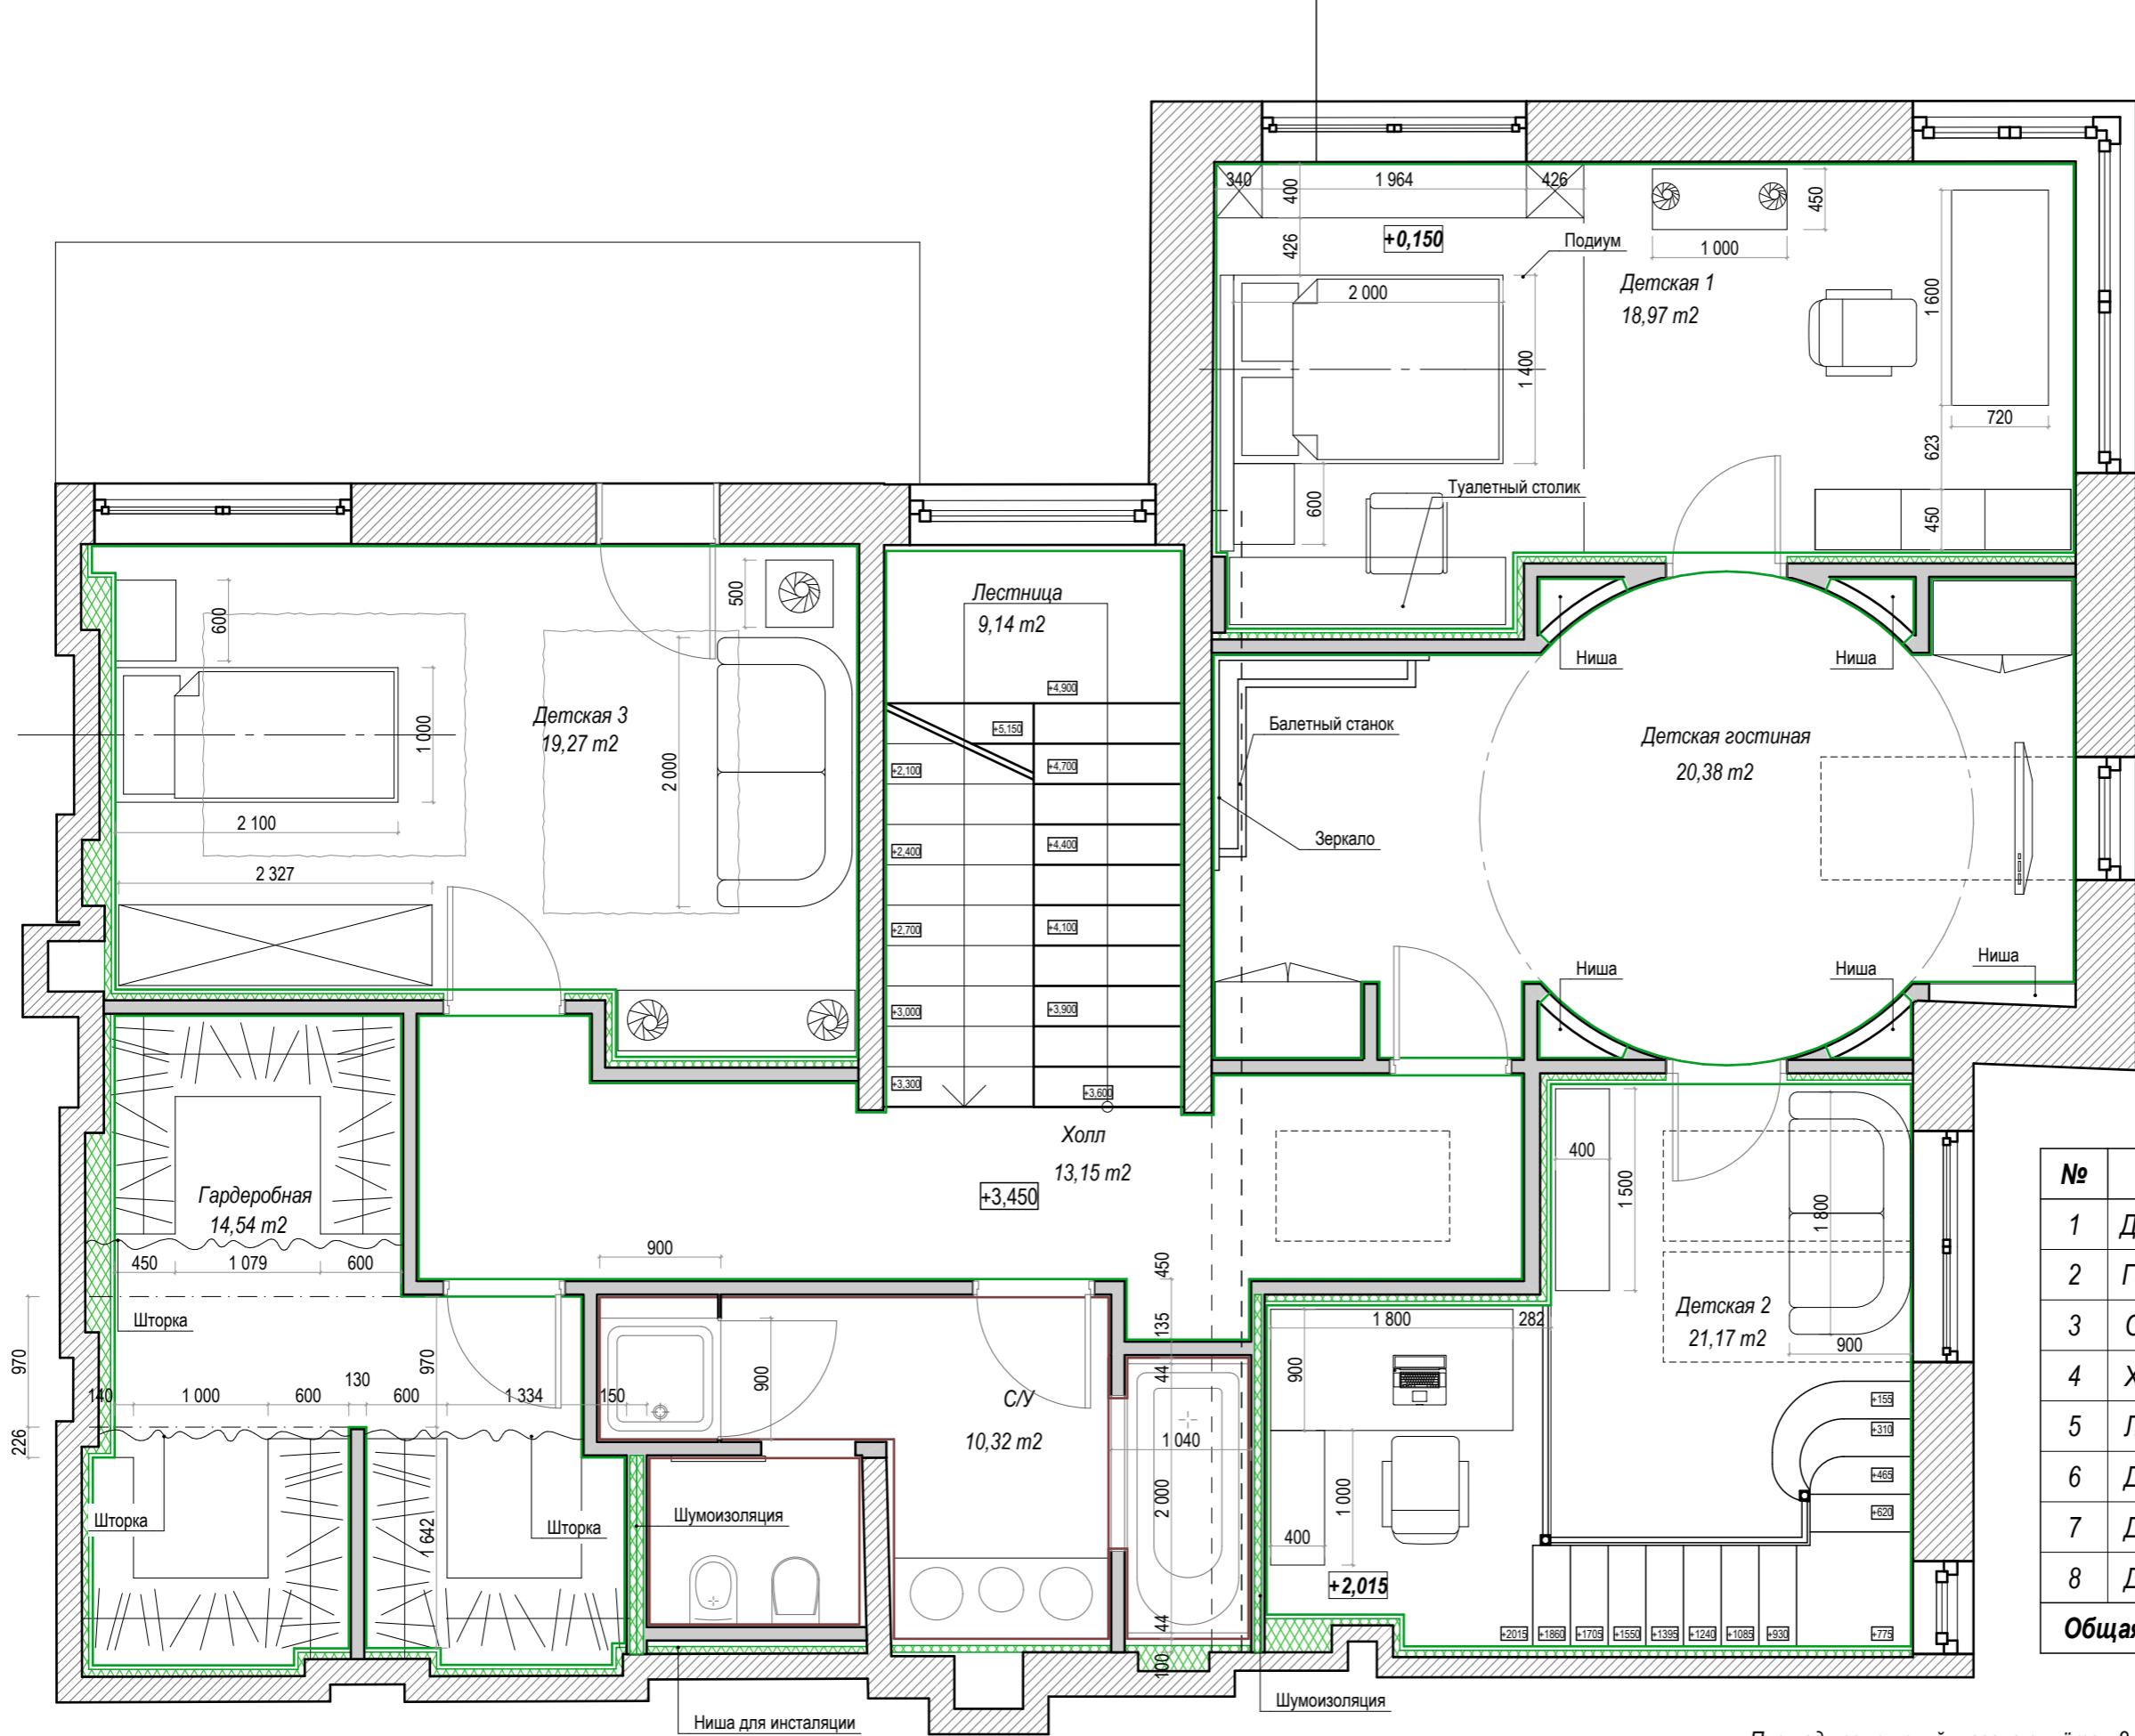


Экспликация помещений


№	Помещение	Площадь
1	Детская 3	19,27 м ²
2	Гардеробная	14,54 м ²
3	С/У	10,32 м ²
4	Холл	13,15 м ²
5	Лестница	9,14 м ²
6	Детская 1	18,97 м ²
7	Детская гостиная	20,38 м ²
8	Детская 2	21,17 м ²
Общая площадь		126,94 м ²

Площадь помещений указана с учётом 2х уровней в помещении "Детской2"

A1-A⁺

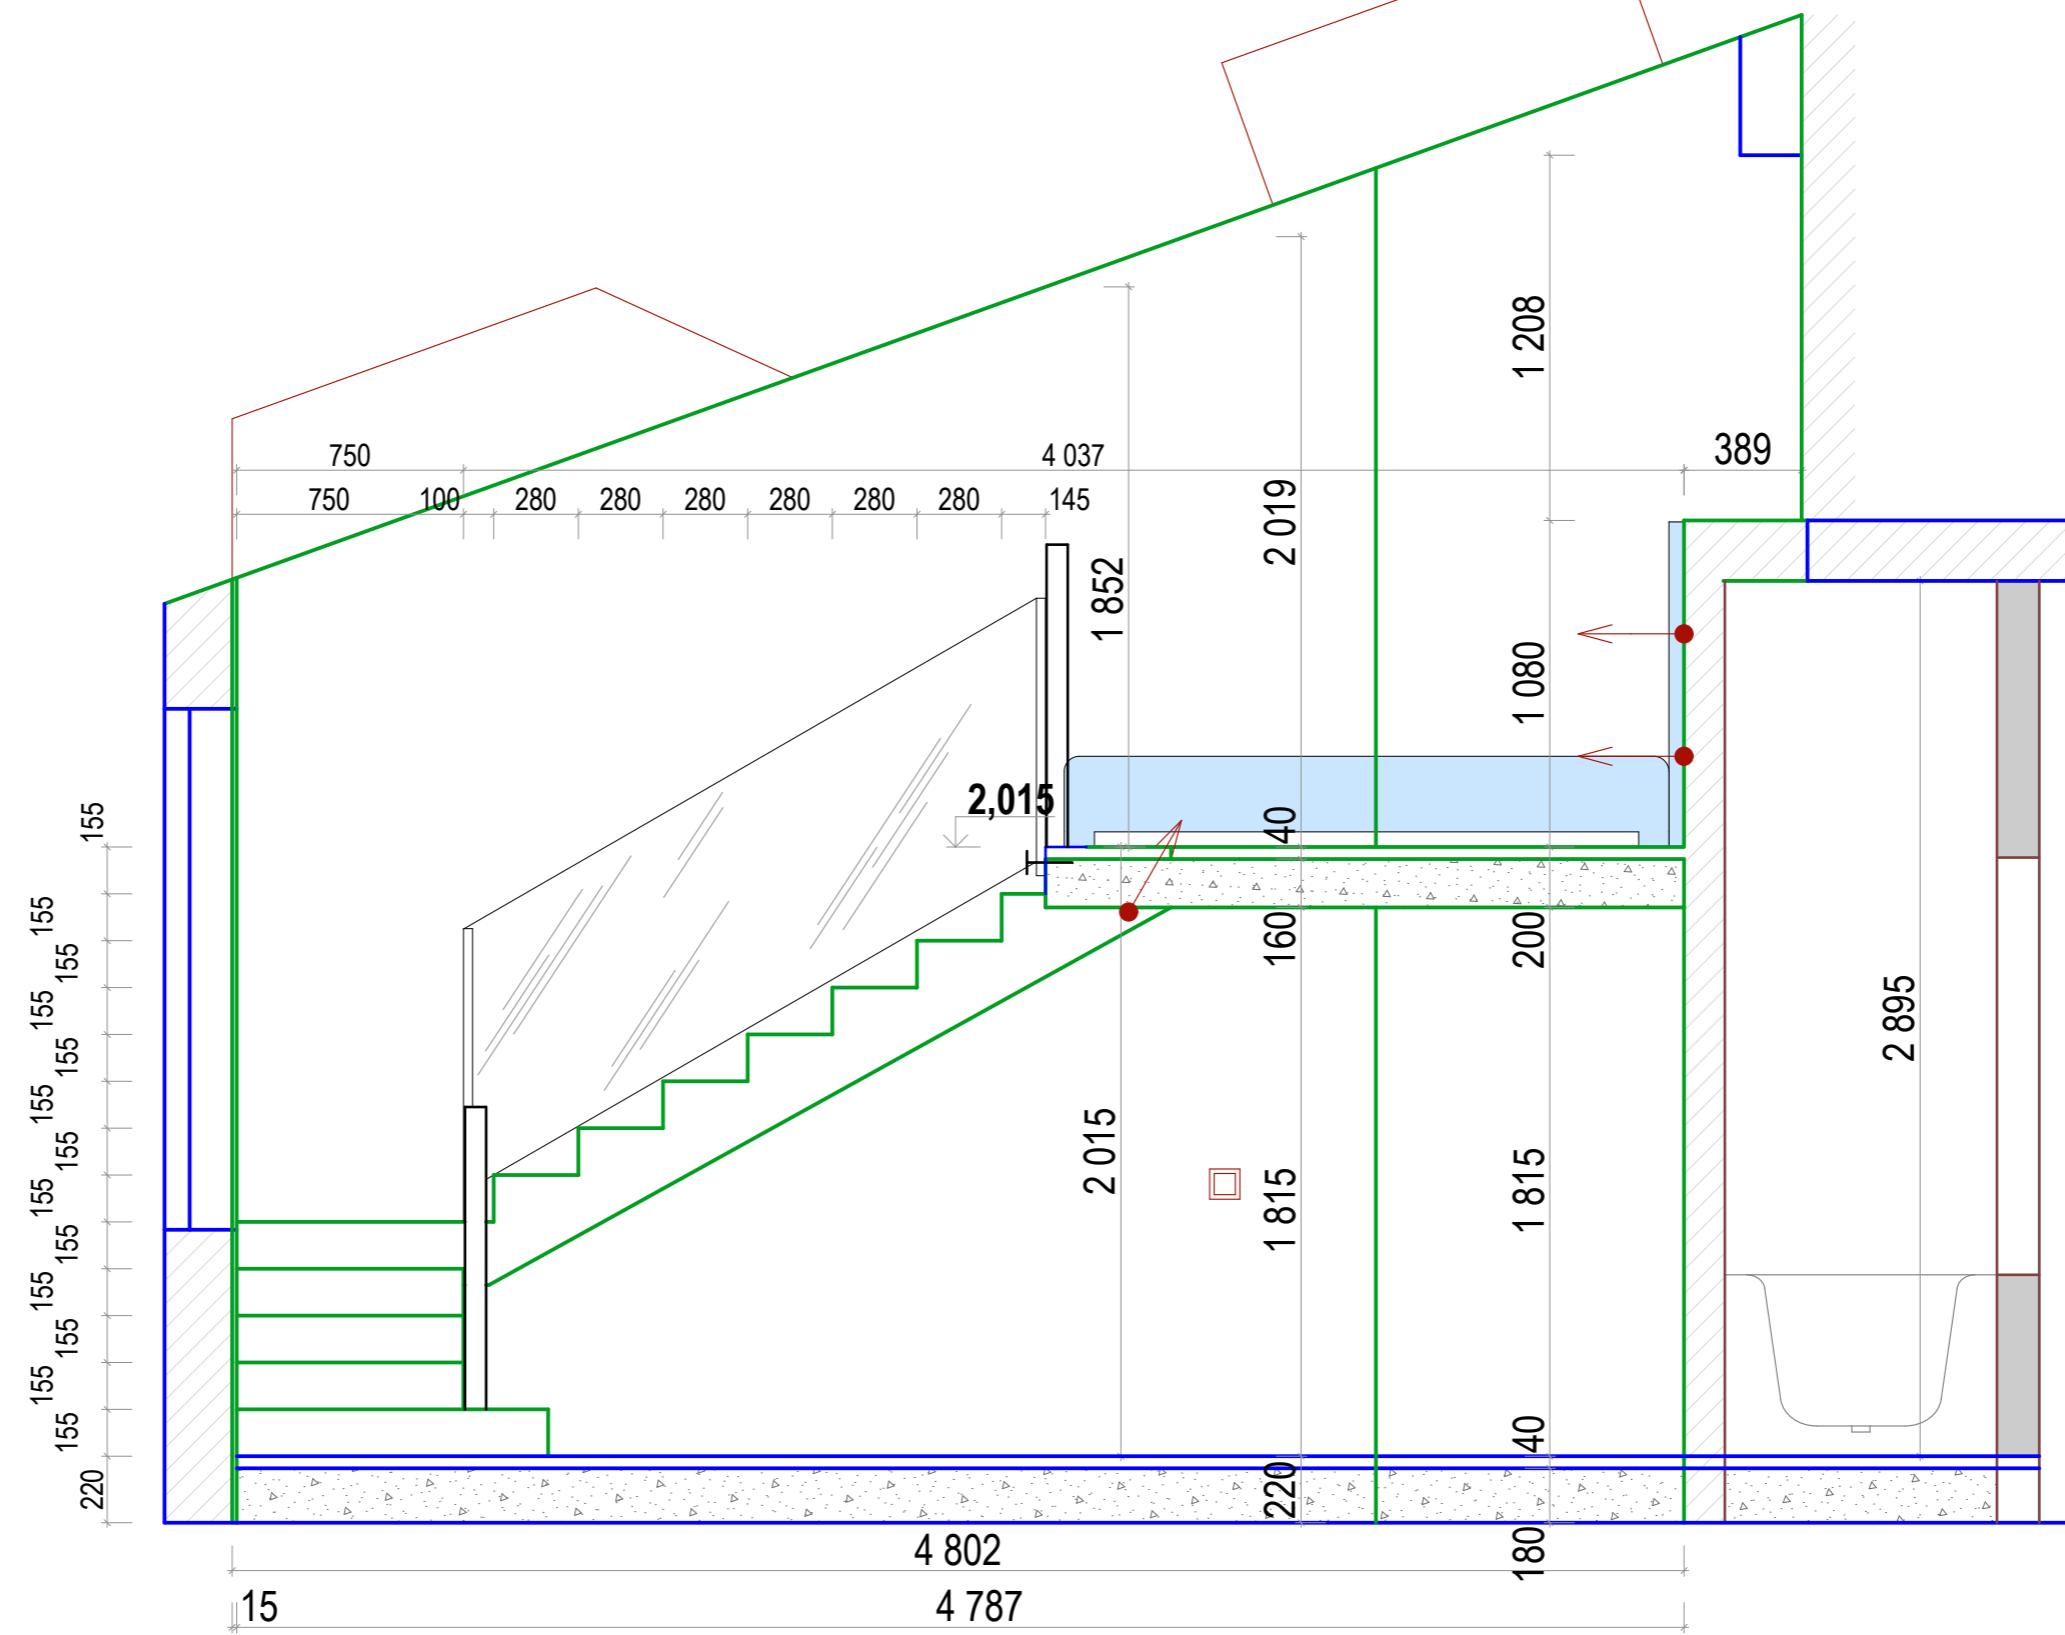



Сечение A1-A1	Масштаб	Лист	Листов
	1:25	9	46

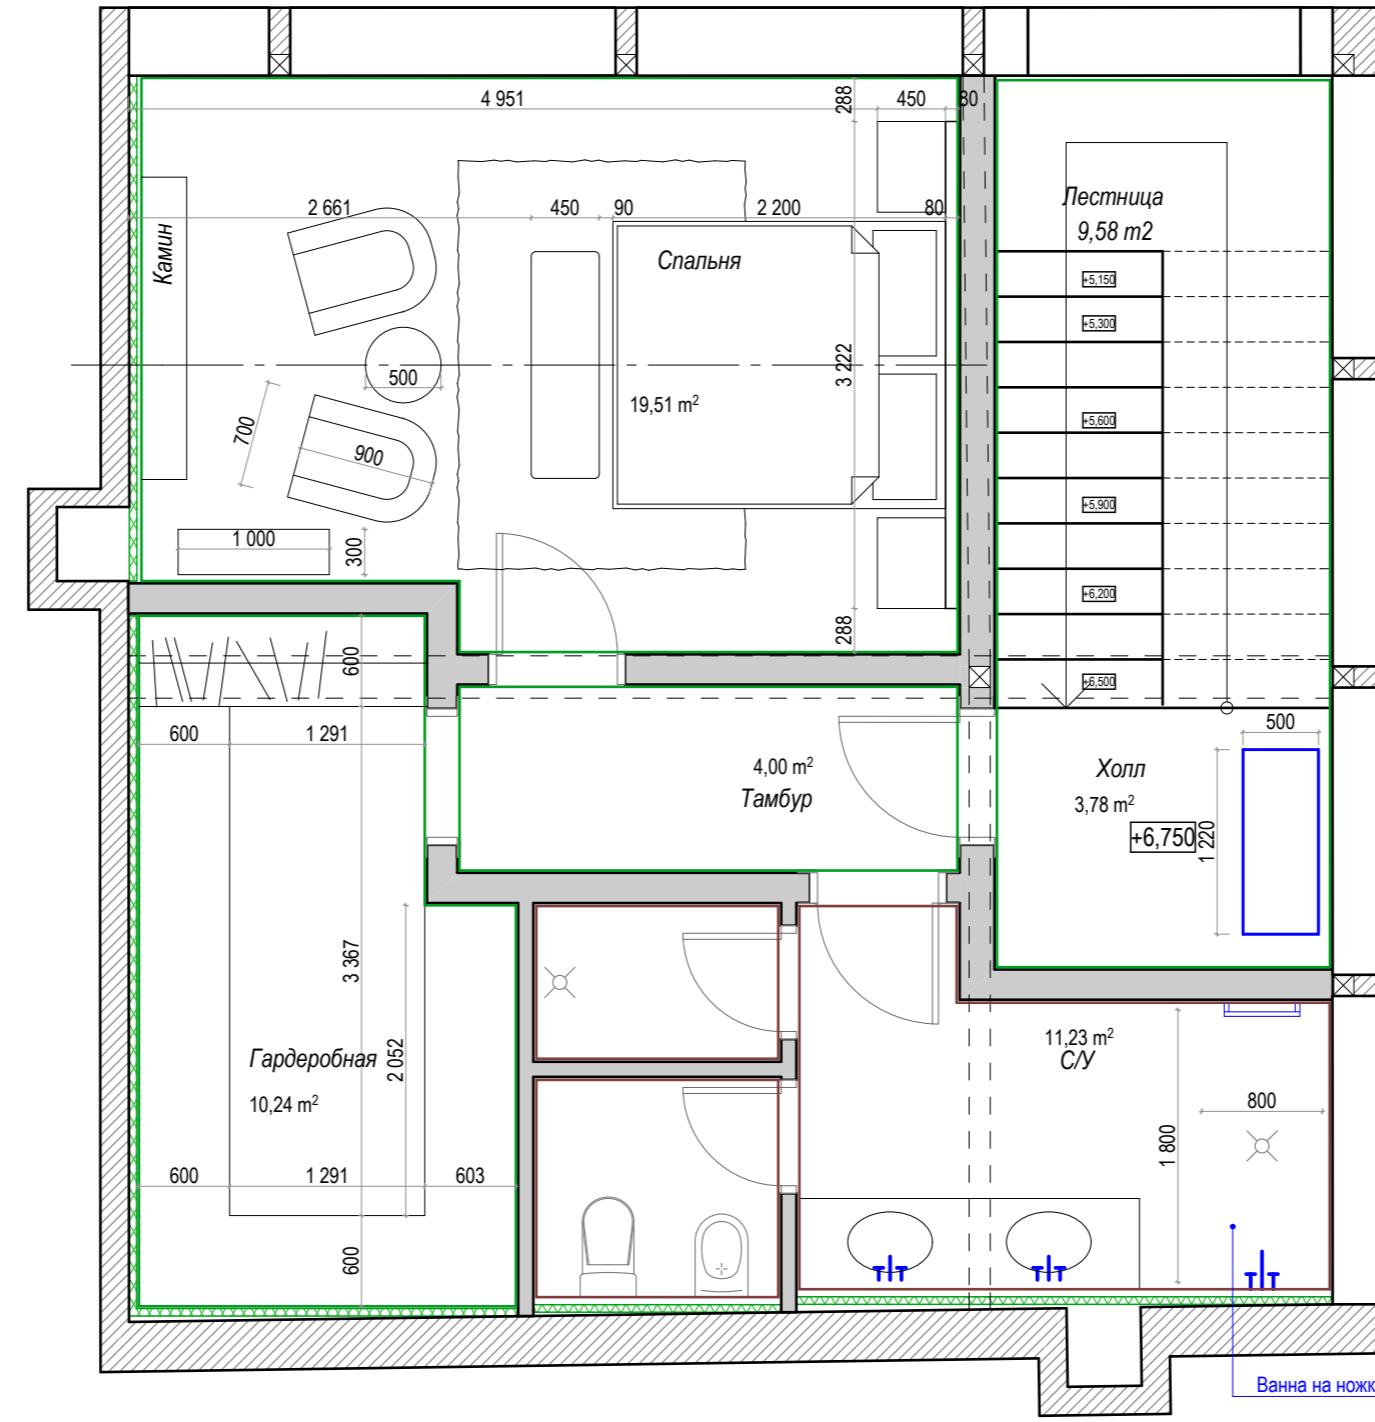

Экспликация помещений

№	Помещение	Площадь
1	Спальня	19,51 m ²
2	Гардеробная	10,24 m ²
3	С/У	11,23 m ²
4	Тамбур	4,00 m ²
5	Лестница	9,58 m ²
6	Холл	3,78 m ²
Общая площадь		58,34 m ²



Условные обозначения:

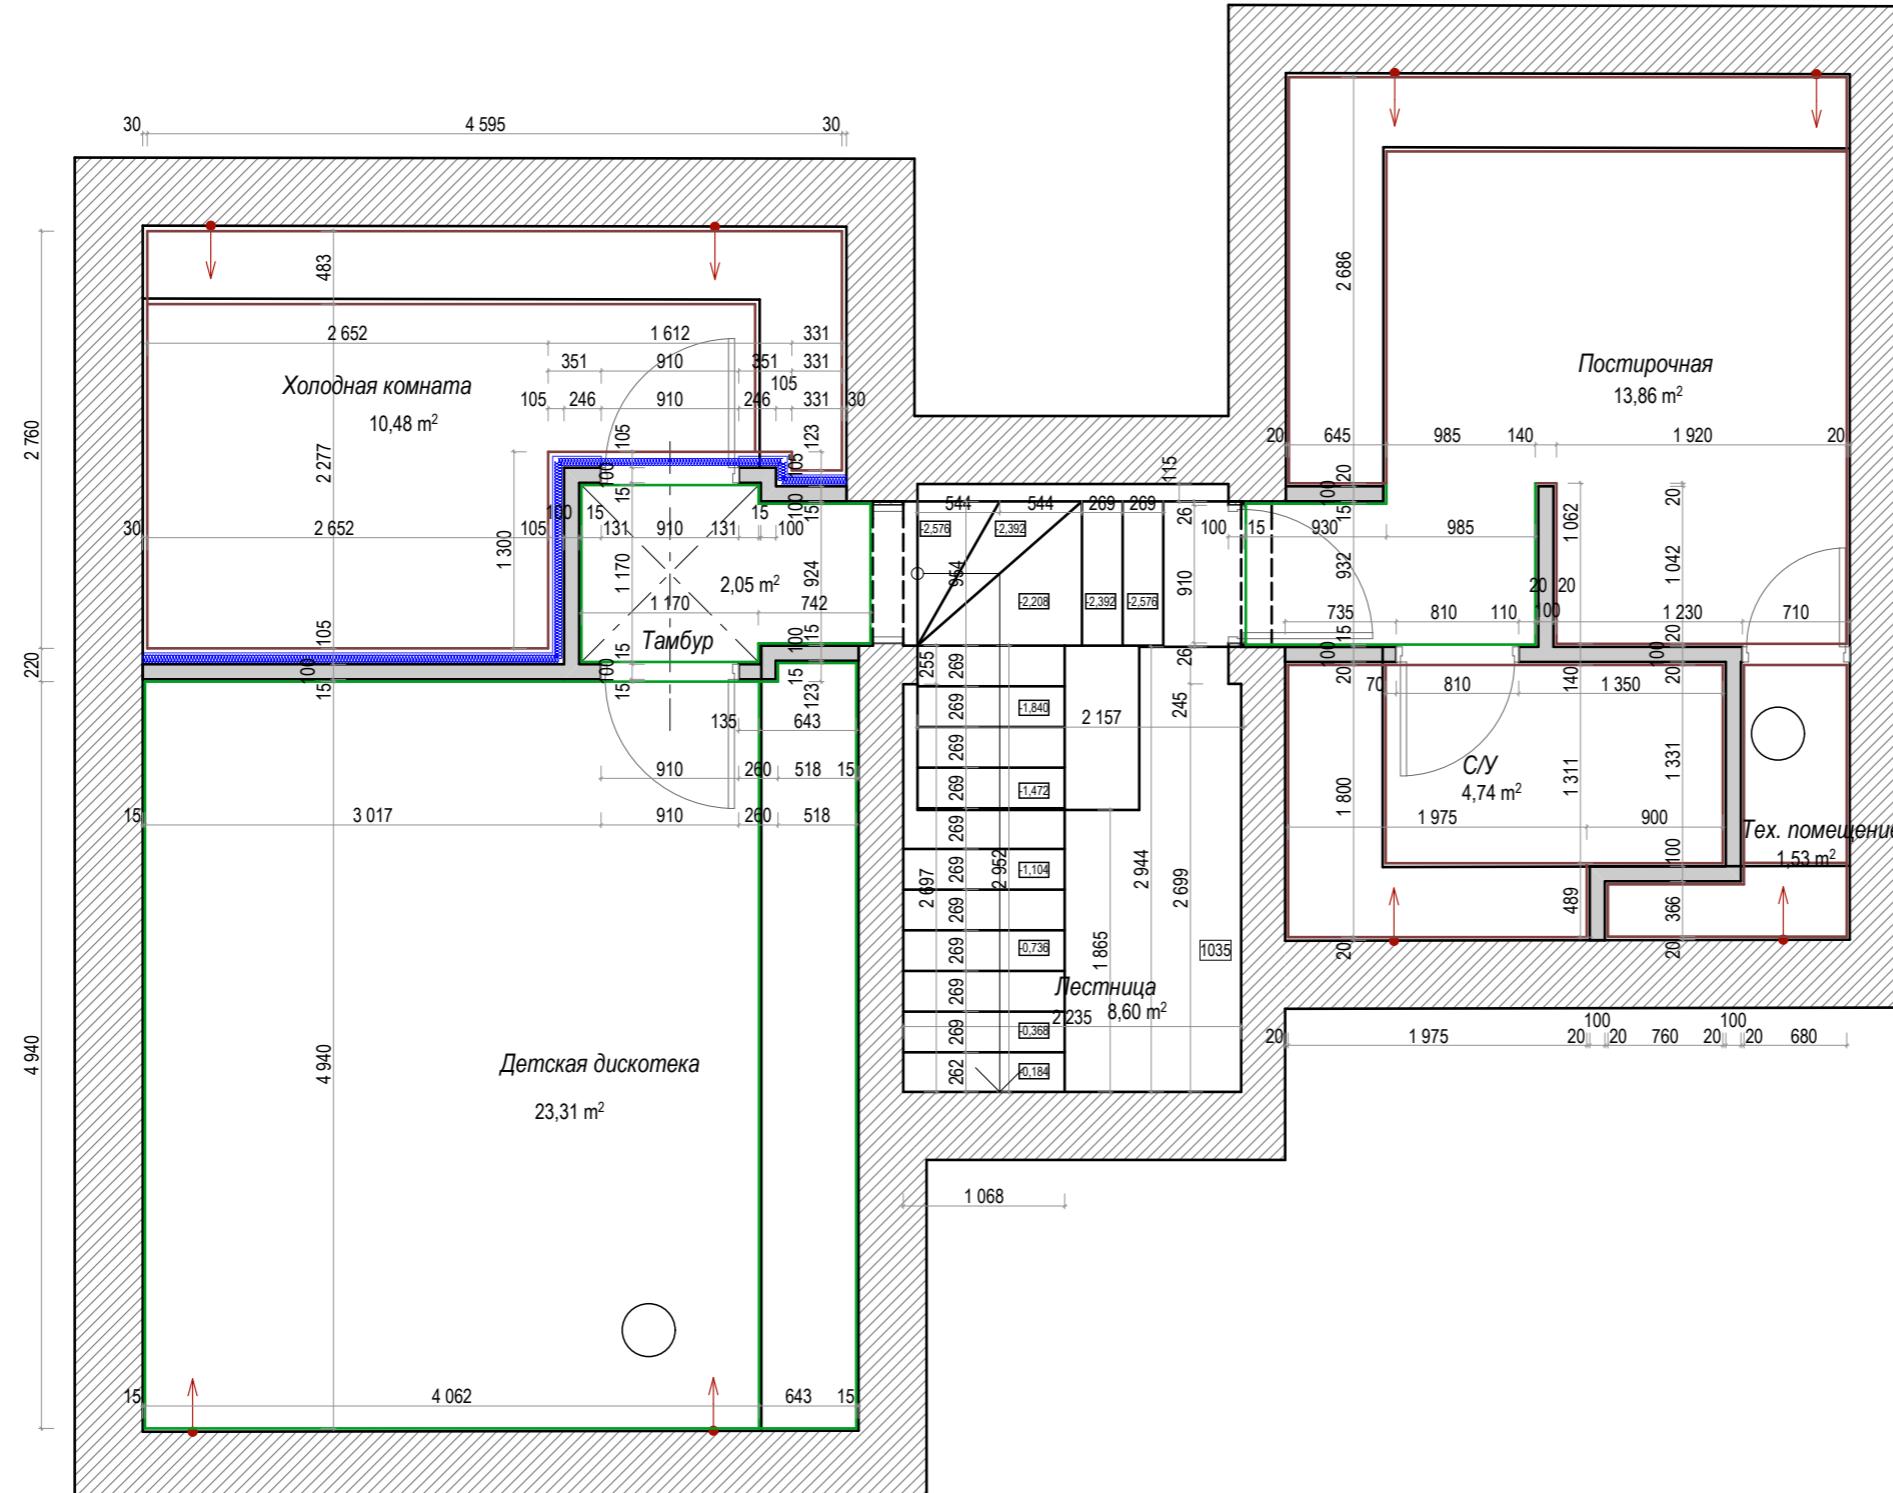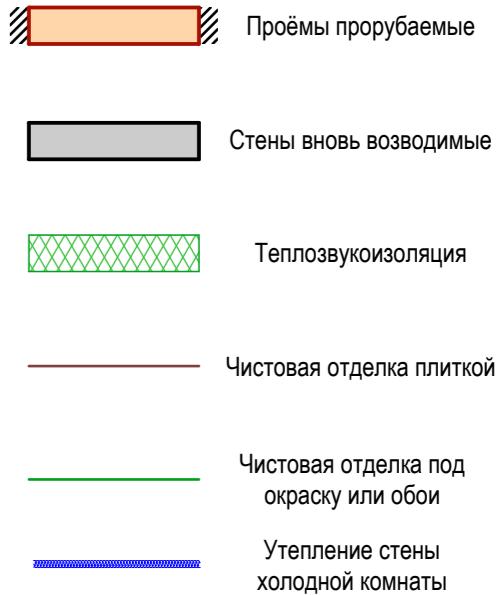


План сносимых и возводимых стен цокольного этажа.

План сносимых и возводимых стен цокольного этажа.	Масштаб	Лист	Листов
	1:50	11	46

Условные обозначения:

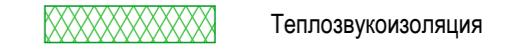
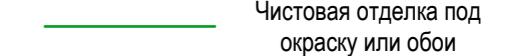
-  Проёмы прорубаемые
-  Стены вновь возводимые
-  Теплозвукоизоляция
-  Чистовая отделка плиткой
-  Чистовая отделка под окраску или обои

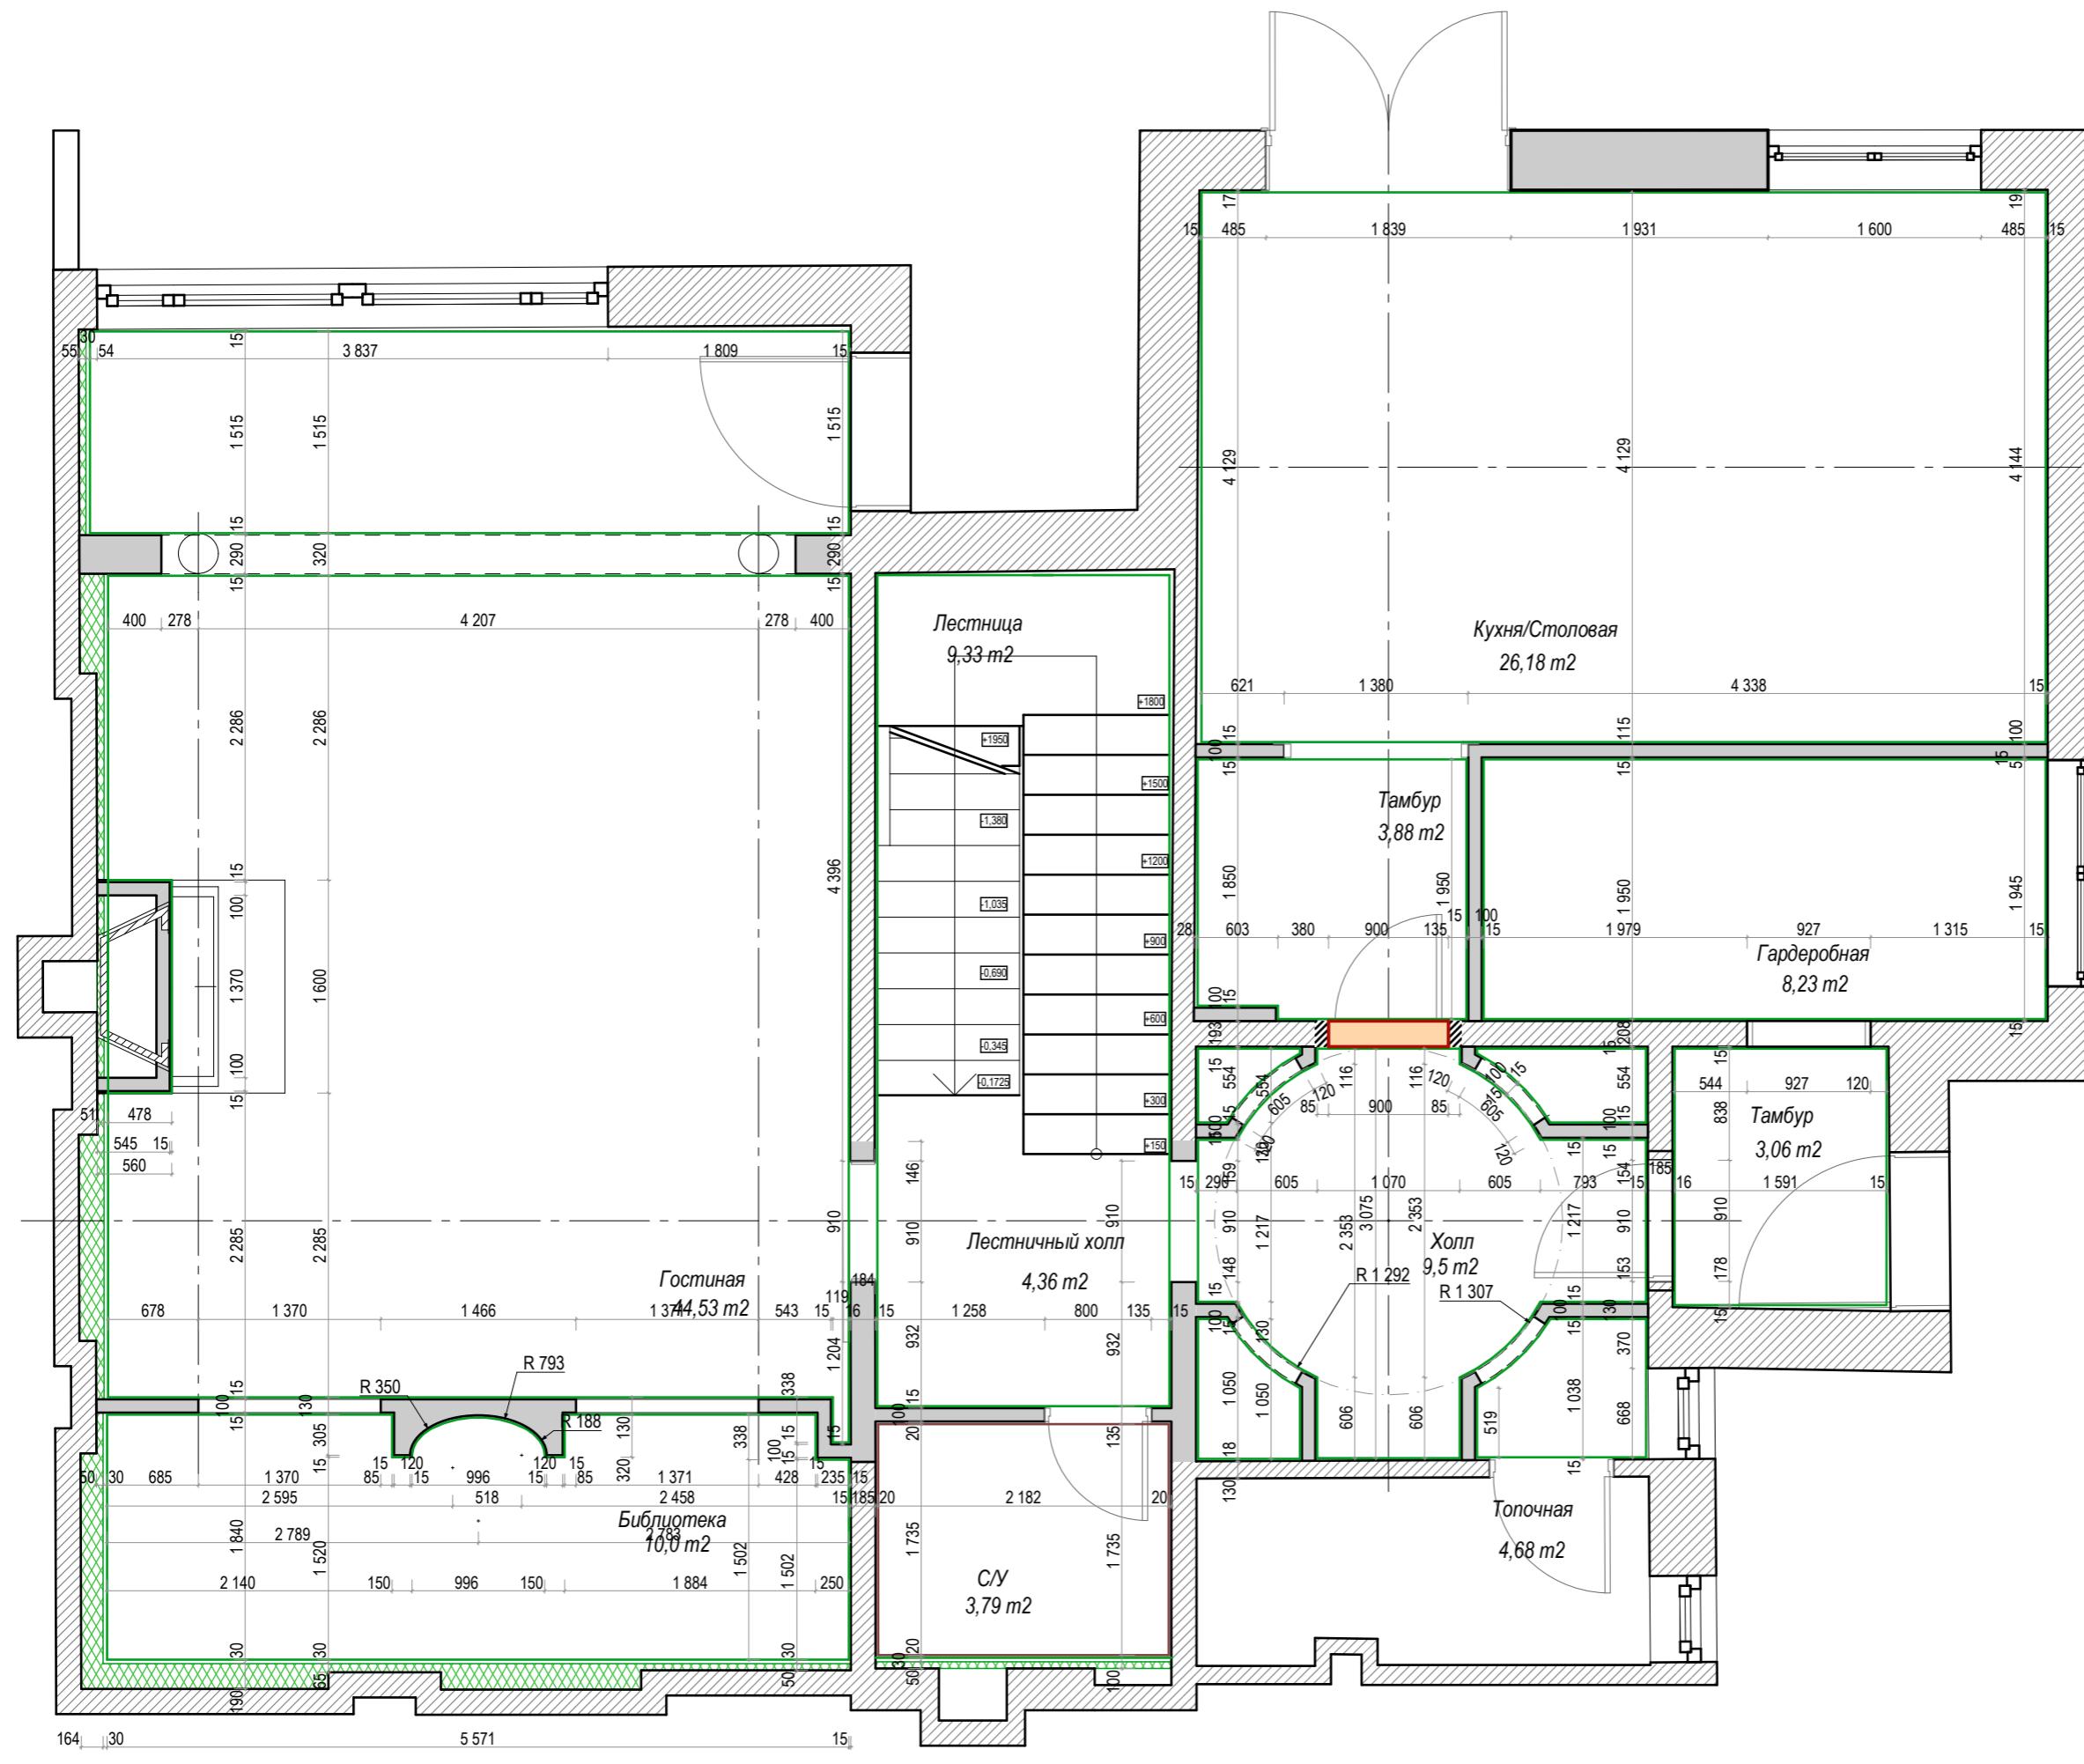


План сносимых и возводимых стен 1го этажа.

Масштаб	Лист	Листов
1:50	12	46

Условные обозначения:

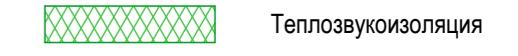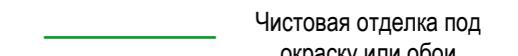-  Проёмы прорубаемые
-  Стены вновь возводимые
-  Теплозвукоизоляция
-  Чистовая отделка плиткой
-  Чистовая отделка под окраску или обои

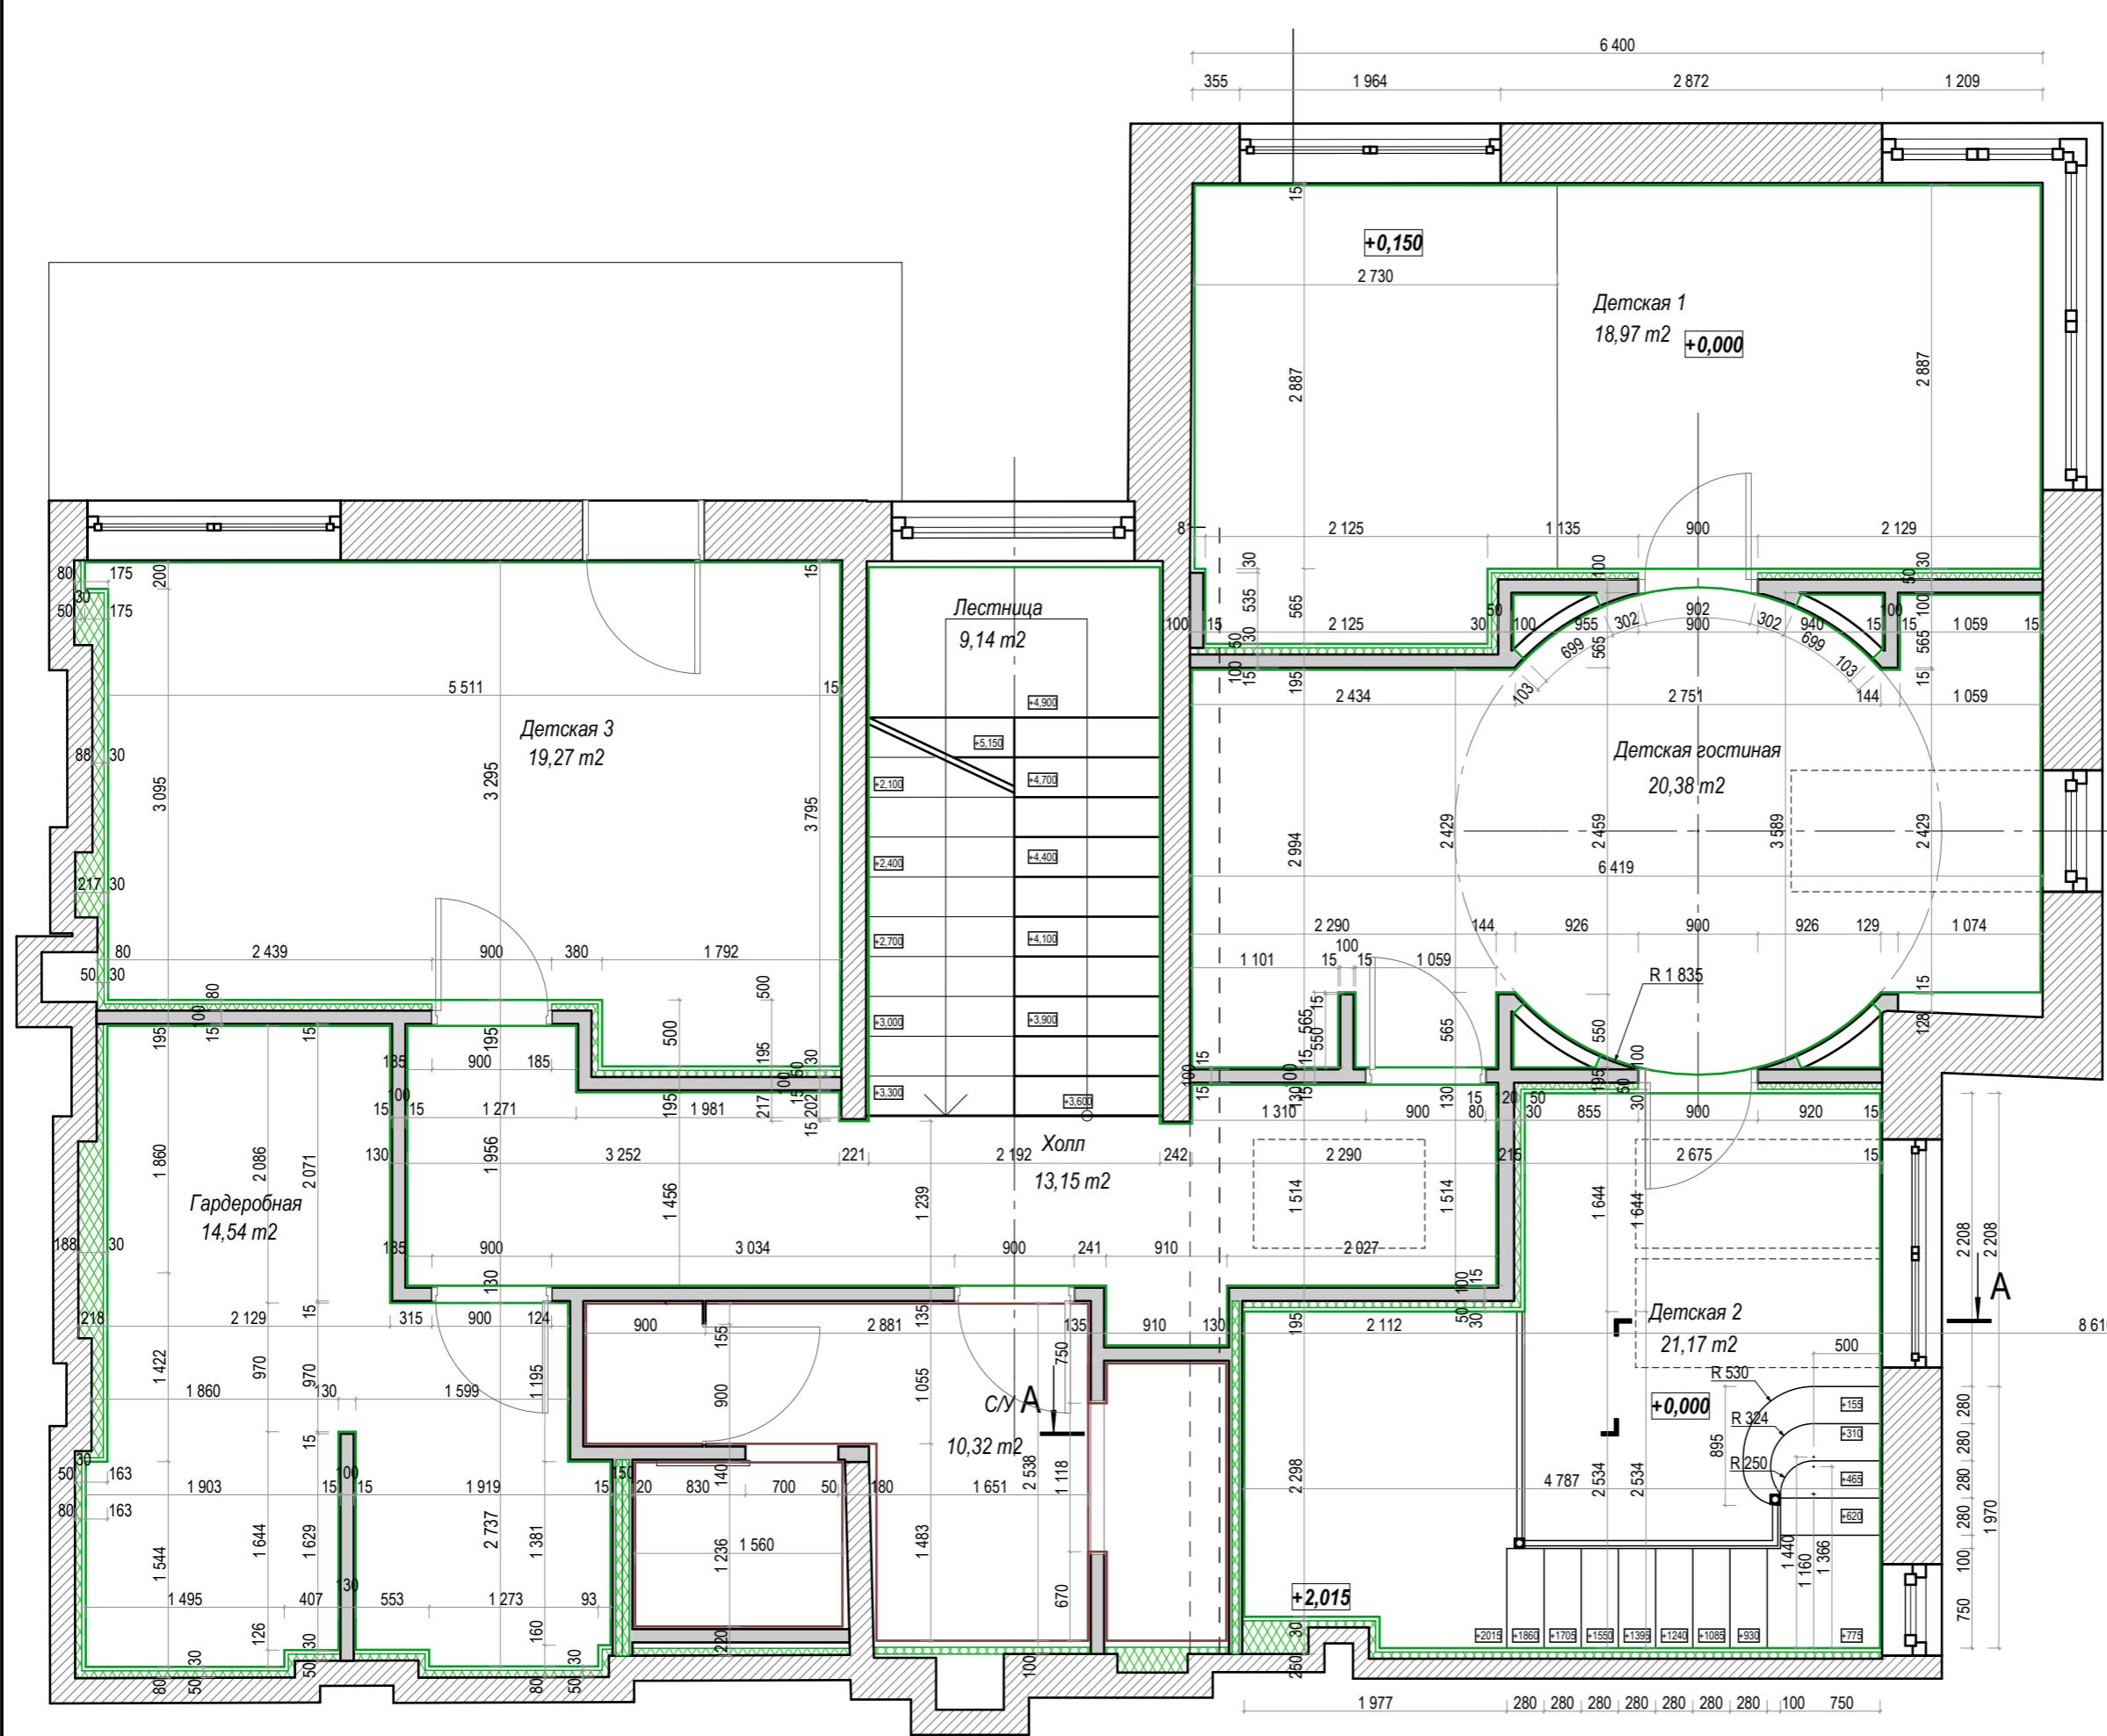


План сносимых и возводимых стен 2го этажа.

Масштаб	Лист	Листов
1:50	13	46


Условные обозначения:

	Проёмы прорубаемые
	Стены вновь возводимые
	Теплозвукоизоляция
	Чистовая отделка плиткой
	Чистовая отделка под окраску или обои

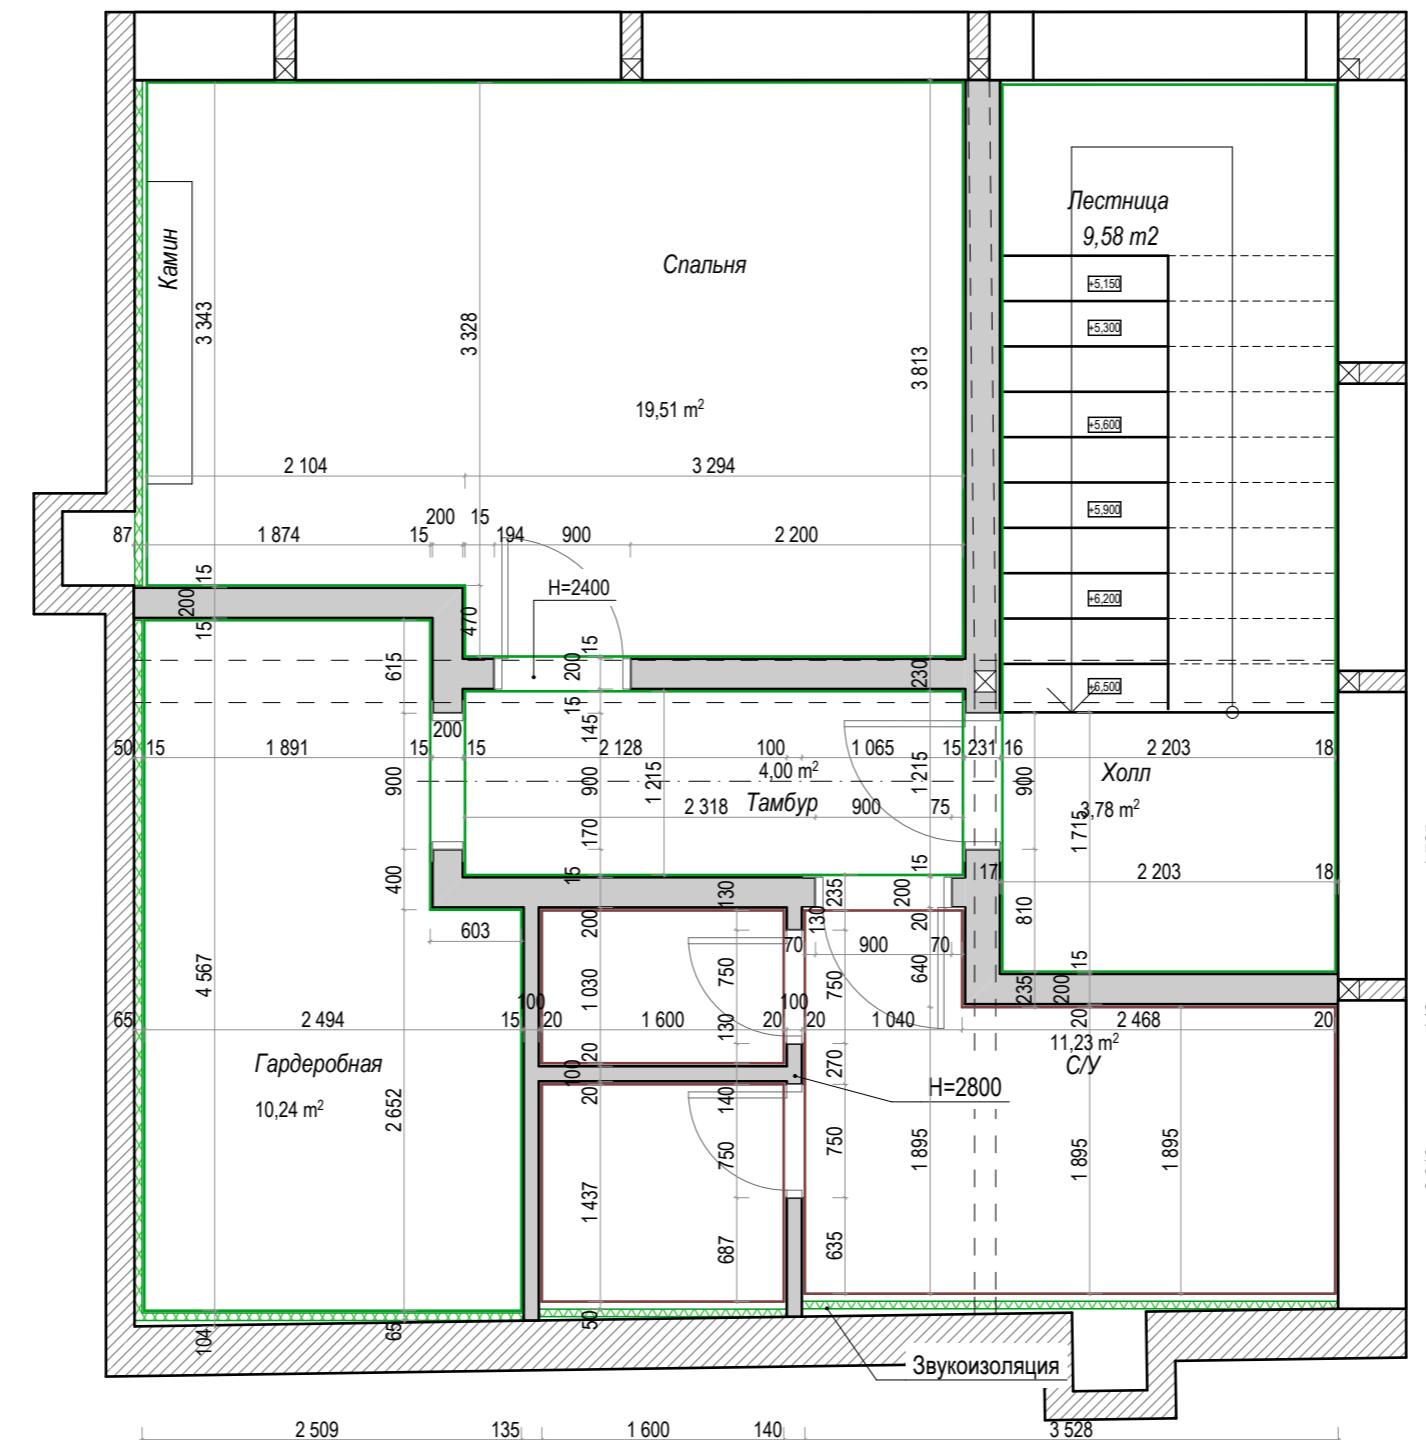

План сносимых и возводимых стен мансардного этажа.

Масштаб	Лист	Листов
1:50	14	46

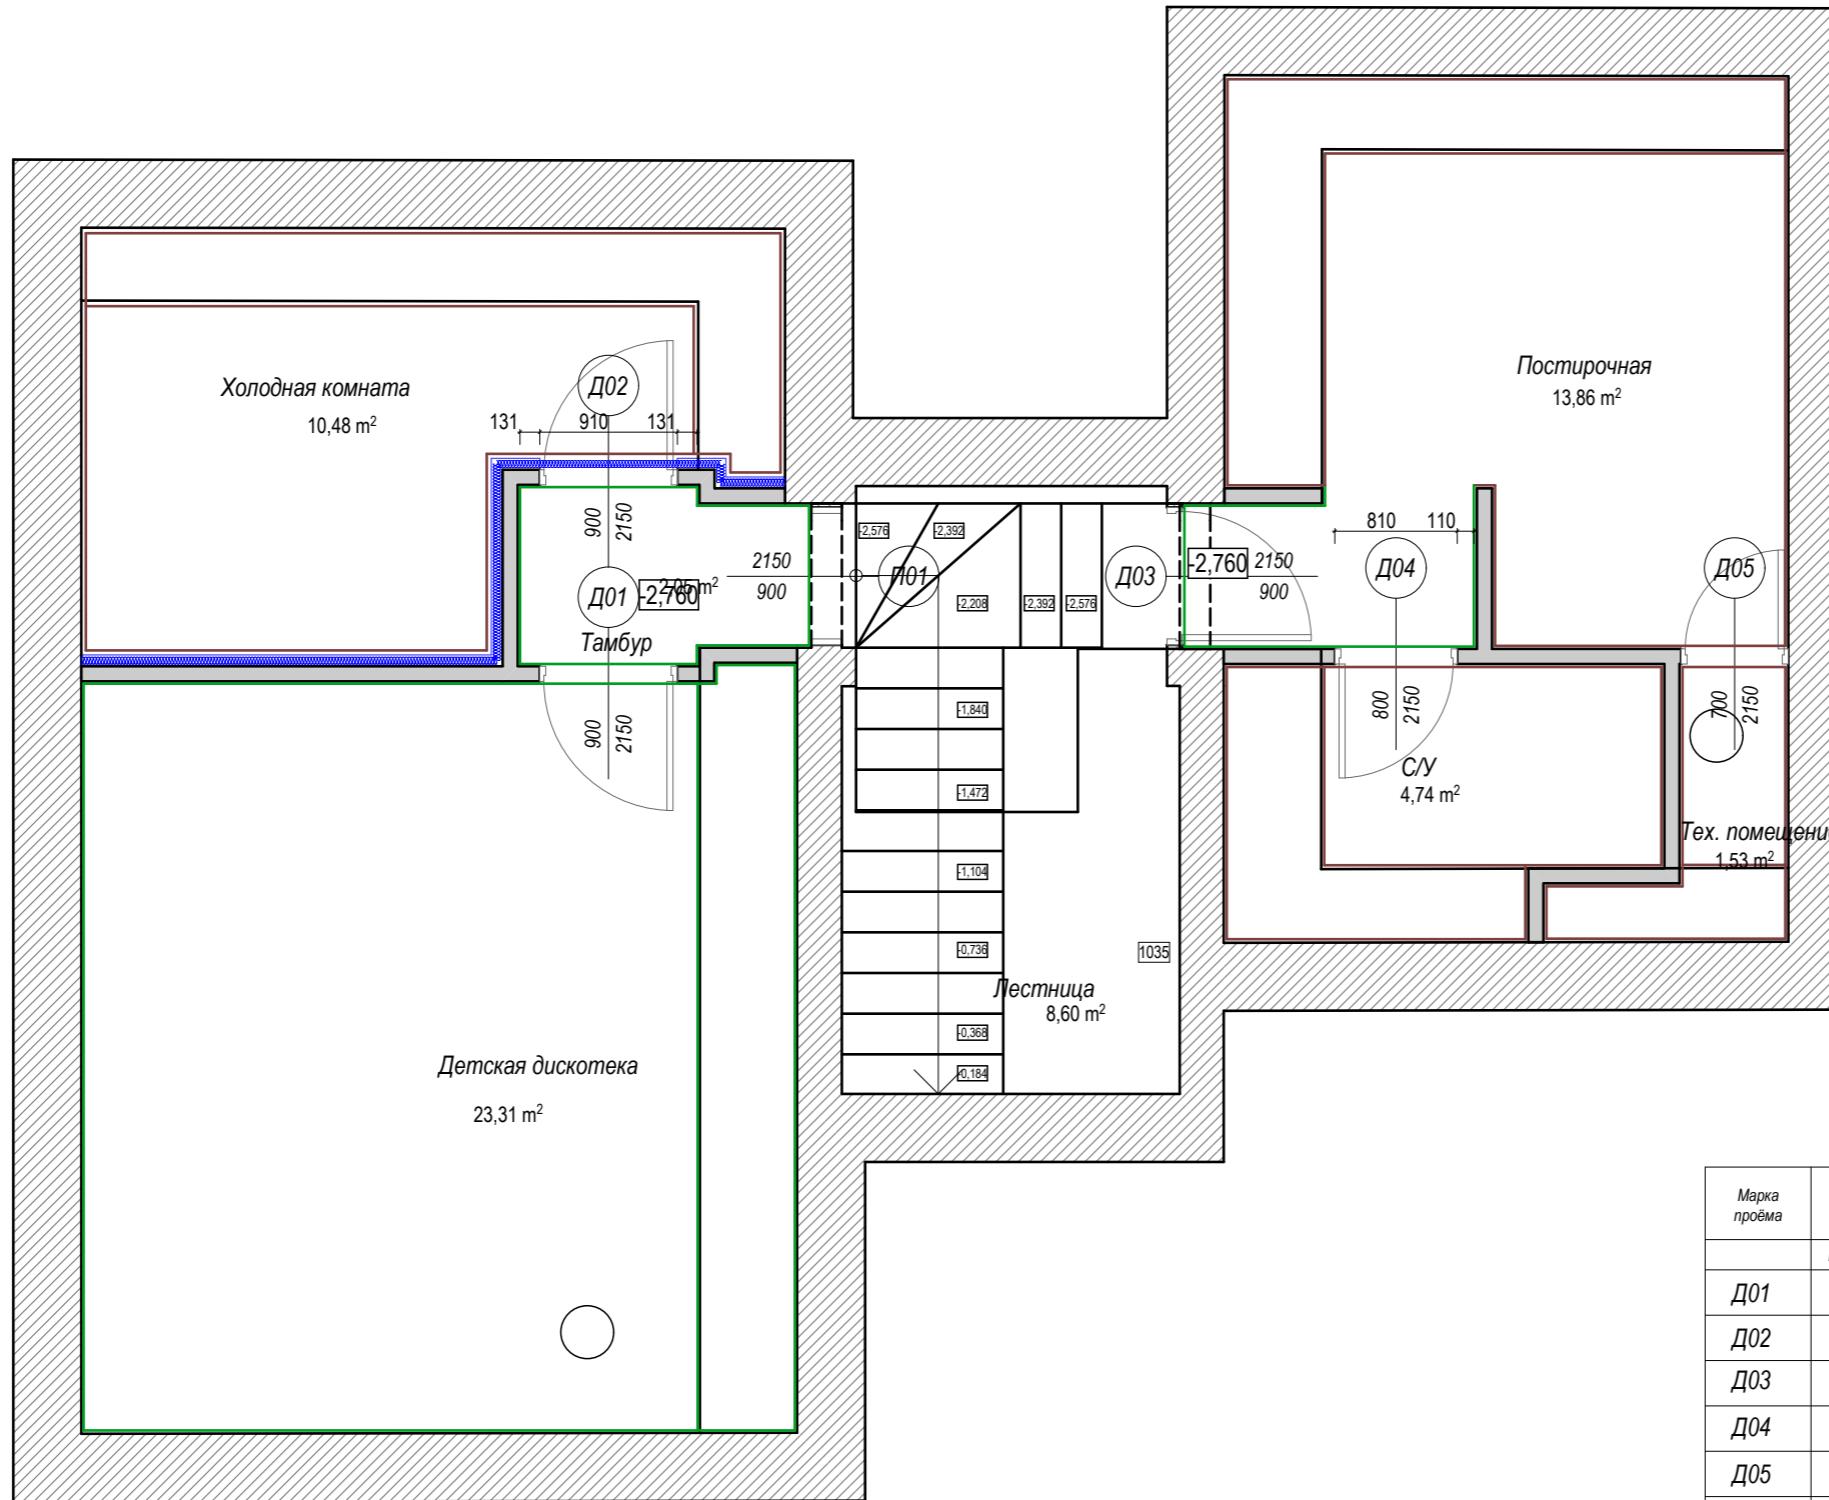



Марка проёма	Размеры проёма мм		Обозначения	Размеры полотна мм	Примечания
	Ширина	Высота			
Д01	910	2150	Дверь индивидуальная откатная	800x2100	
Д02	910	2150	Дверь индивидуальная	800x2100	
Д03	910	2150	Дверь индивидуальная	800x2100	
Д04	810	2150	Дверь индивидуальная	700x2100	
Д05	710	2150	Дверь индивидуальная	600x2100	
П01	910	2150	Дверь индивидуальная		

Высота проёма указана от отм. чистого пола цокольного этажа

Экспликация дверей и проёмов цокольного этажа.


Масштаб	Лист	Листов
1:50	15	46

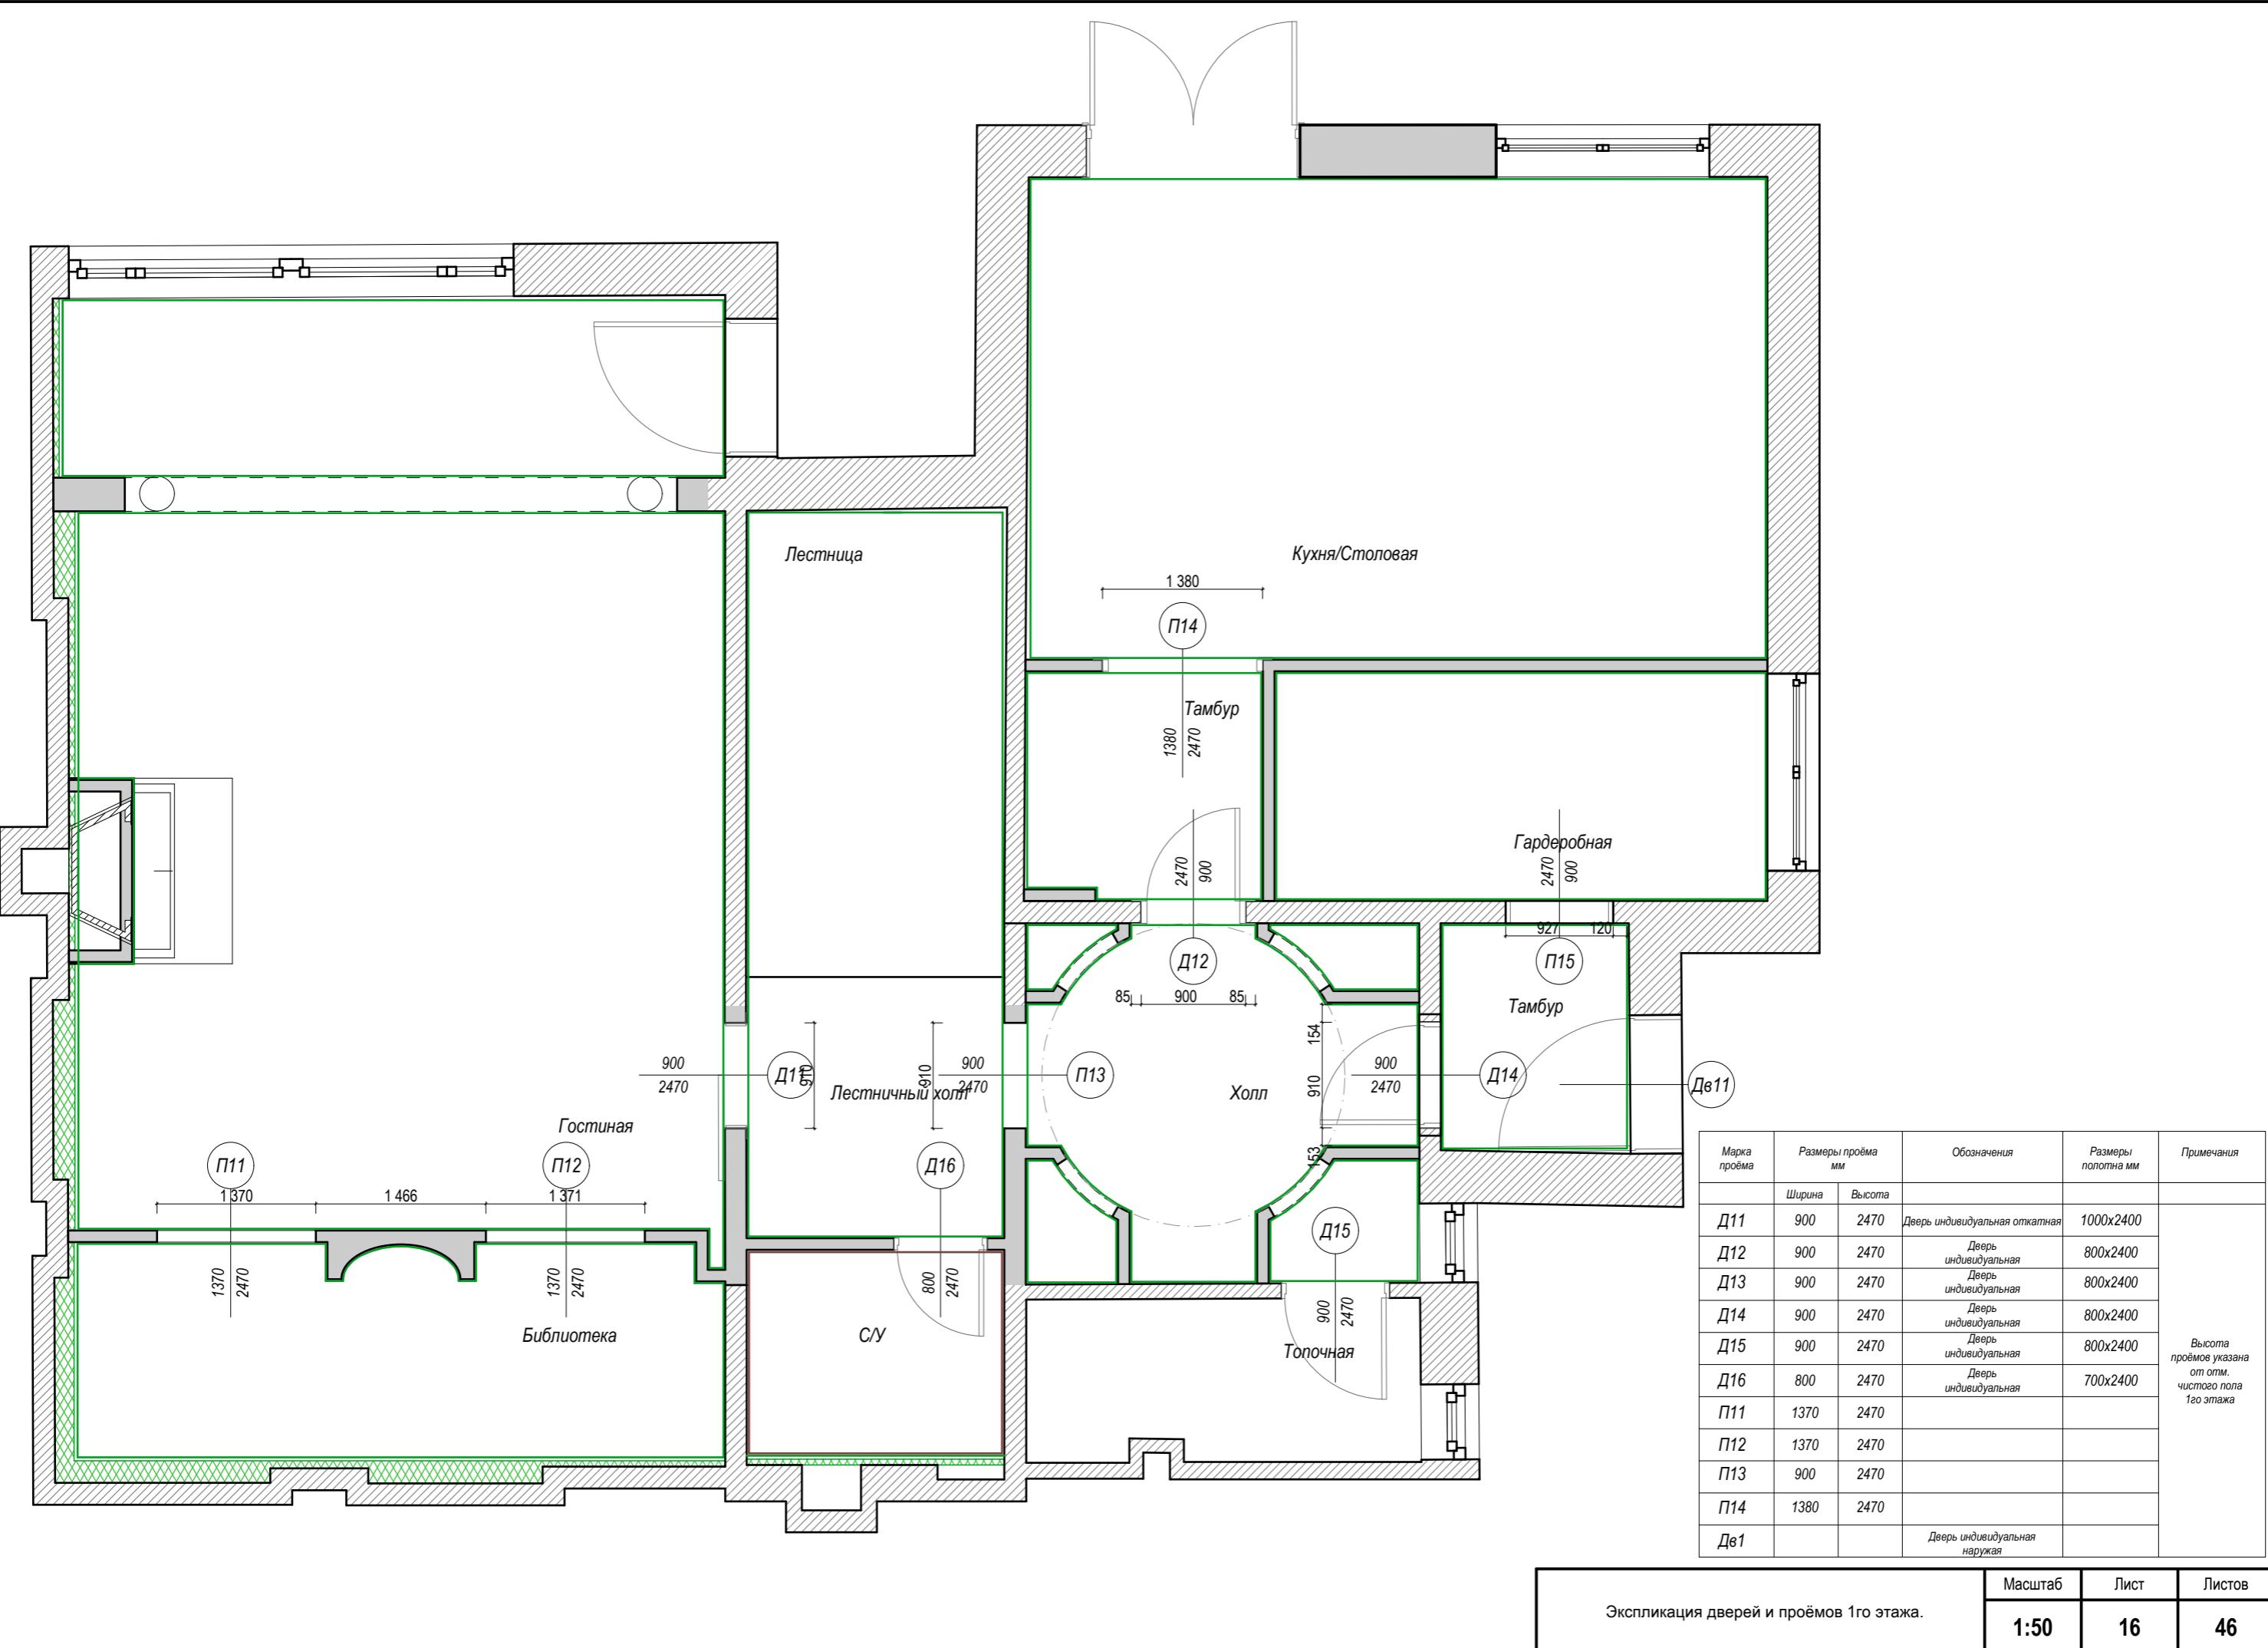

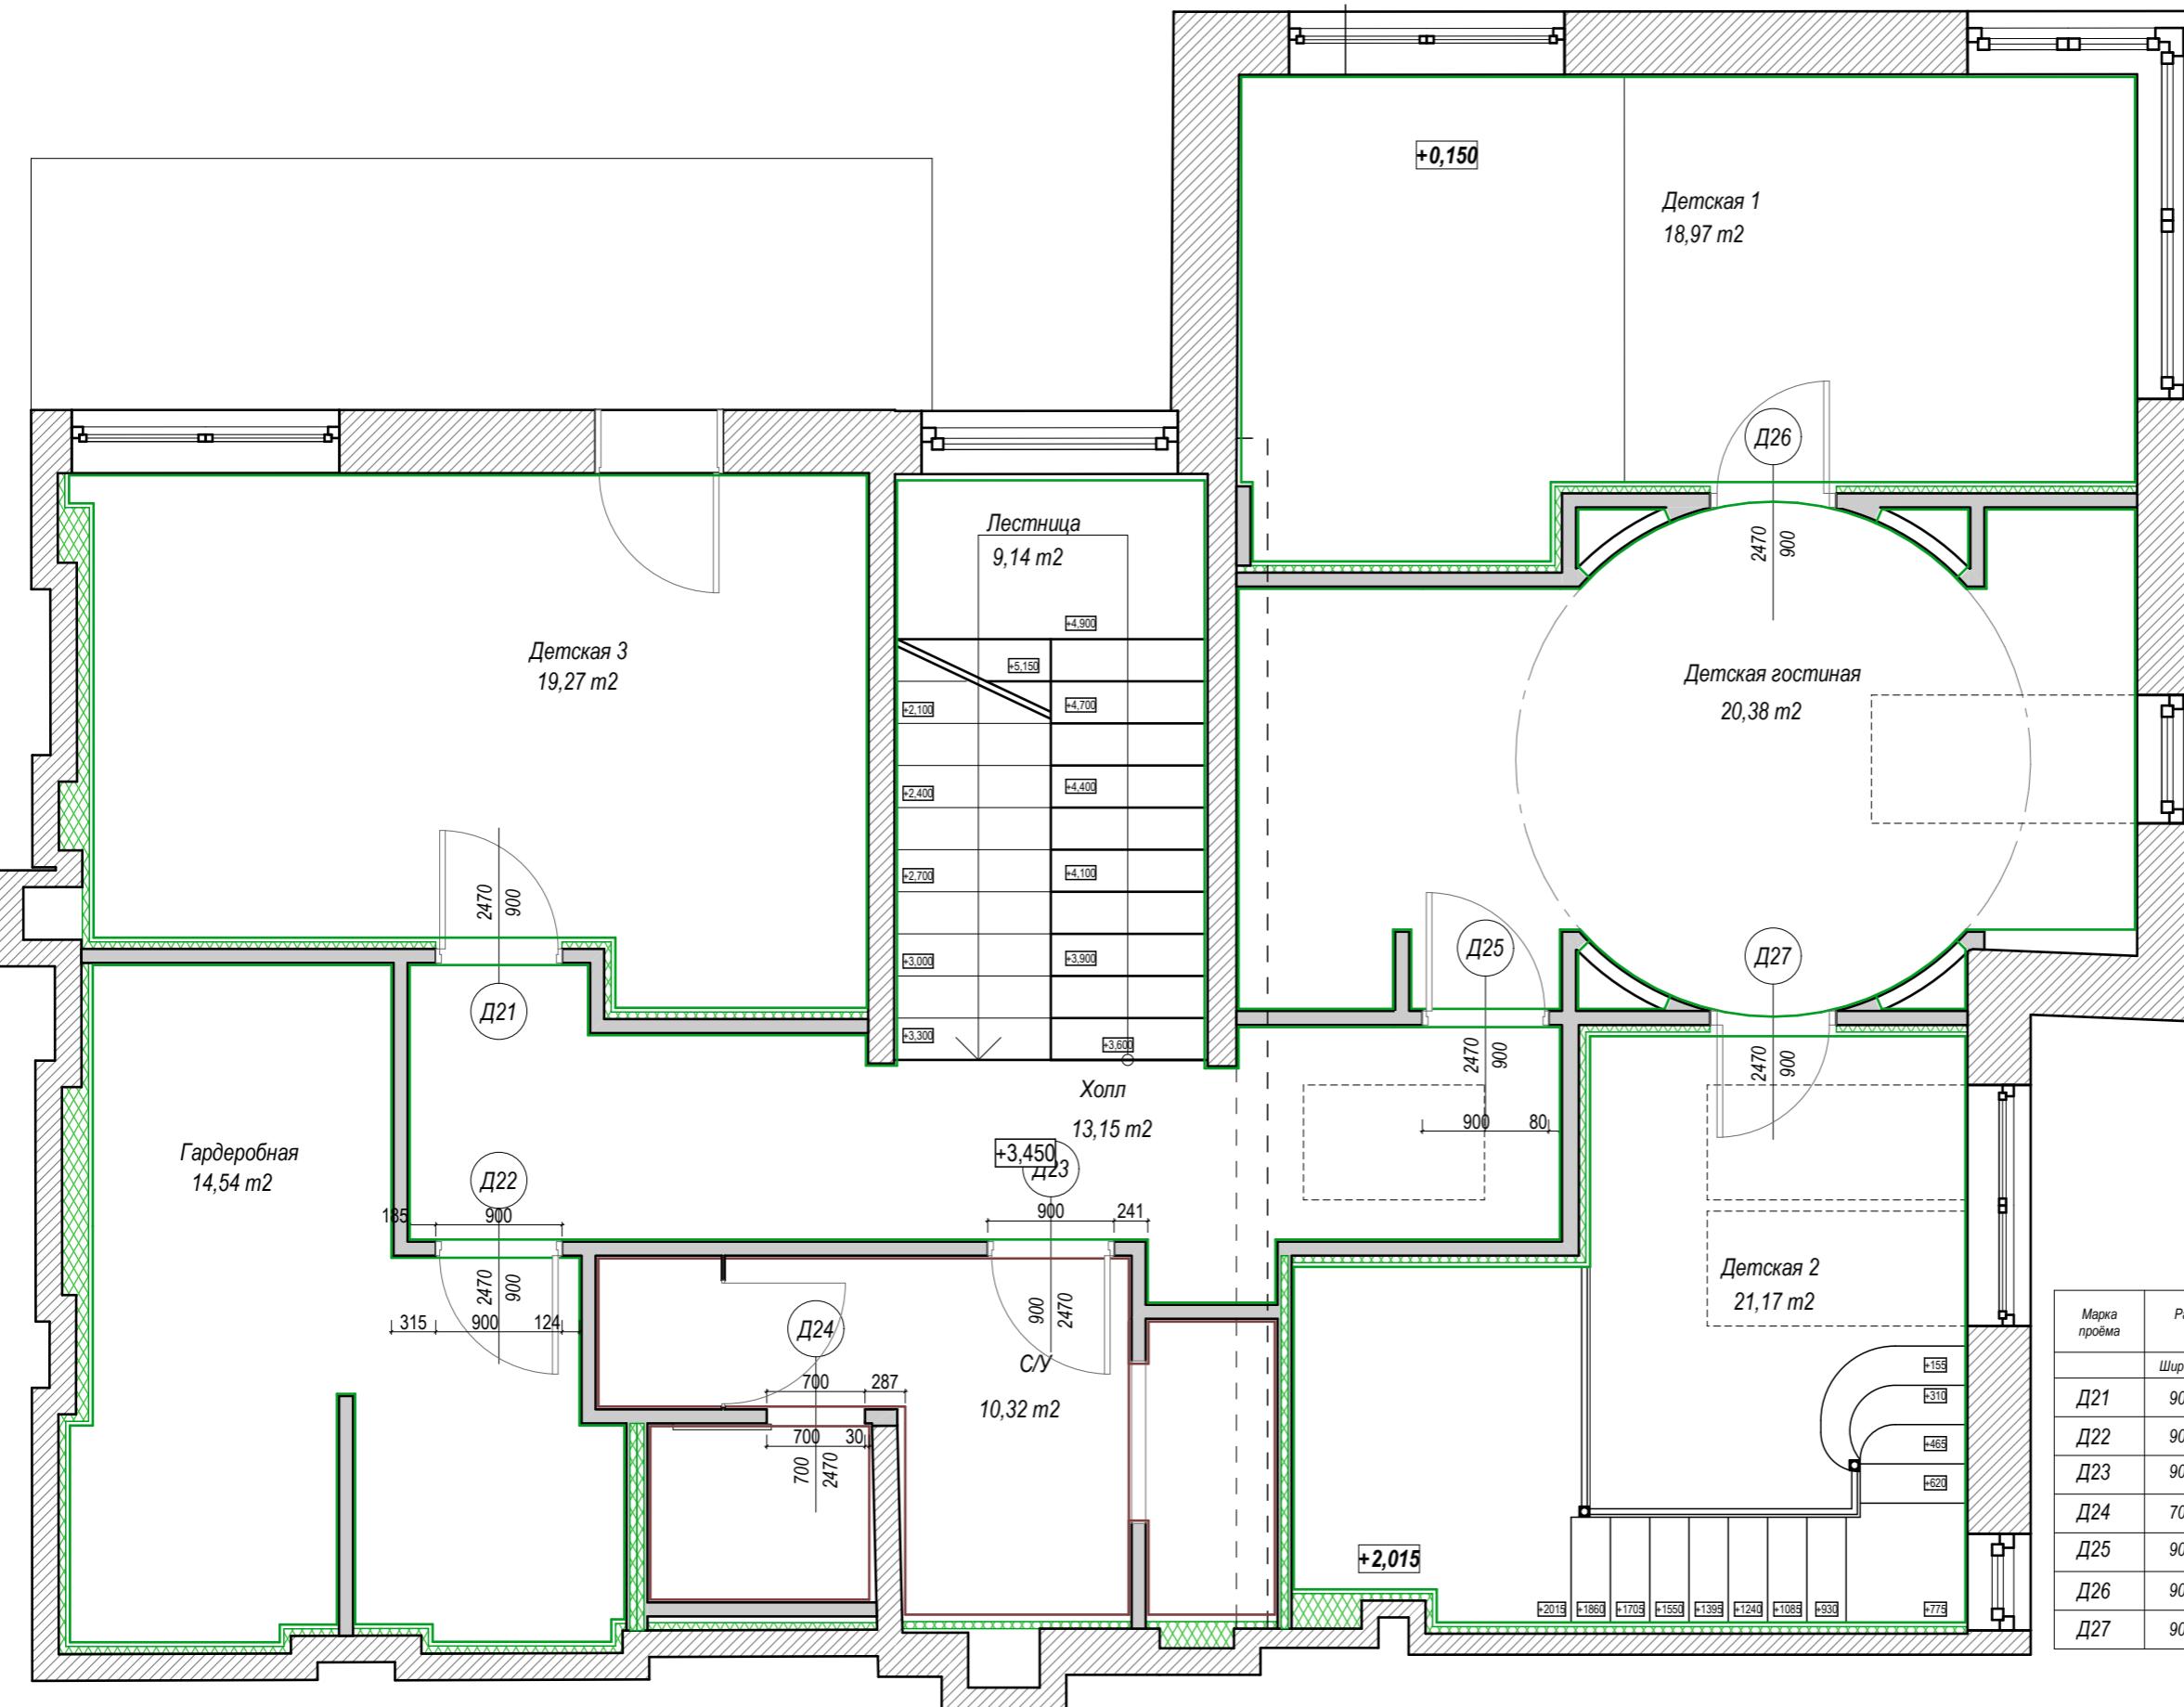

Марка проёма	Размеры проёма мм		Обозначения	Размеры полотна мм	Примечания
	Ширина	Высота			
Д21	900	2470	Дверь индивидуальная	800x2400	Высота проёмов указана от отм. чистого пола 2го этажа
Д22	900	2470	Дверь индивидуальная	800x2400	
Д23	900	2470	Дверь индивидуальная	800x2400	
Д24	700	2470	Дверь индивидуальная откатная	800x2400	
Д25	900	2470	Дверь индивидуальная	800x2400	
Д26	900	2470	Дверь индивидуальная	800x2400	
Д27	900	2470			

Высота
проёмов указа-
ет от отм.
чистого пол-
2го этажа

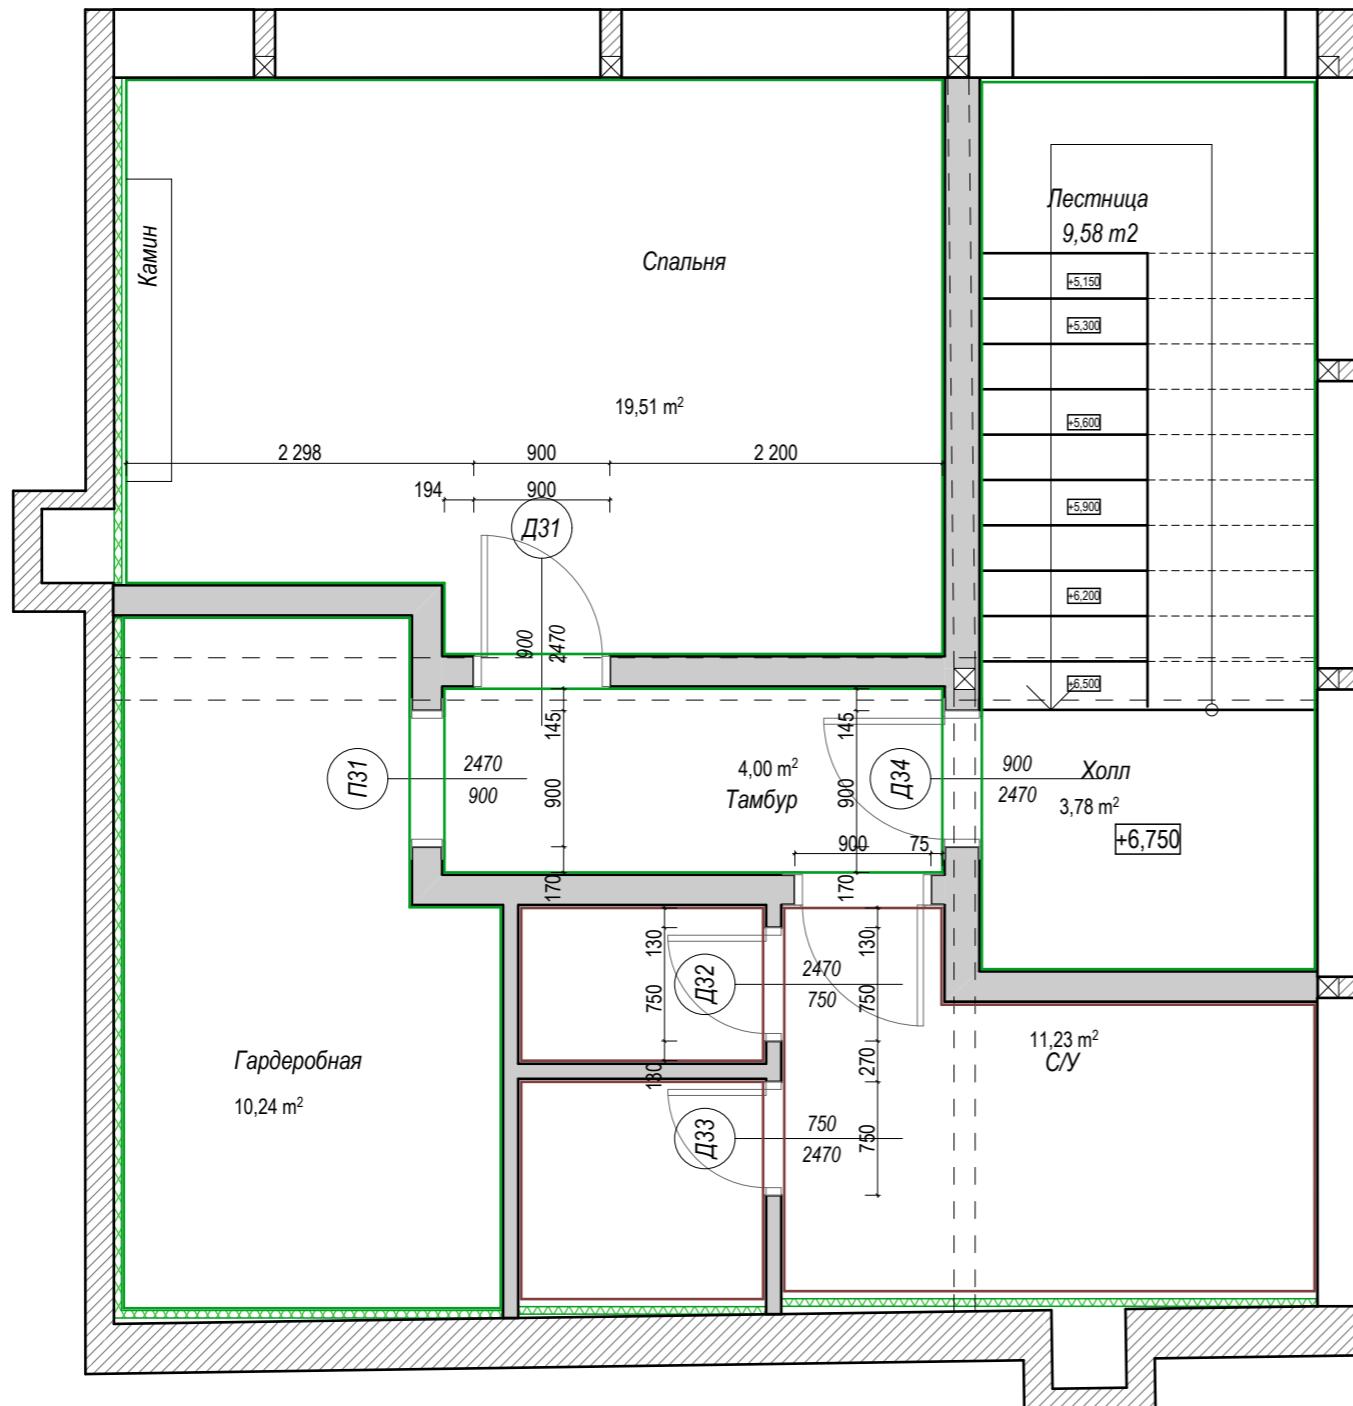

Марка проёма	Размеры проёма мм		Обозначения	Размеры полотна мм	Примечания
	Ширина	Высота			
Д31	900	2470	Дверь индивидуальная откатная	1000x2400	Высота проёмов указана от отм. чистого пола мансардного этажа
Д32	750	2470	Дверь индивидуальная	700x2400	
Д33	750	2470	Дверь индивидуальная	700x2400	
Д34	900	2470	Дверь индивидуальная	800x2400	
П31	900	2470			

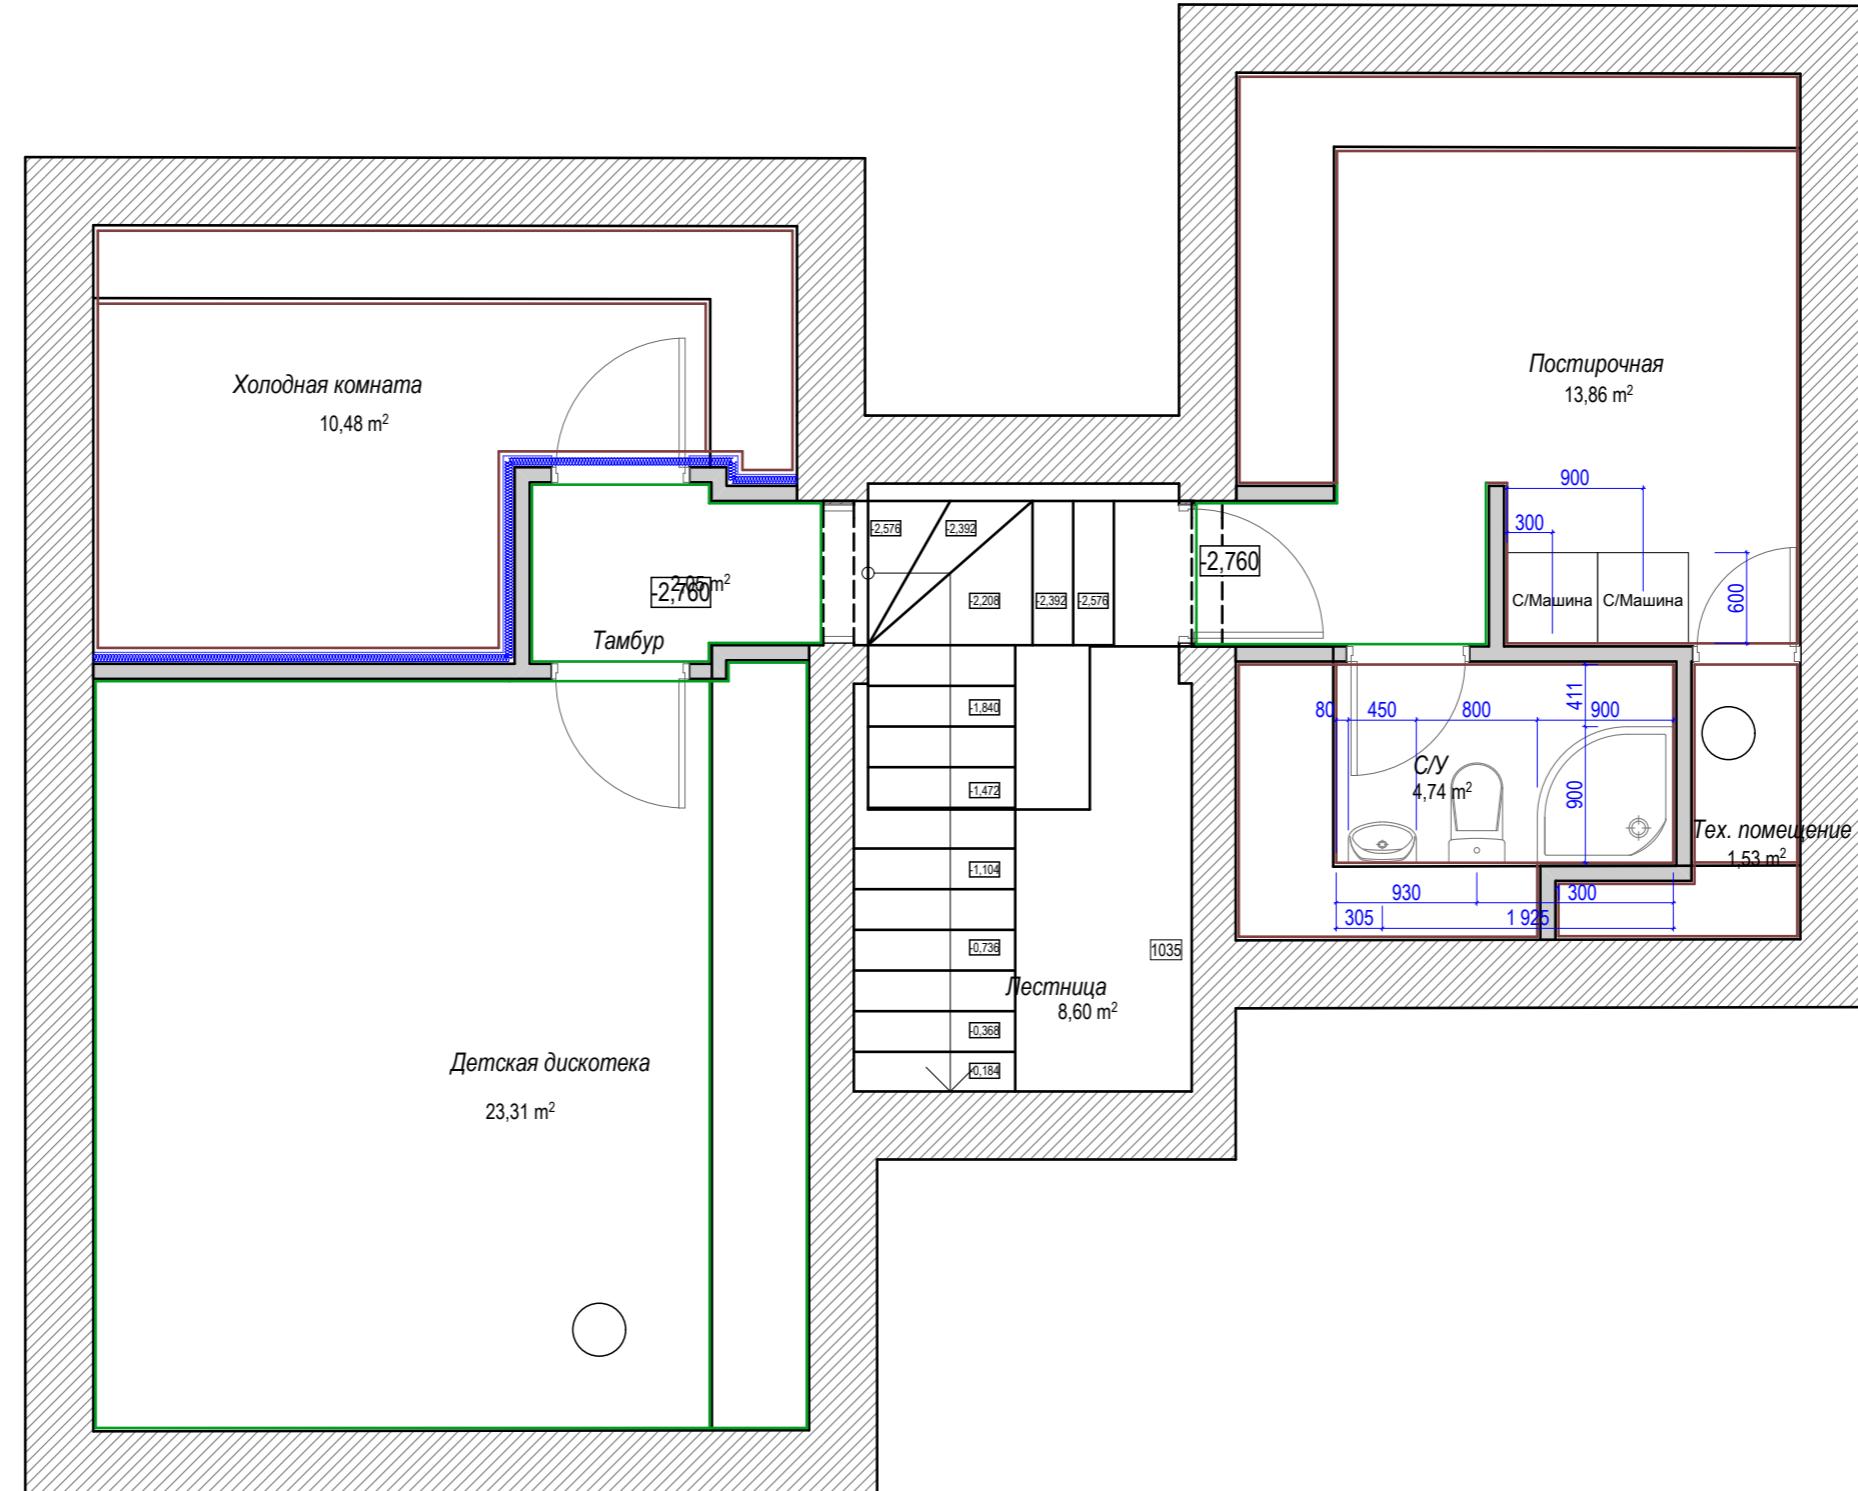


Схема размещения сантехники цокольного этажа.

Схема размещения сантехники цокольного этажа.	Масштаб	Лист	Листов
	1:50	19	46

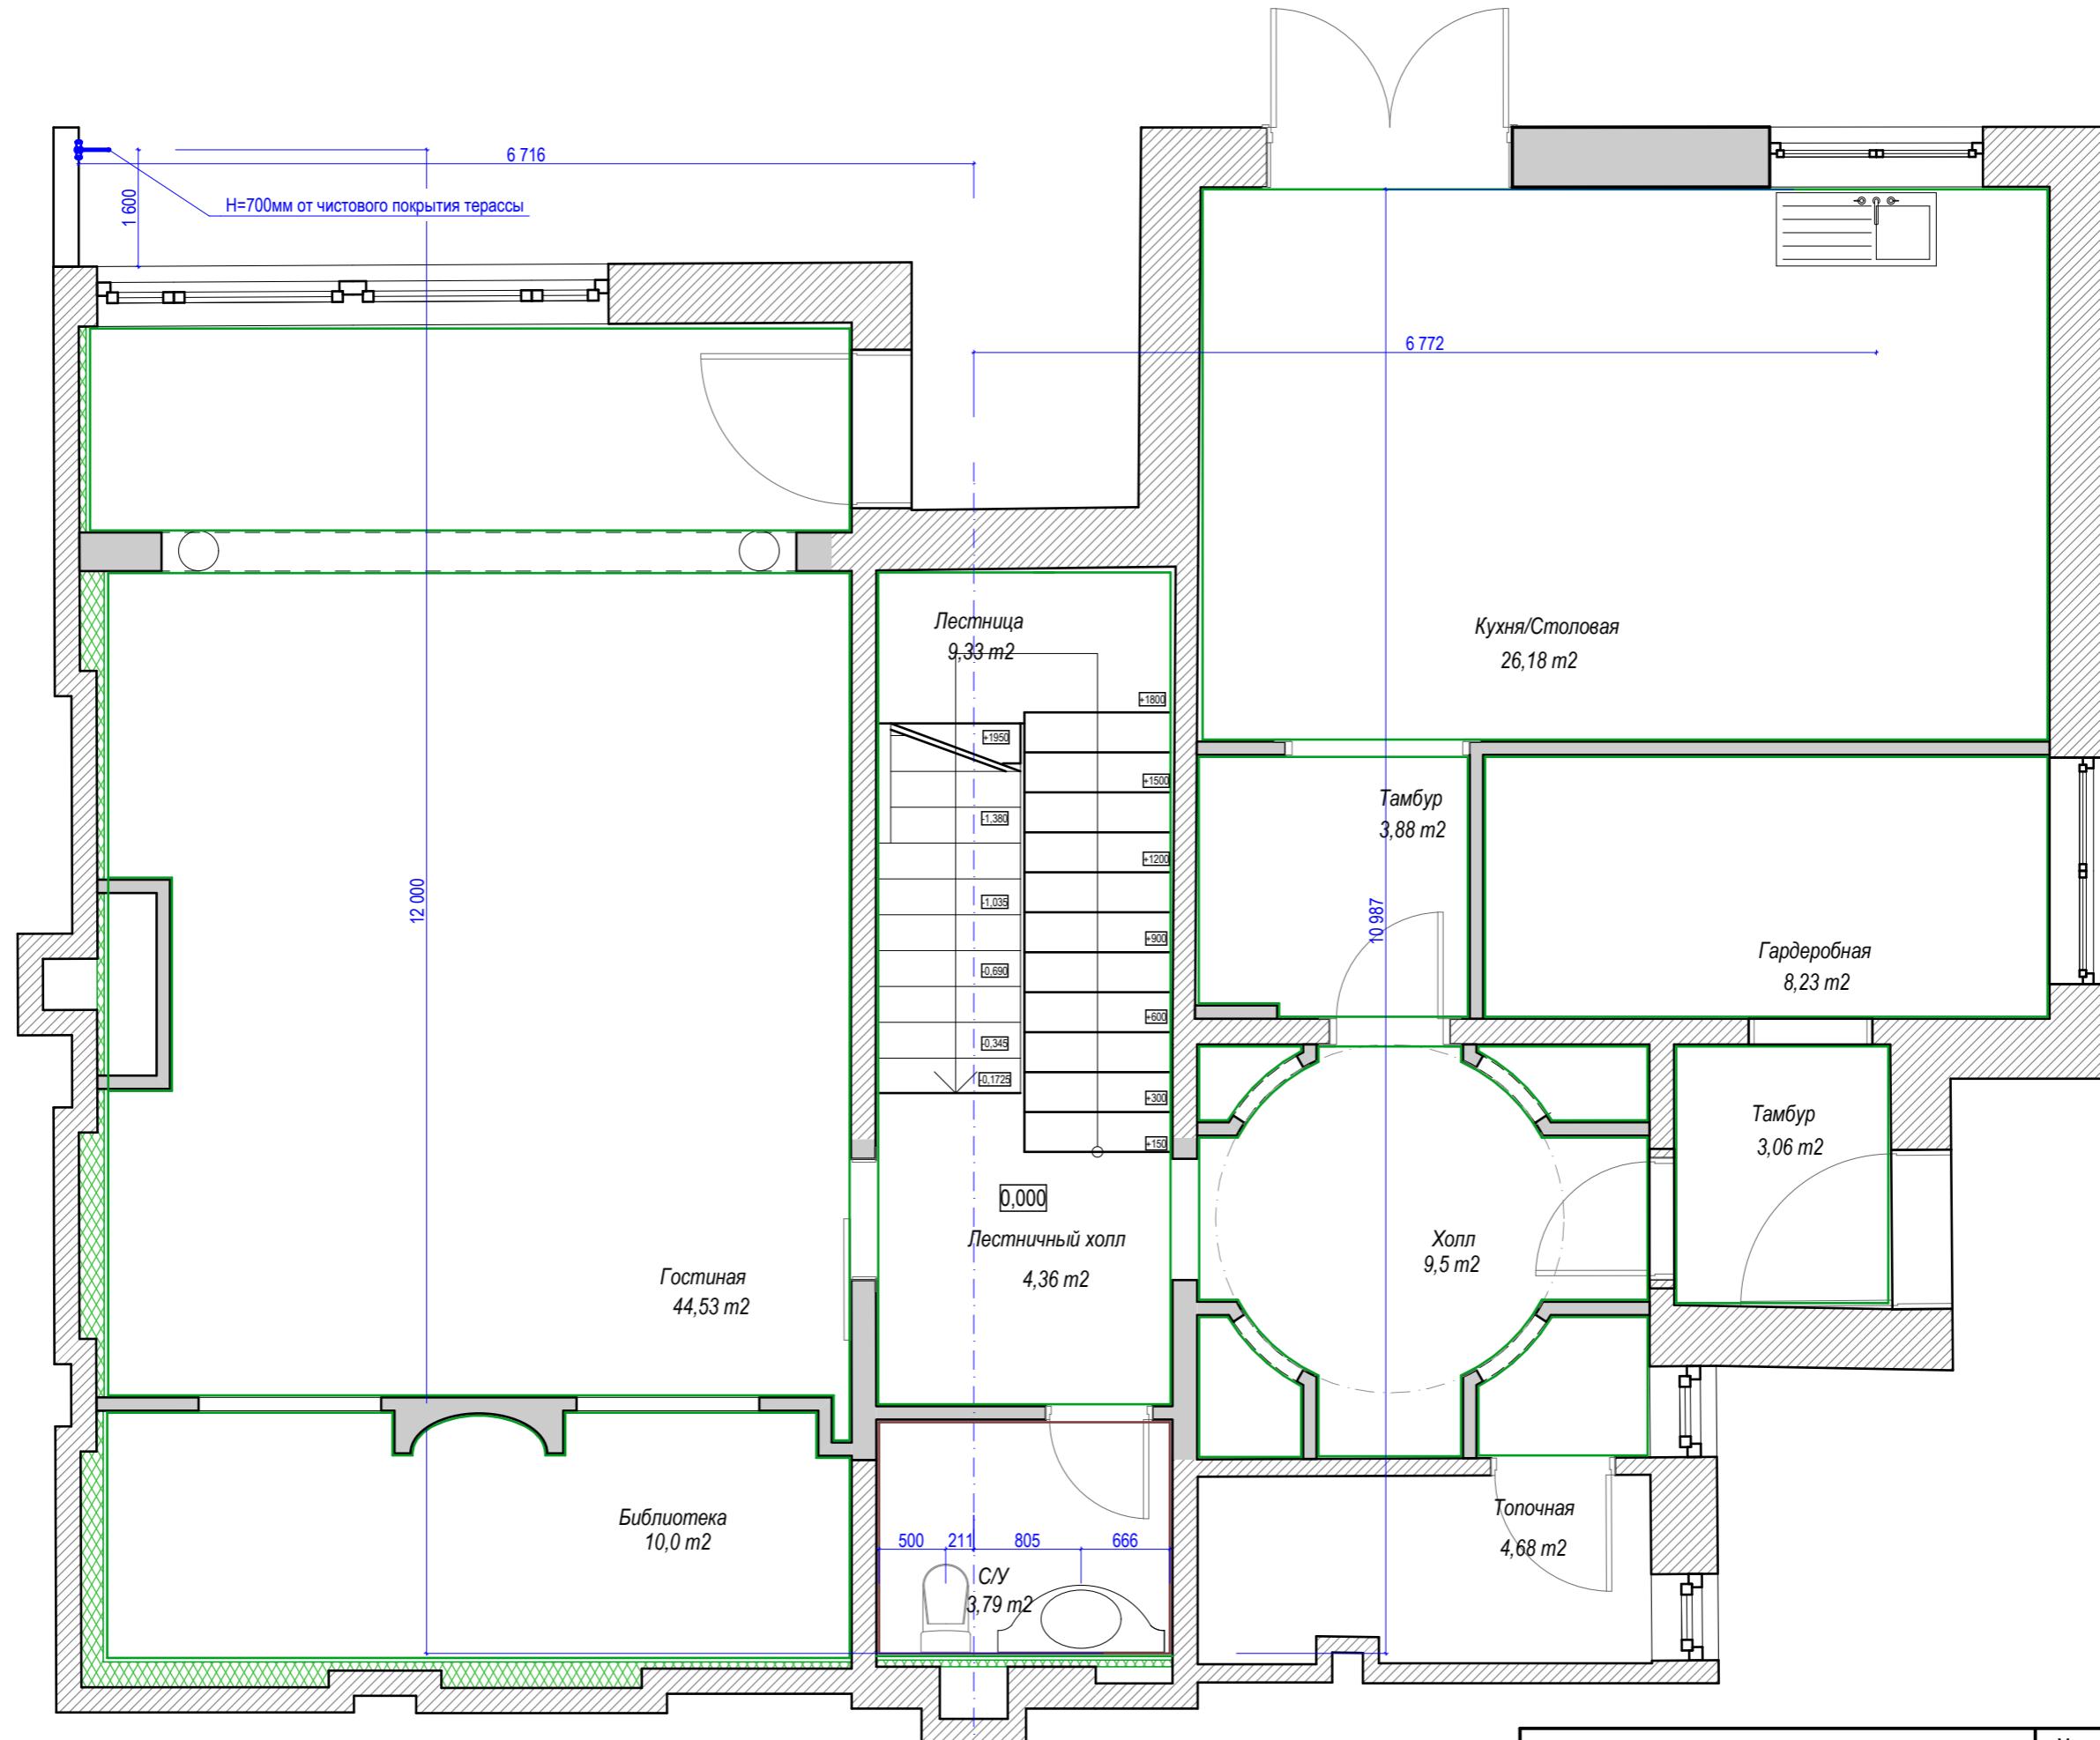


Схема размещения сантехники 1го этажа.

Масштаб	Лист	Листов
1:50	20	46

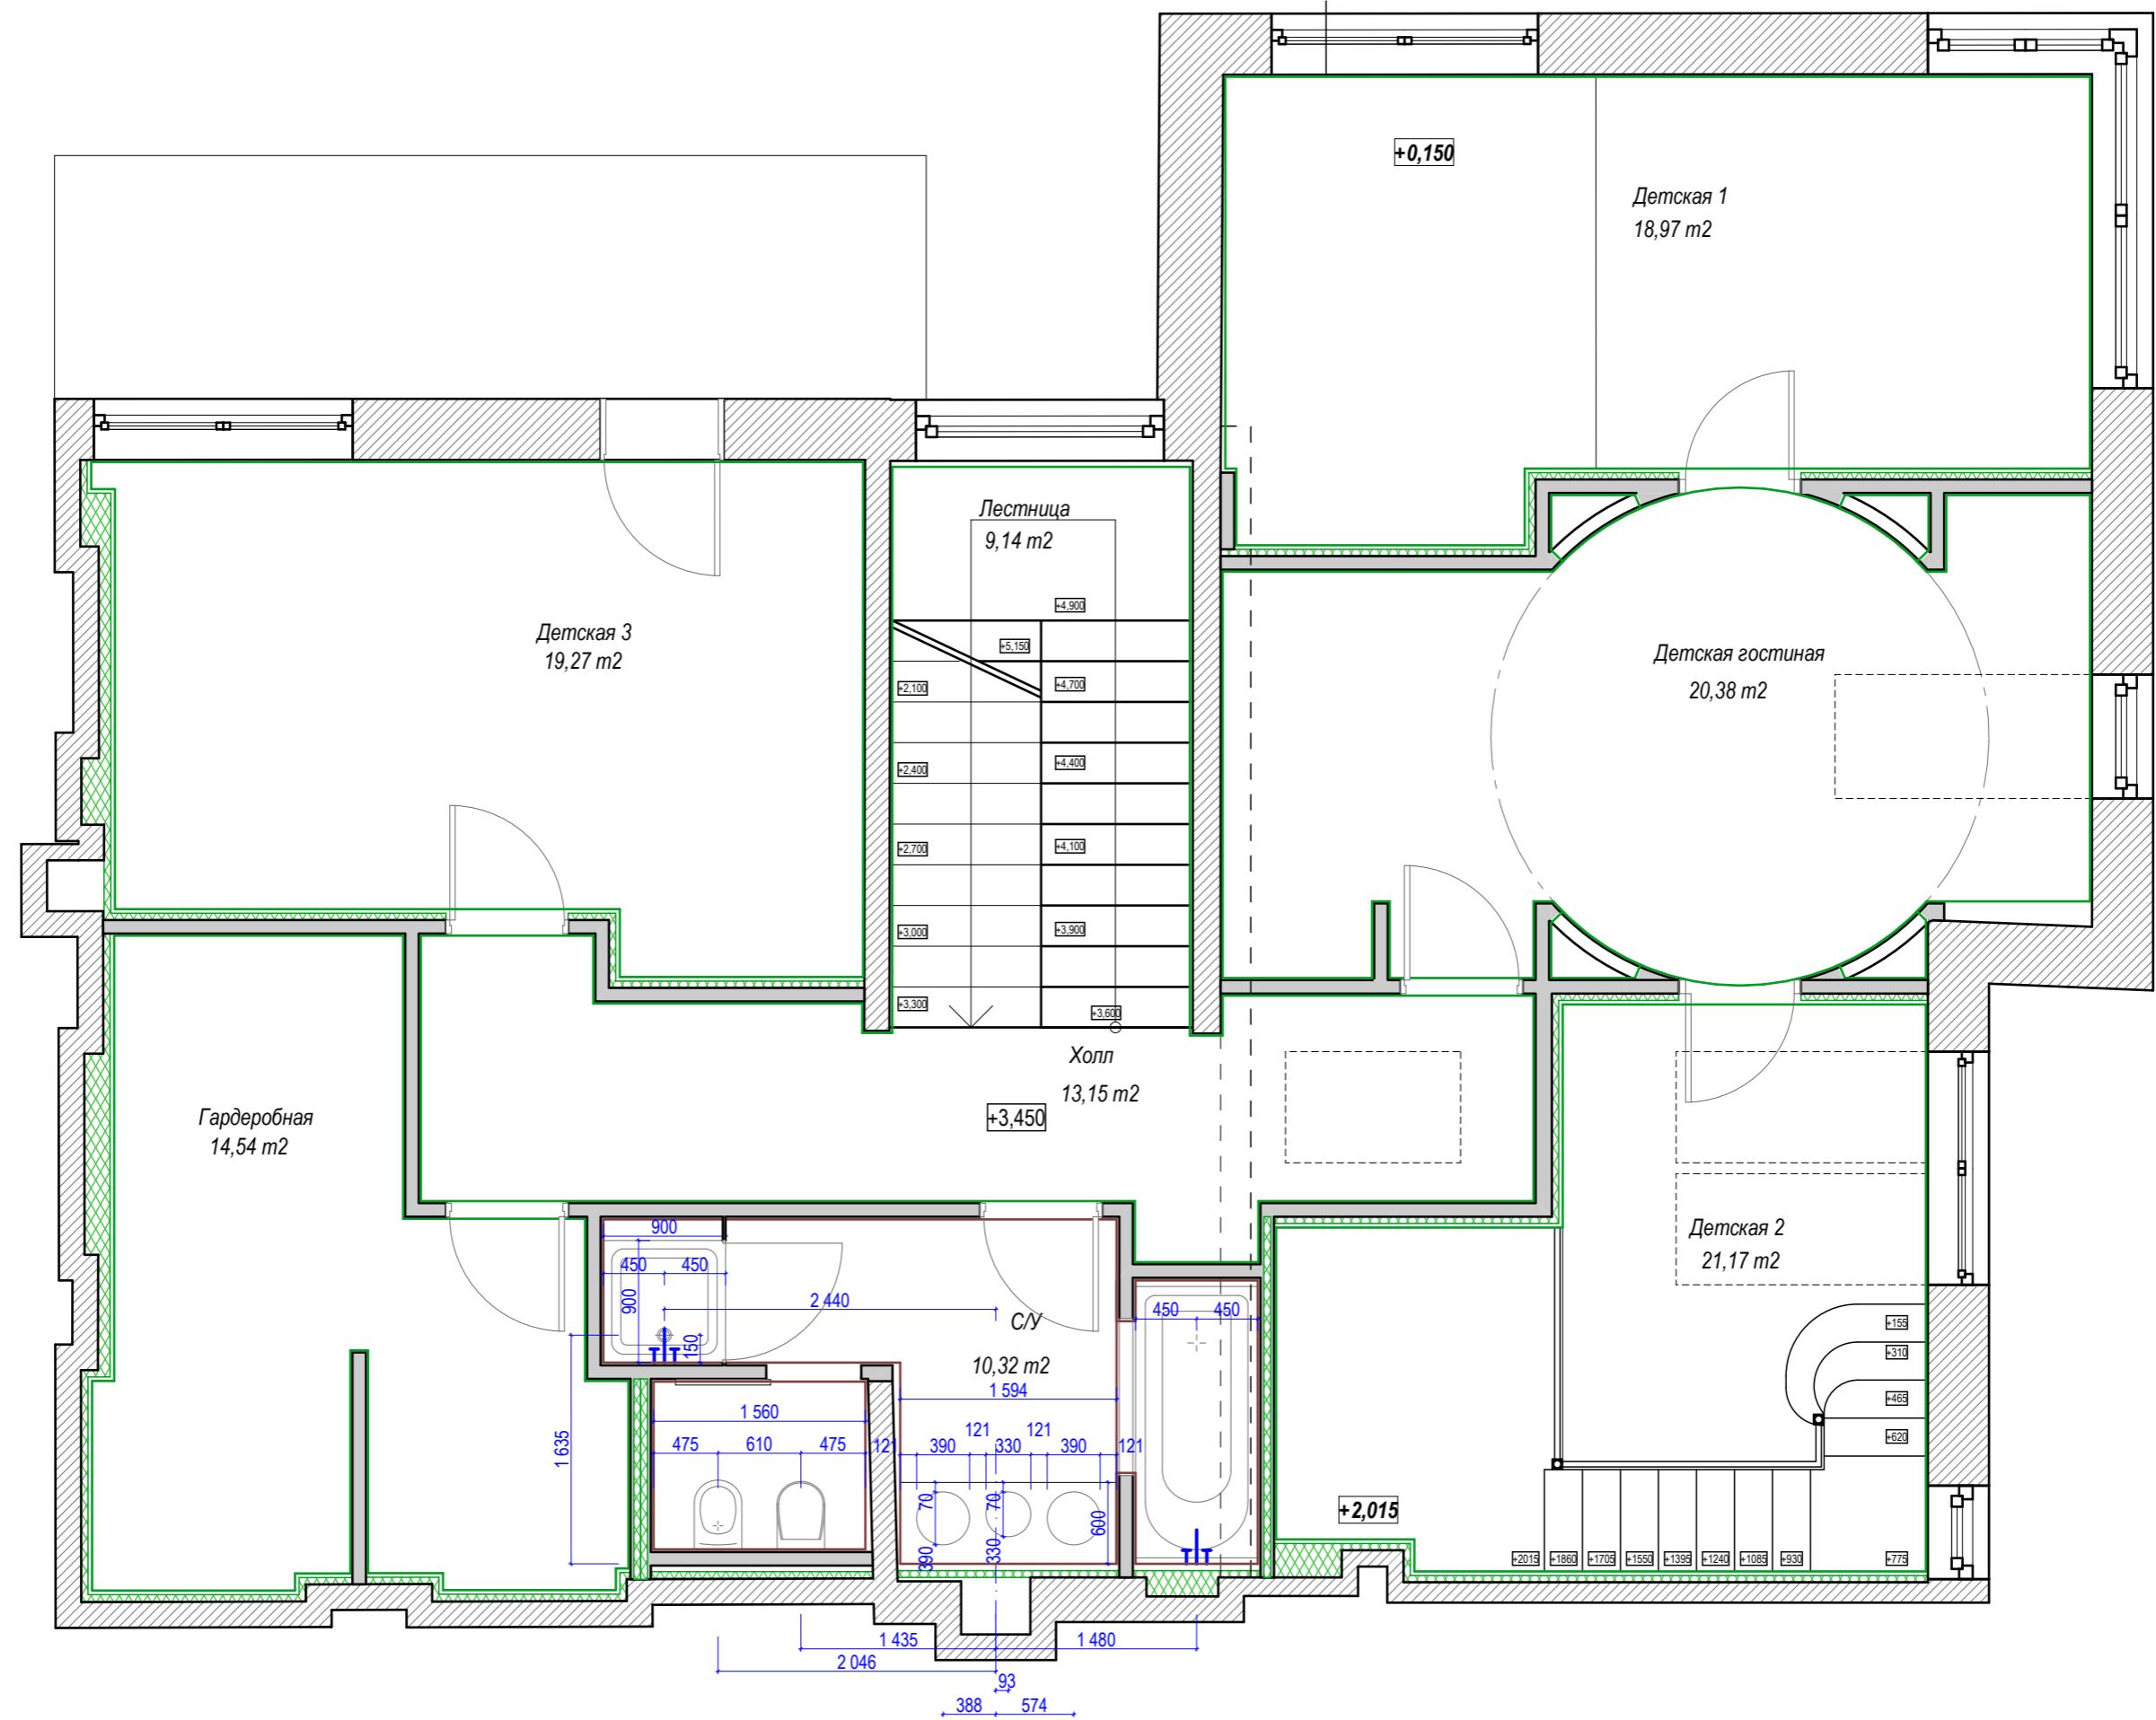


Схема размещения сантехники 2го этажа.

Схема размещения сантехники 2го этажа.	Масштаб	Лист	Листов
	1:50	21	46


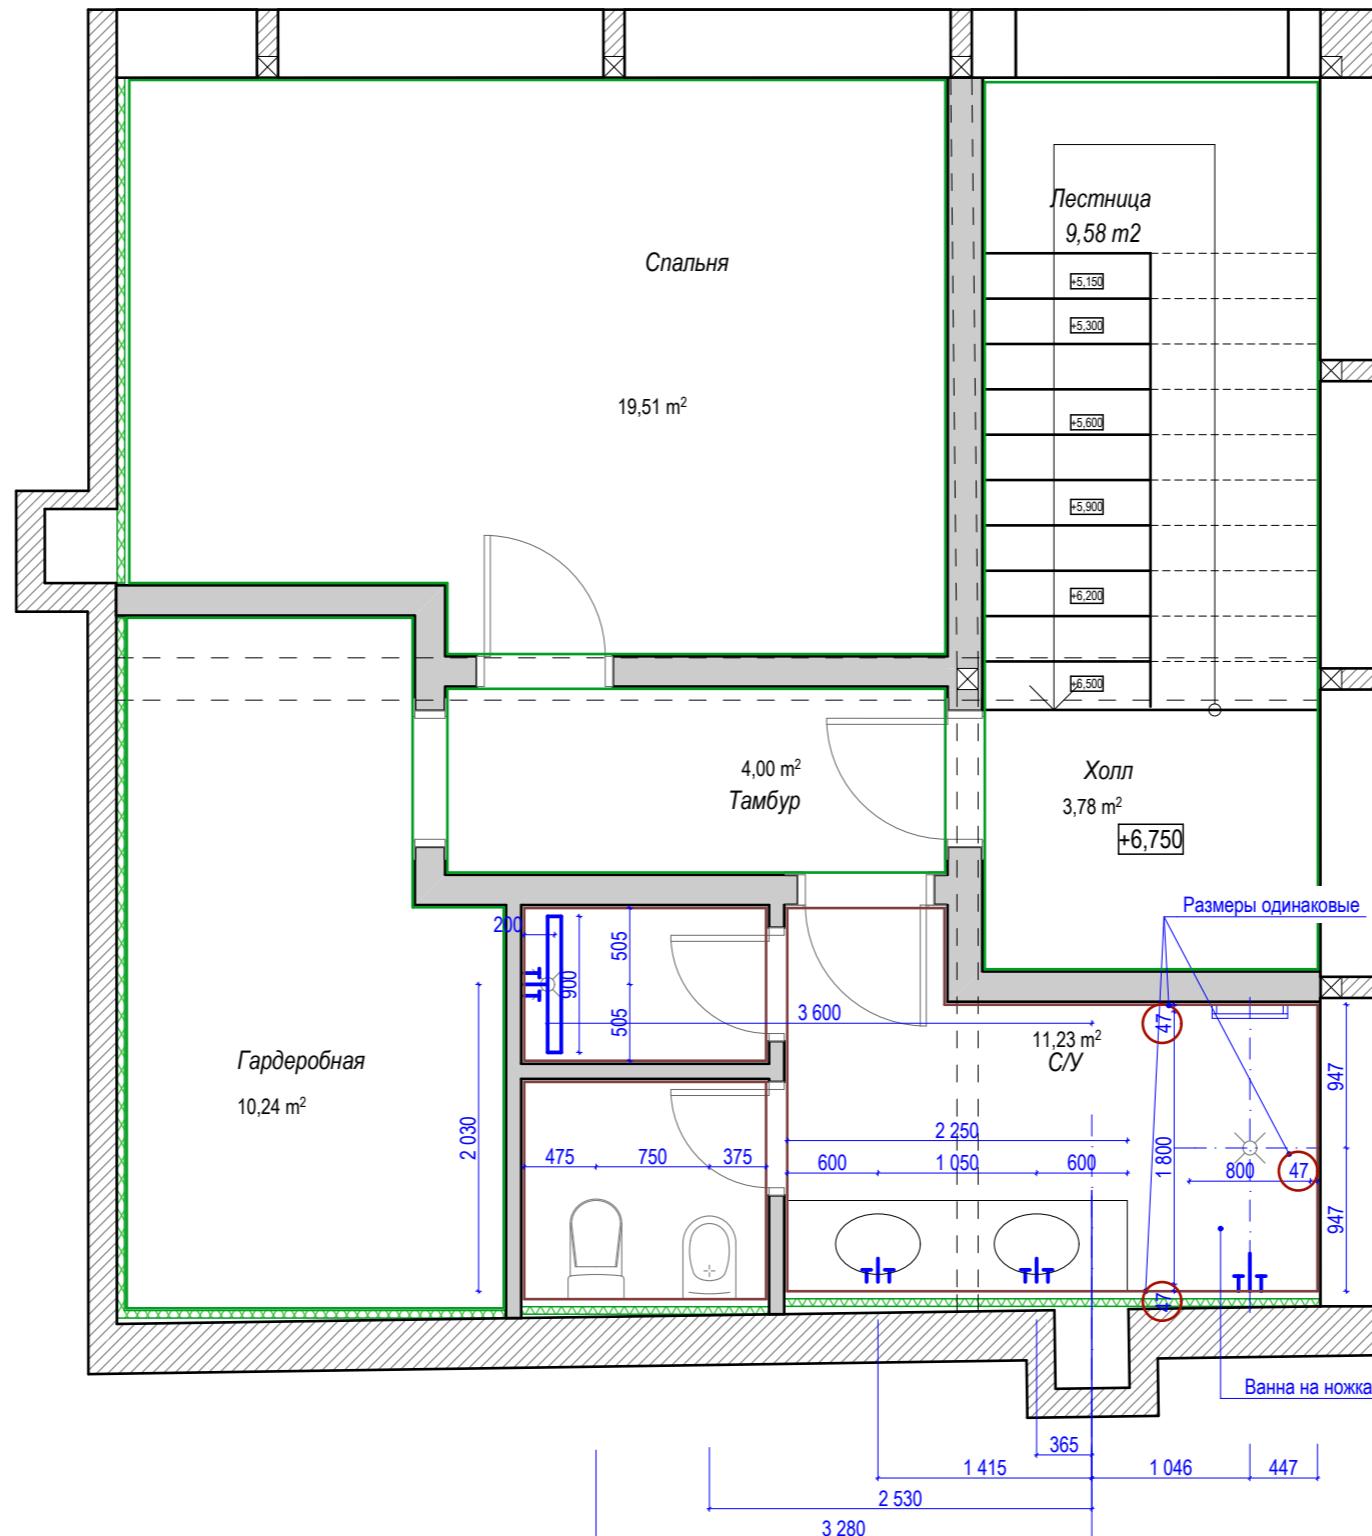


Схема размещения сантехники мансардного этажа.

Масштаб	Лист	Листов
1:50	22	46

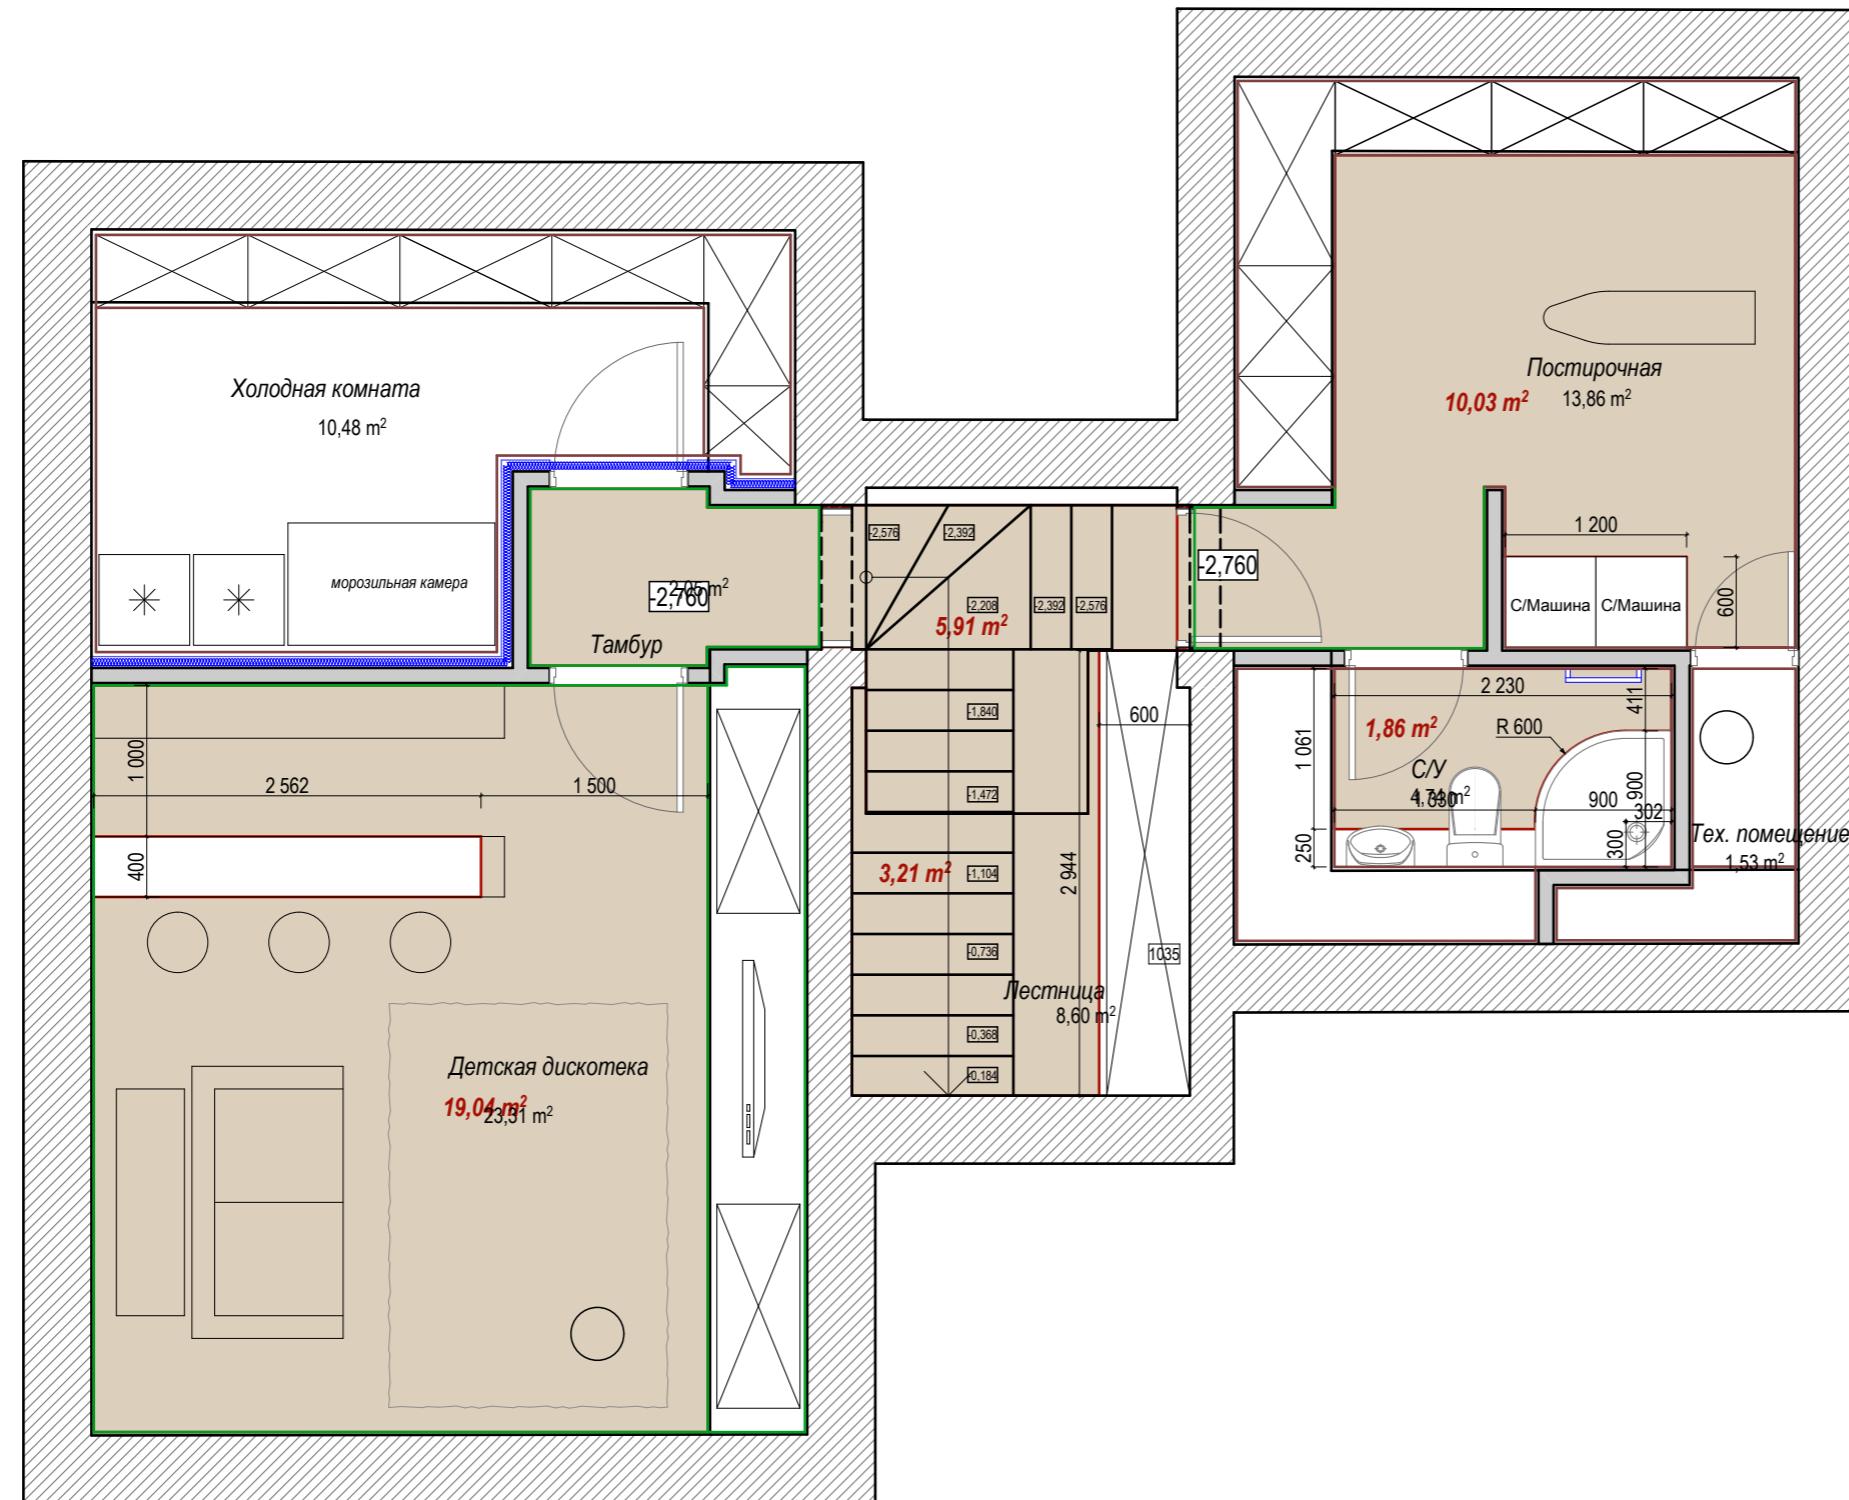


Тёплый пол - общая площадь 34,89 м²

Паркет

Паркет 20мм
Клей
Фанера 20мм
Клей
Цементно песчаная стяжка
Керамзитобетон
Шумоизоляция
Пароизоляция


Ж/Б плита перекрытия
20
180

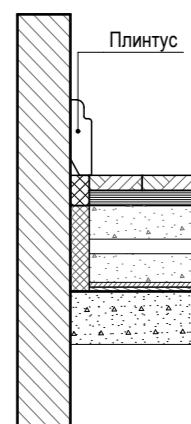

Примечание:

1. Состав пола с "тёплыми полами" уточняется дополнительно после утверждения плитки.

Схема напольного покрытия и тёплых полов цокольного этажа.	Масштаб	Лист	Листов
	1:50, 1:10	23	46

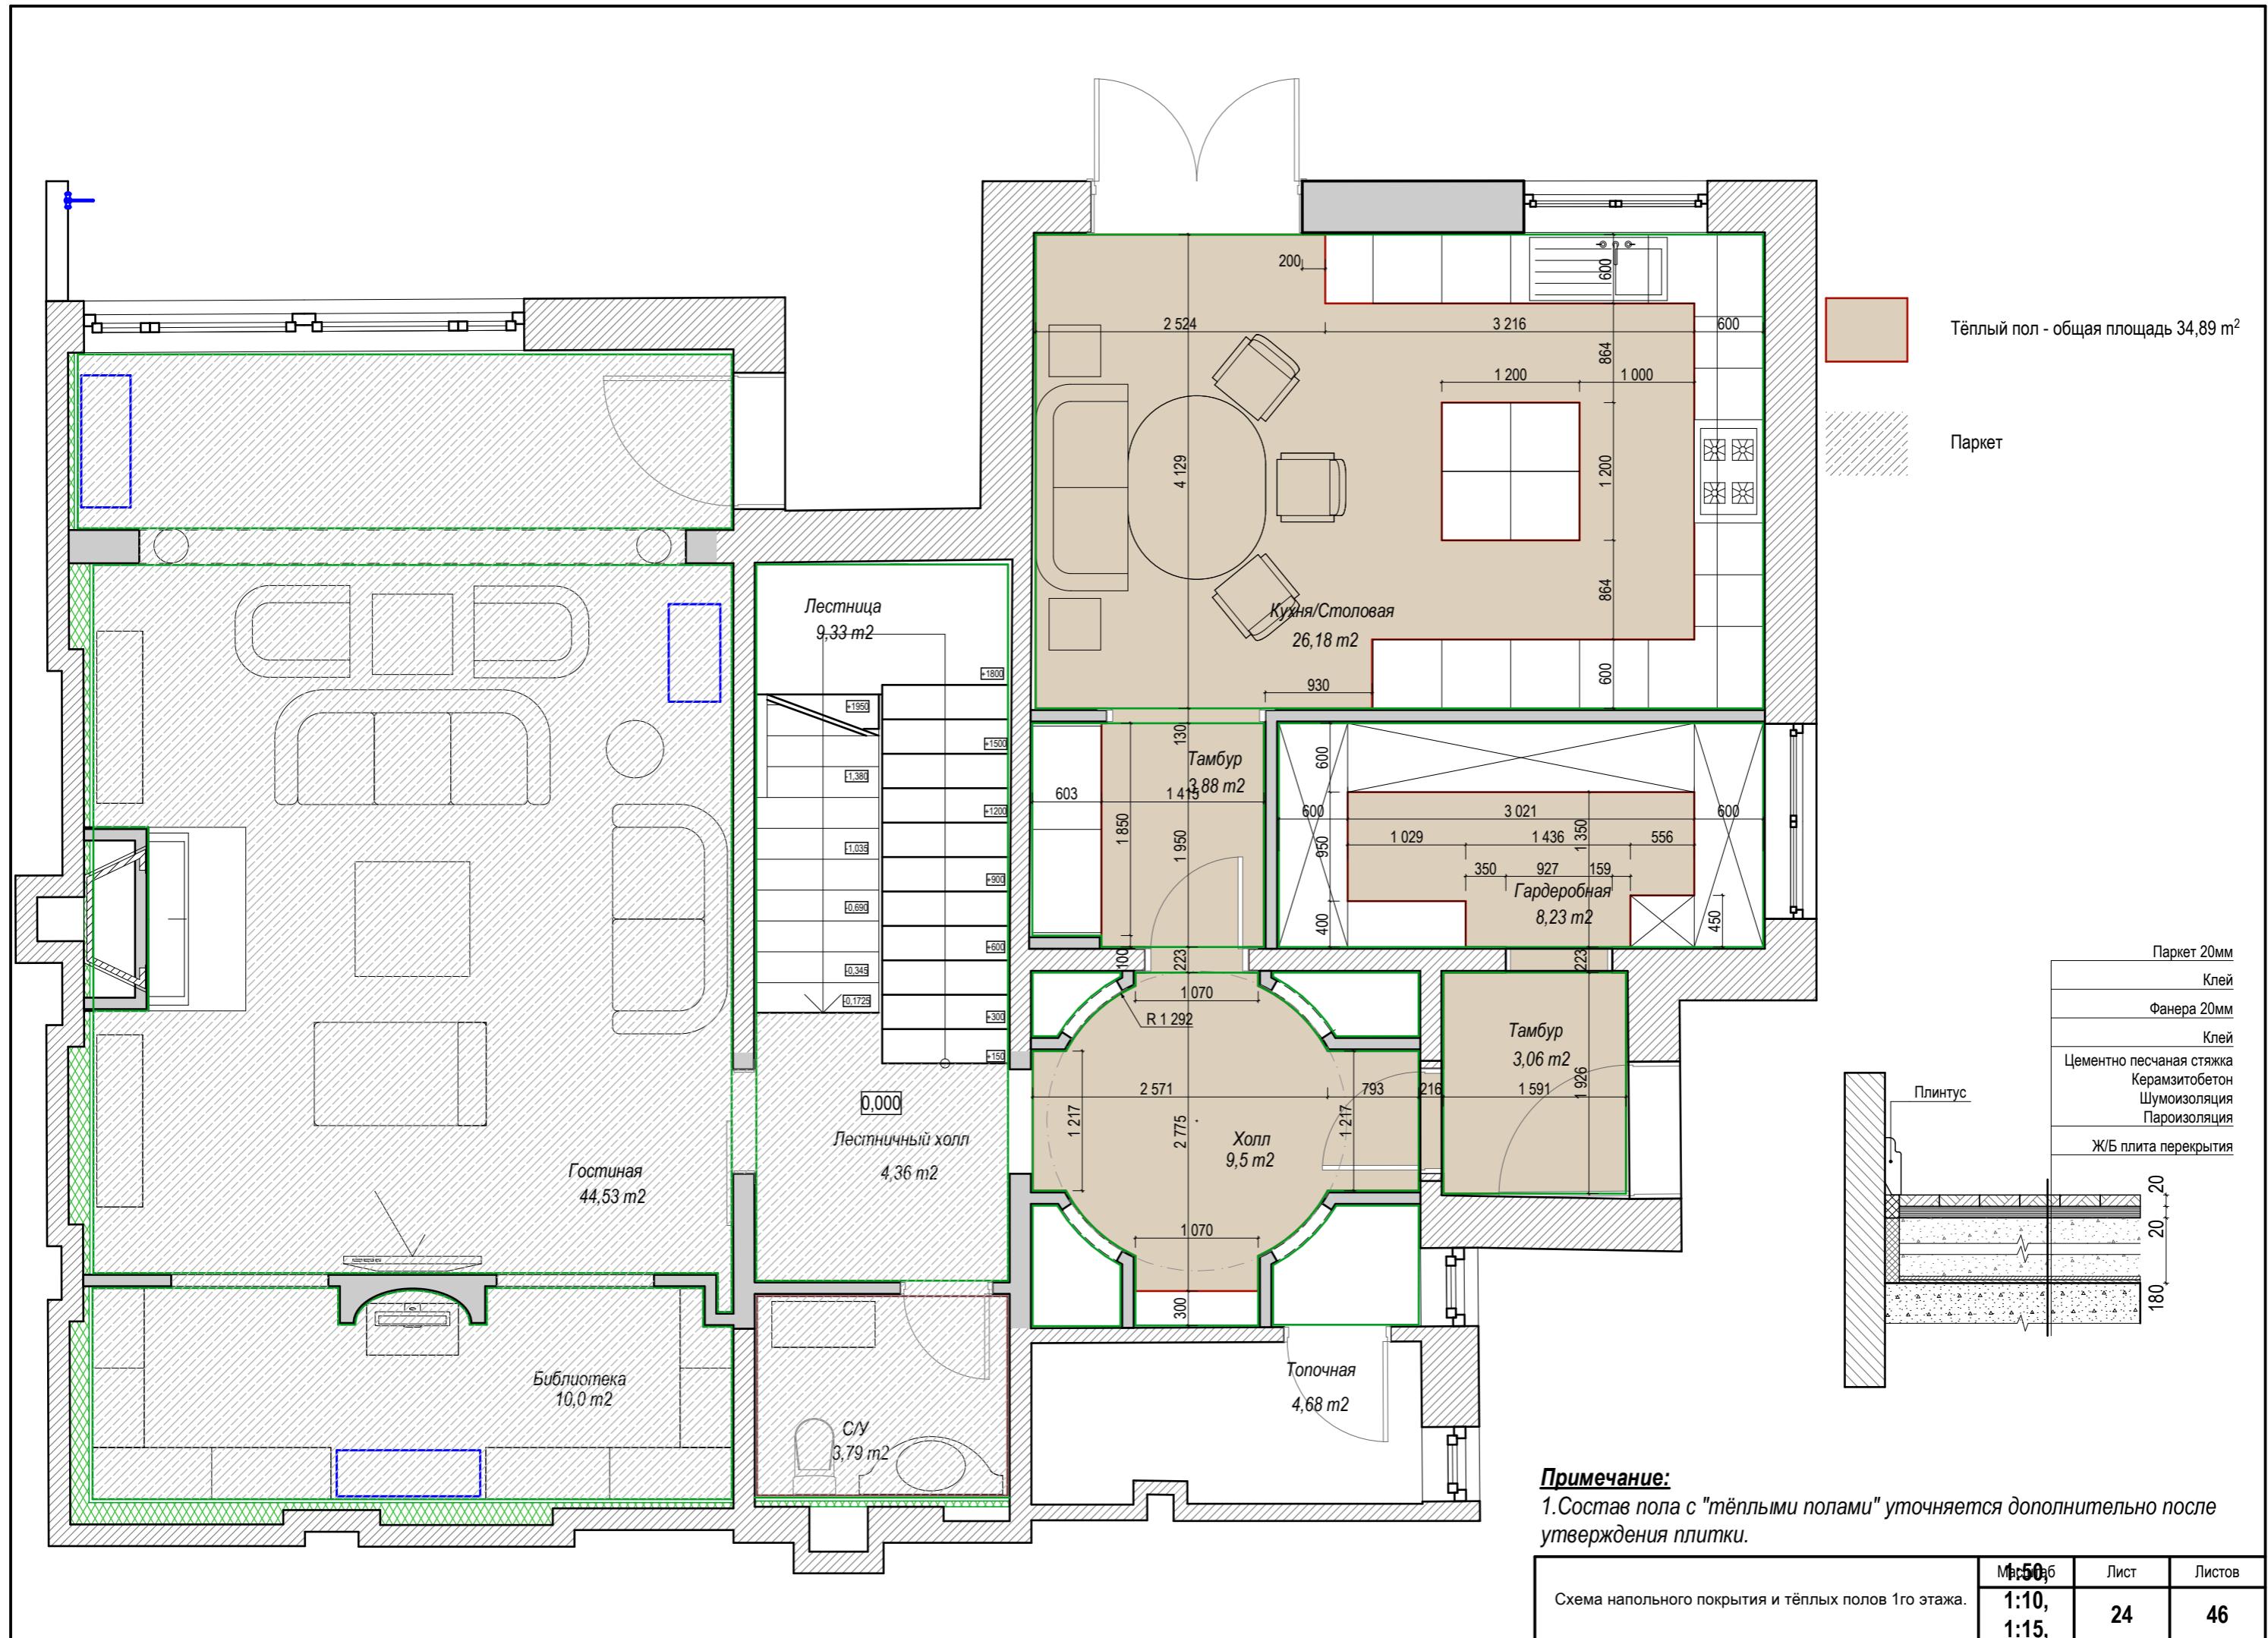


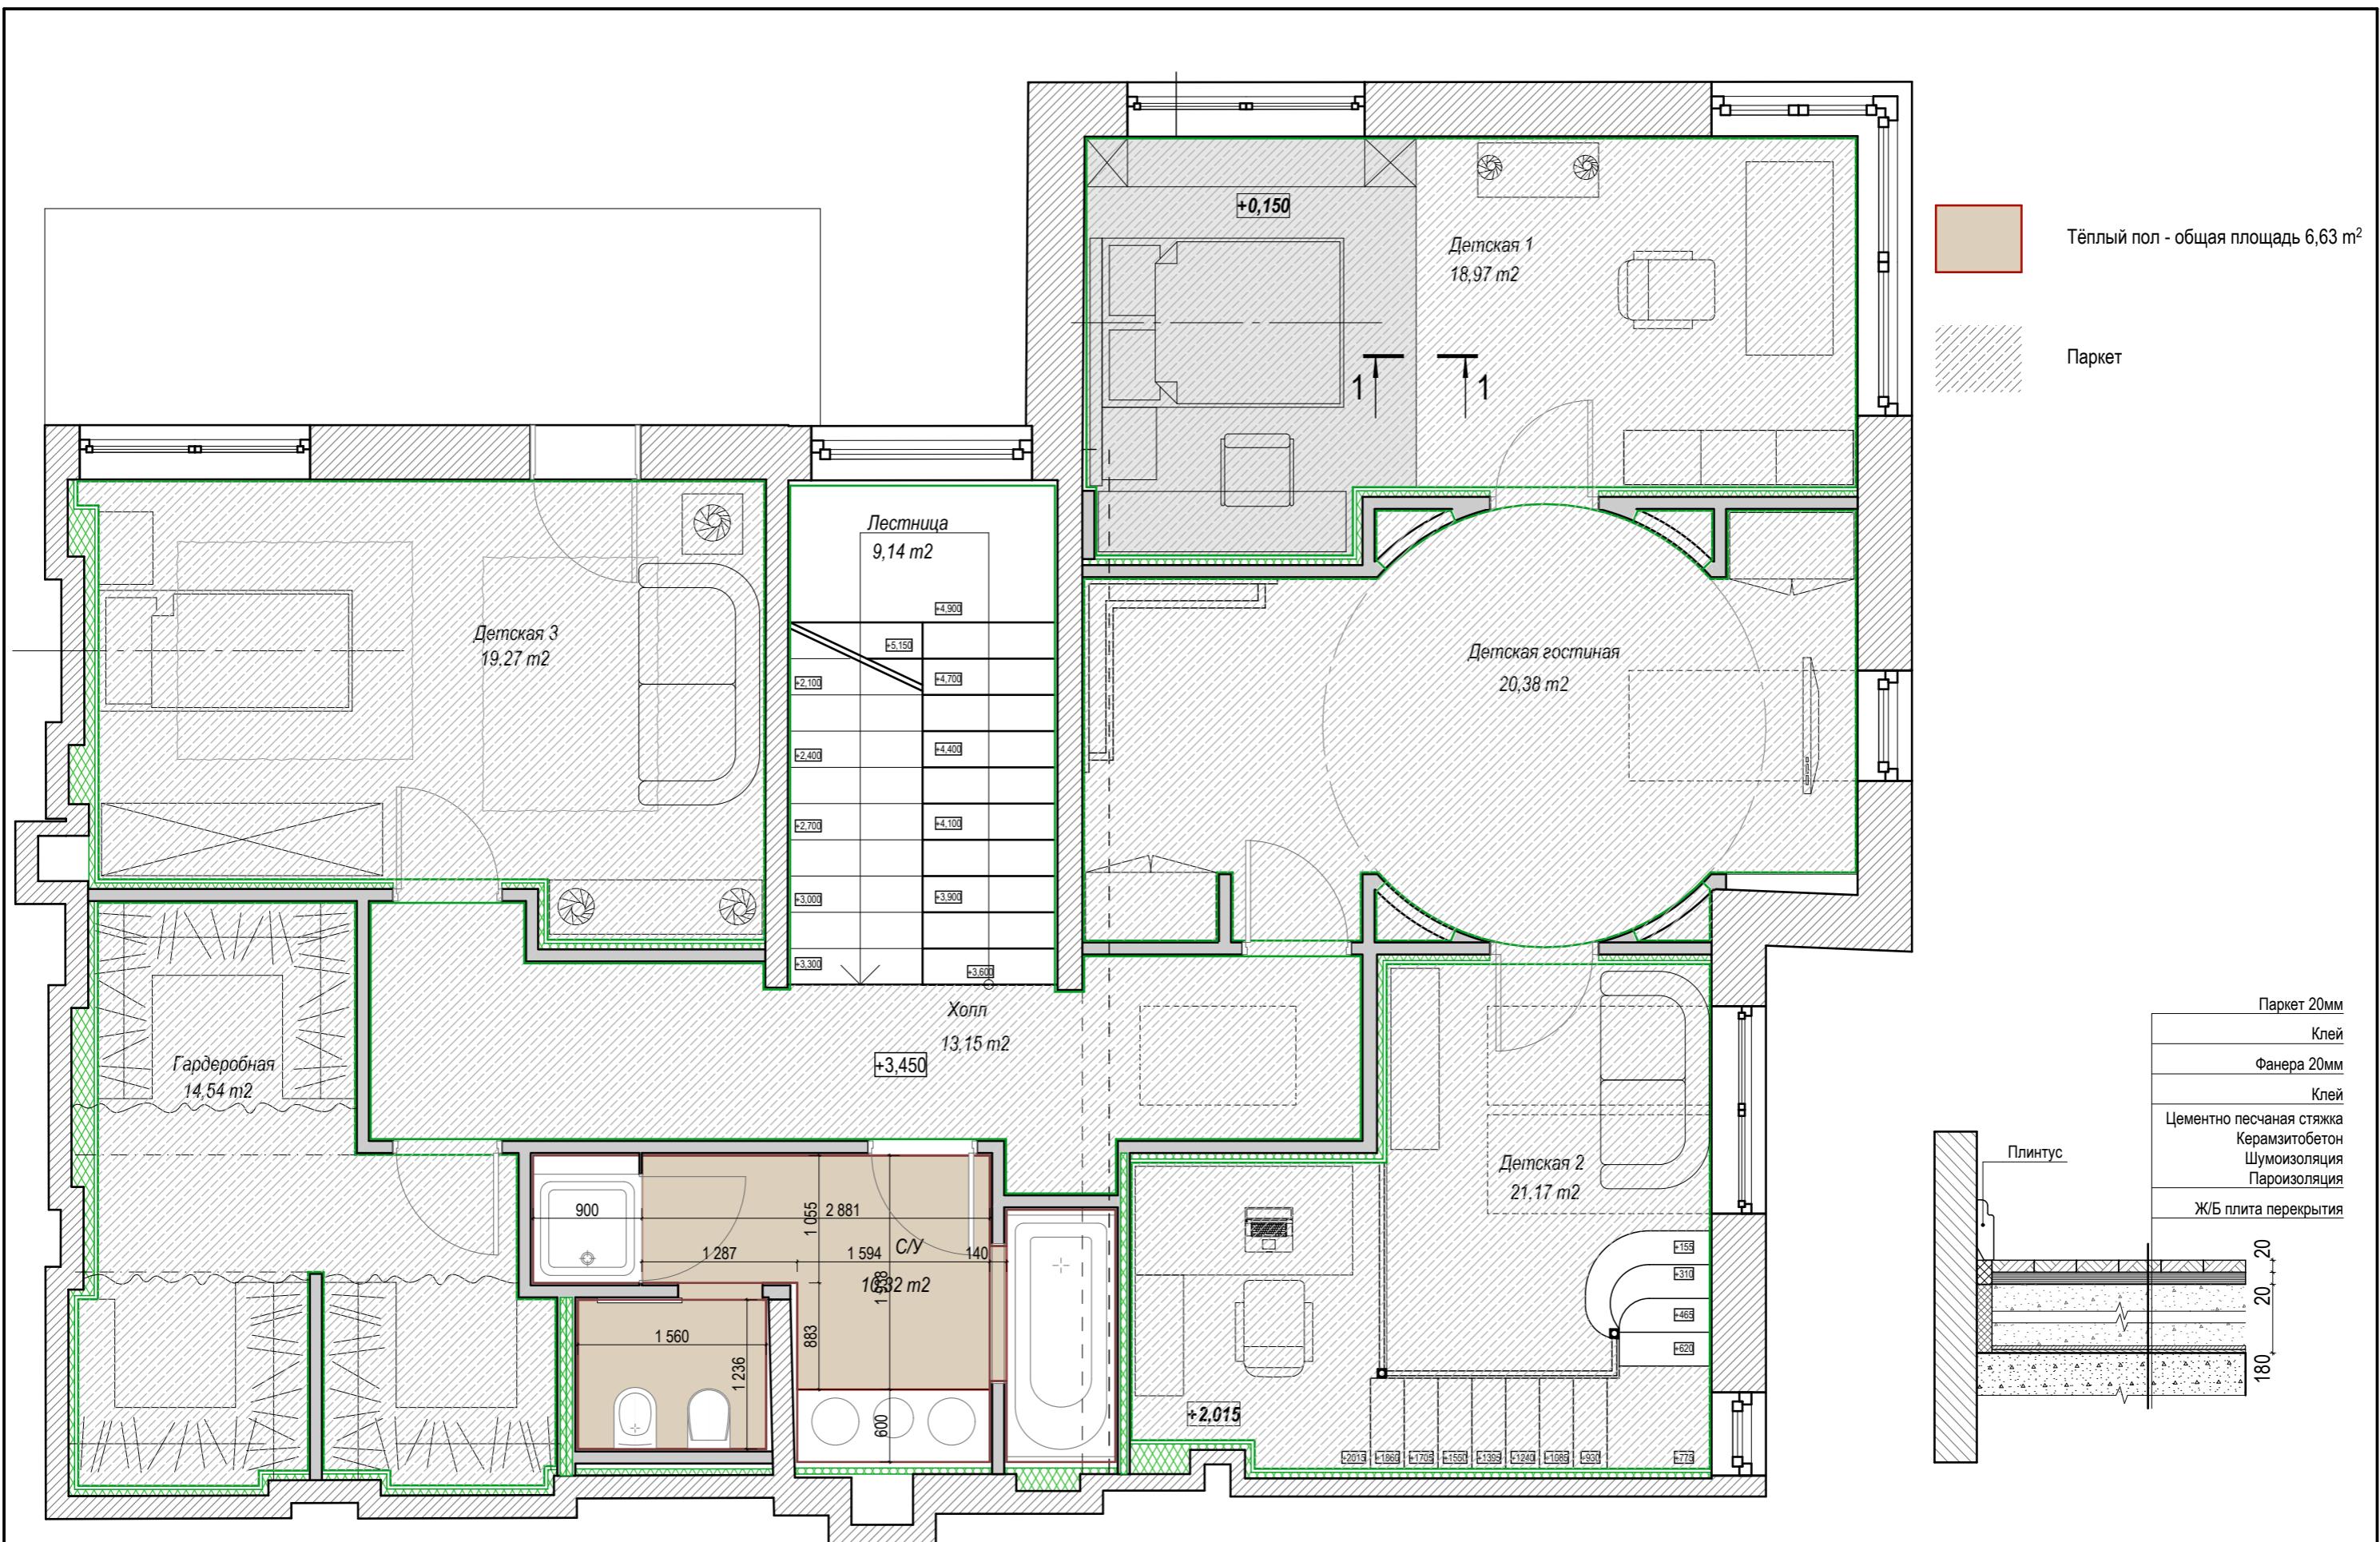


Схема напольного покрытия и тёплых полов 2го этажа.	Масштаб	Лист	Листов
	1:50, 1:10	25	46



Тёплый пол - общая площадь 5,45 м²


Паркет

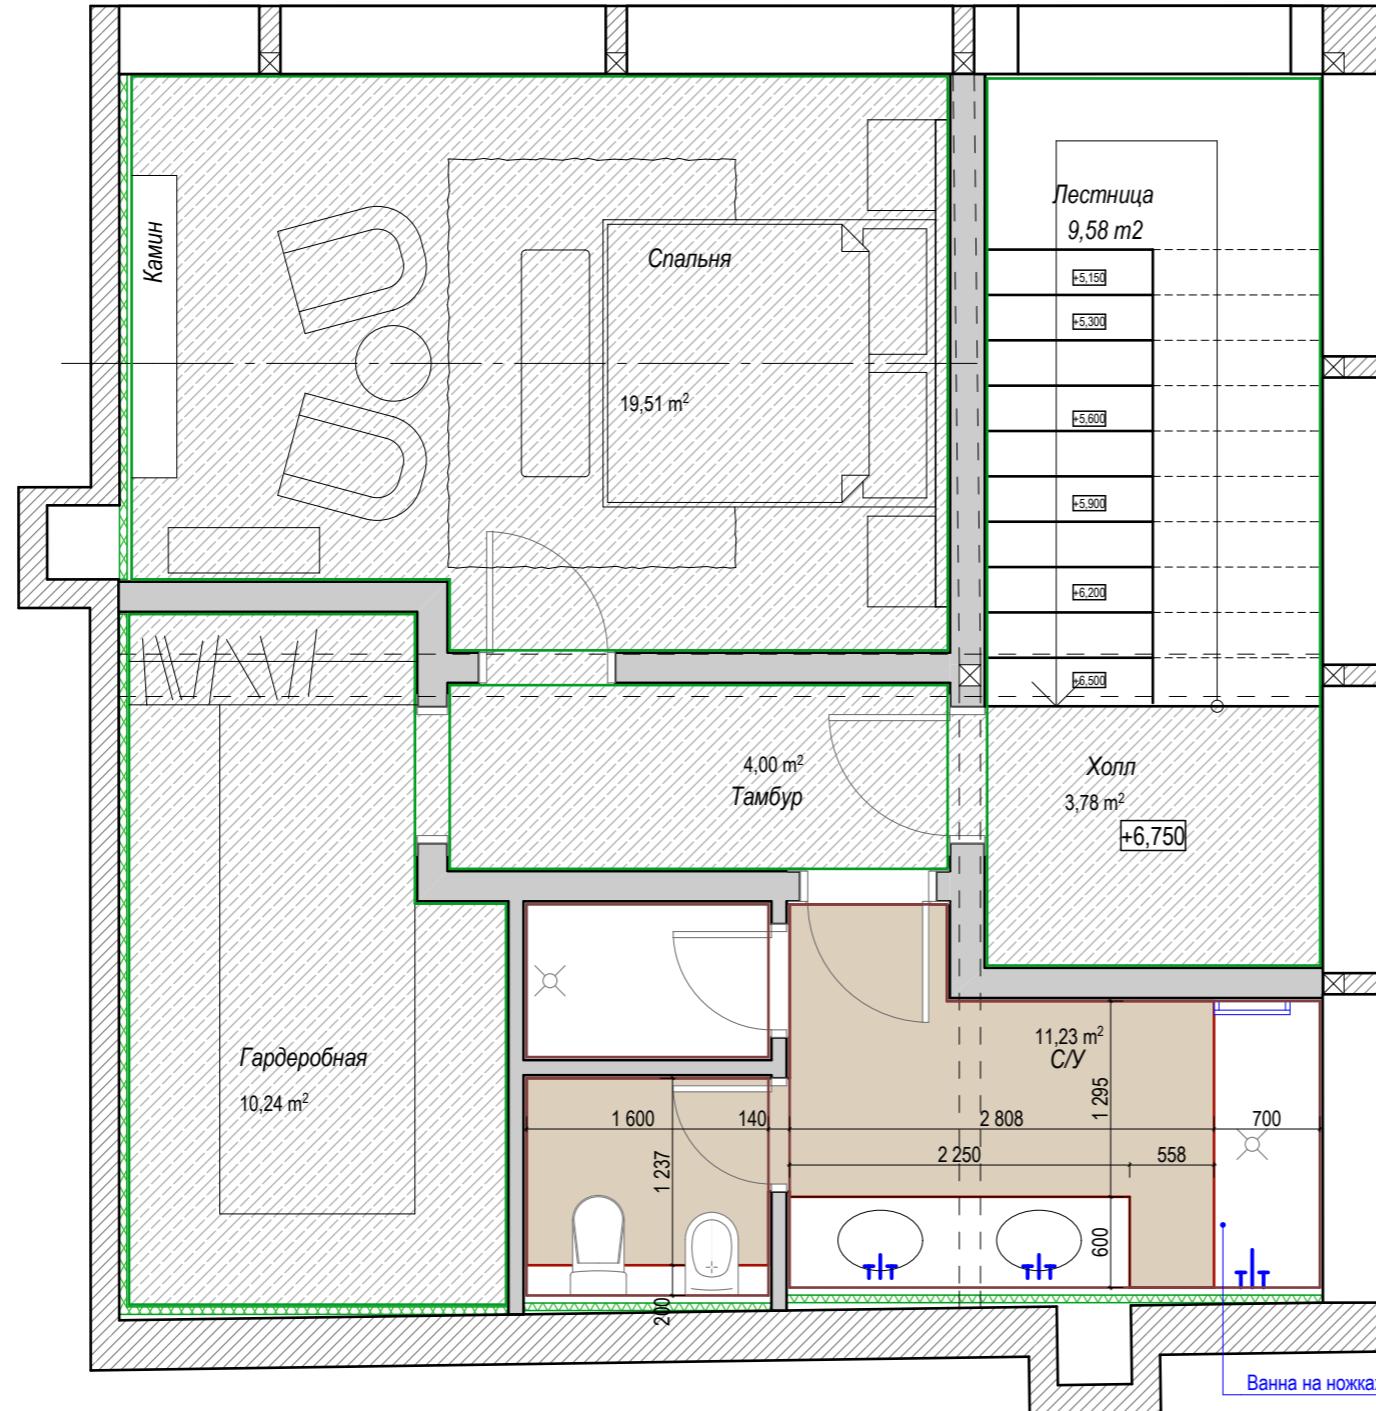

Примечание:

1. Состав пола с "тёплыми полами" уточняется дополнительно после утверждения плитки.


Схема напольного покрытия и тёплых полов мансардного этажа.	Масштаб	Лист	Листов
	1:50, 1:10	26	46

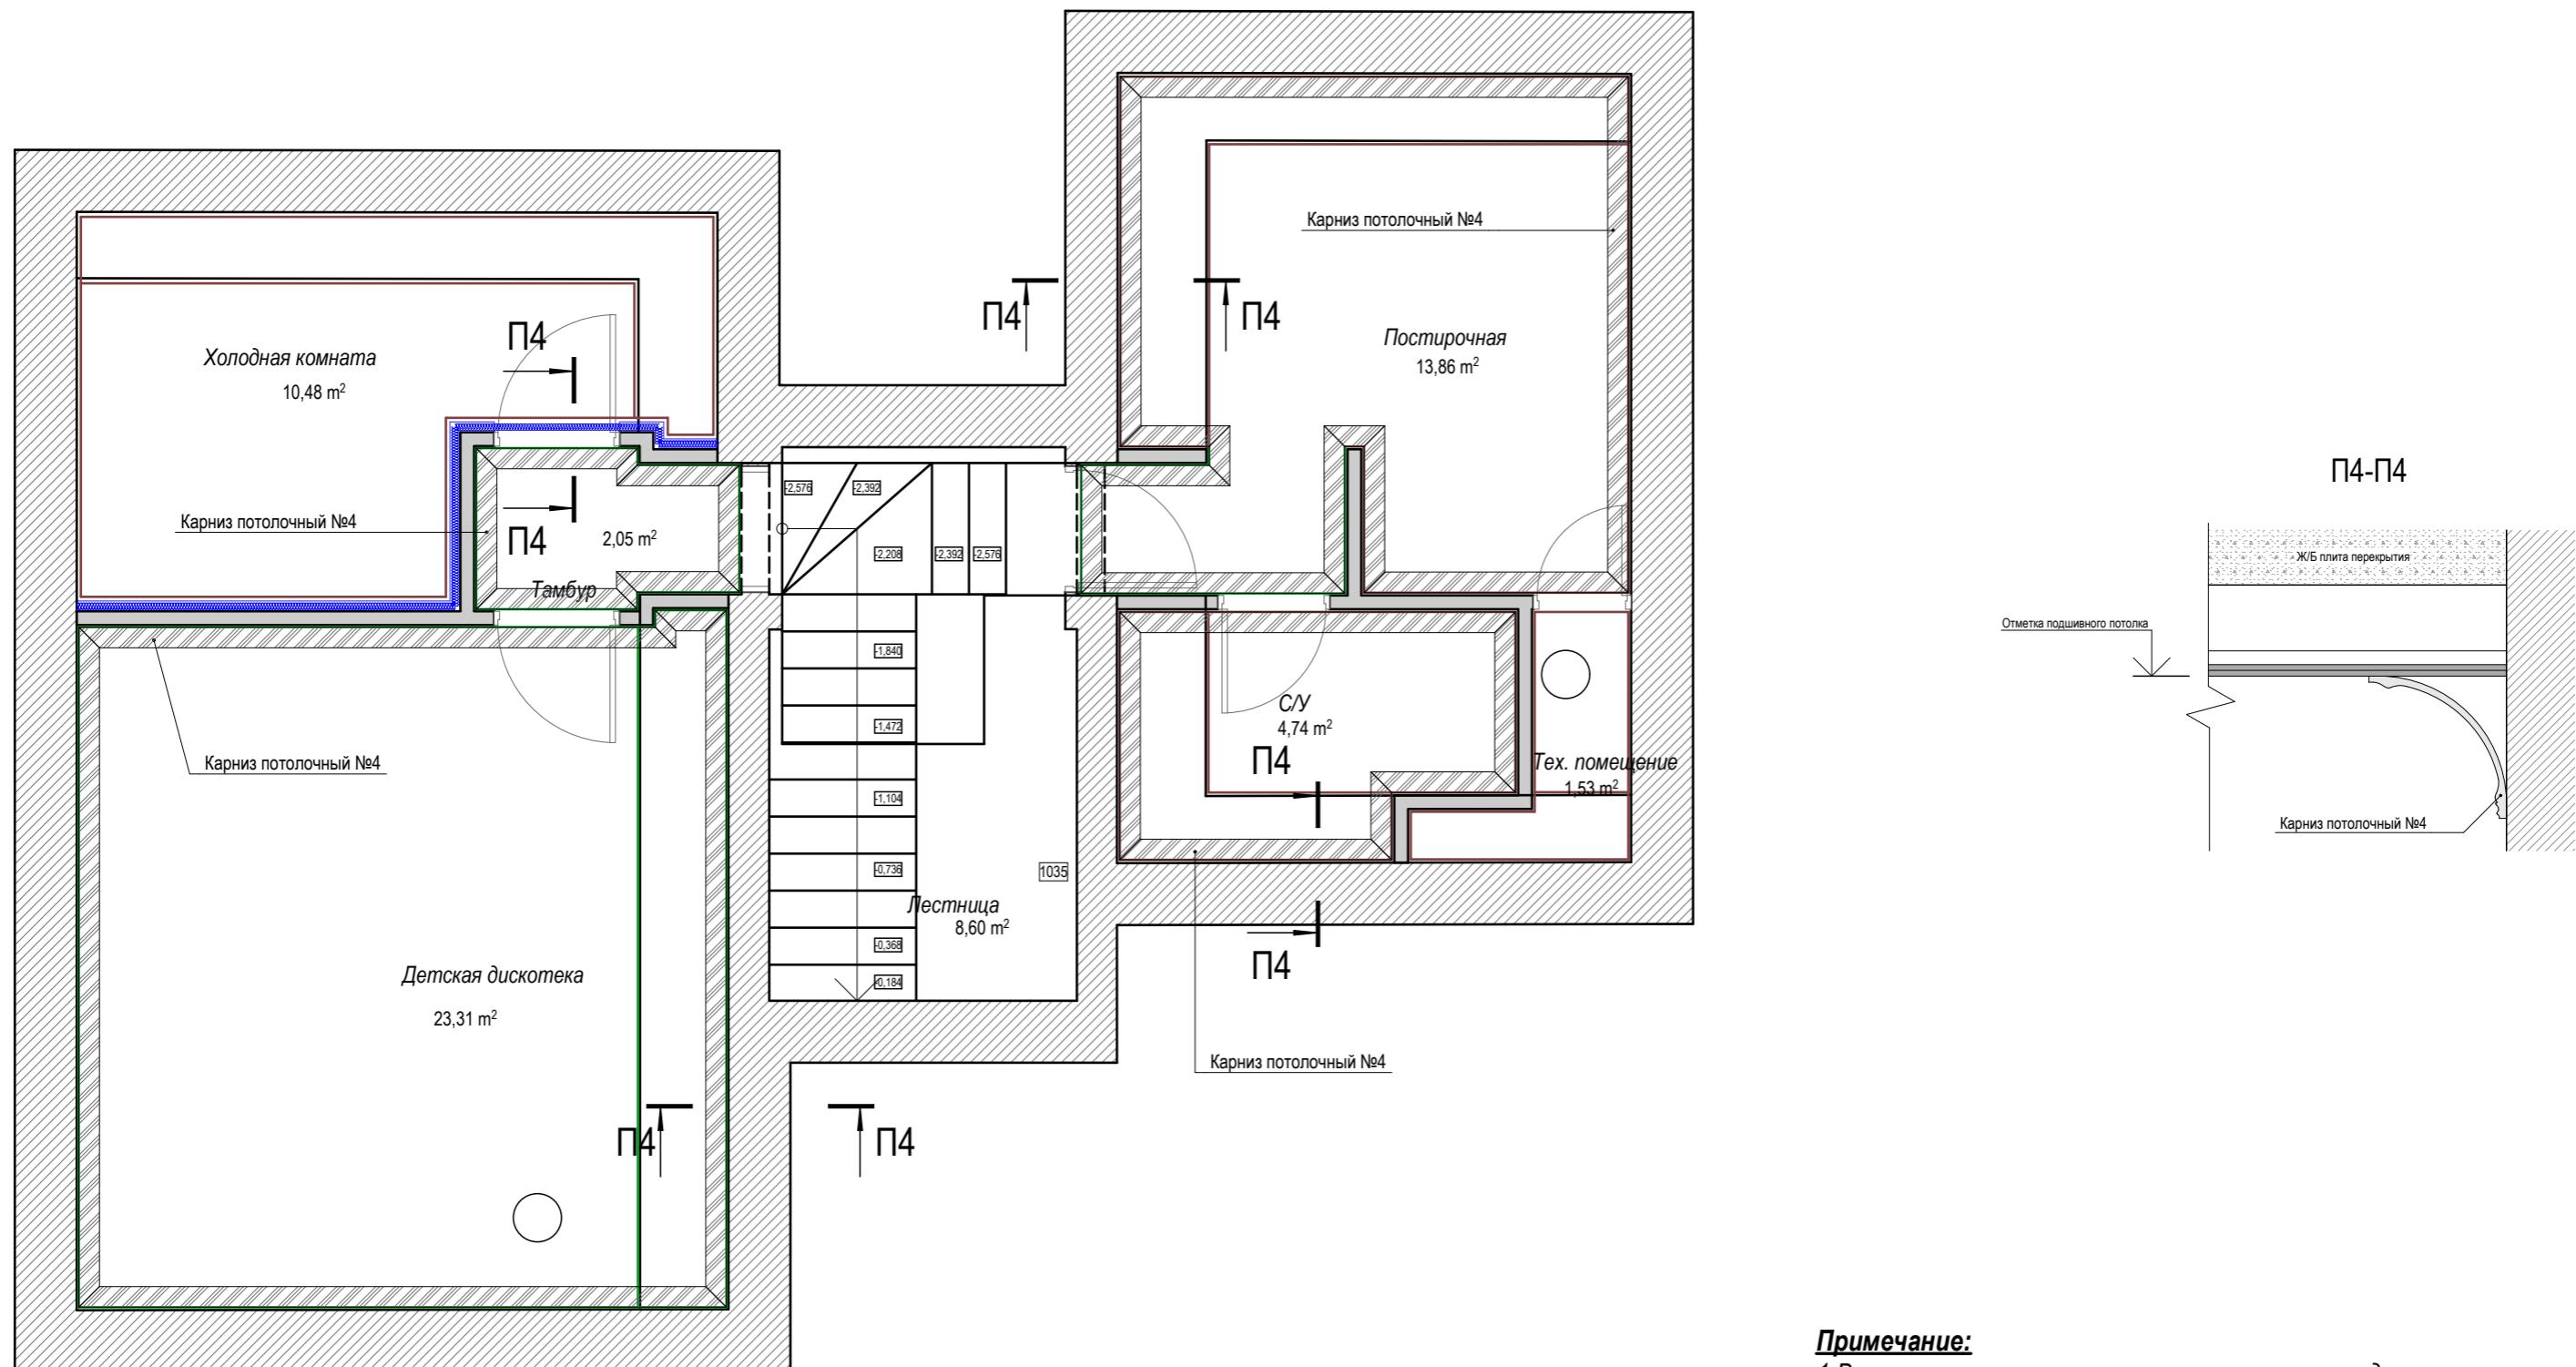


Примечание:

- Высоты потолков уточняются после утвержденного плана кондиционирования и вентиляции.
- Размеры со * уточняются после получения тех. карт от изготовителя кухонной мебели.
- Размеры с *** уточняются после утверждения камина.
- Цвета красок уточняются дополнительно.

План потолков цокольного этажа.	Масштаб 1:50, 1:15, AA	Лист 27	Листов 46
---------------------------------	---------------------------------	------------	--------------

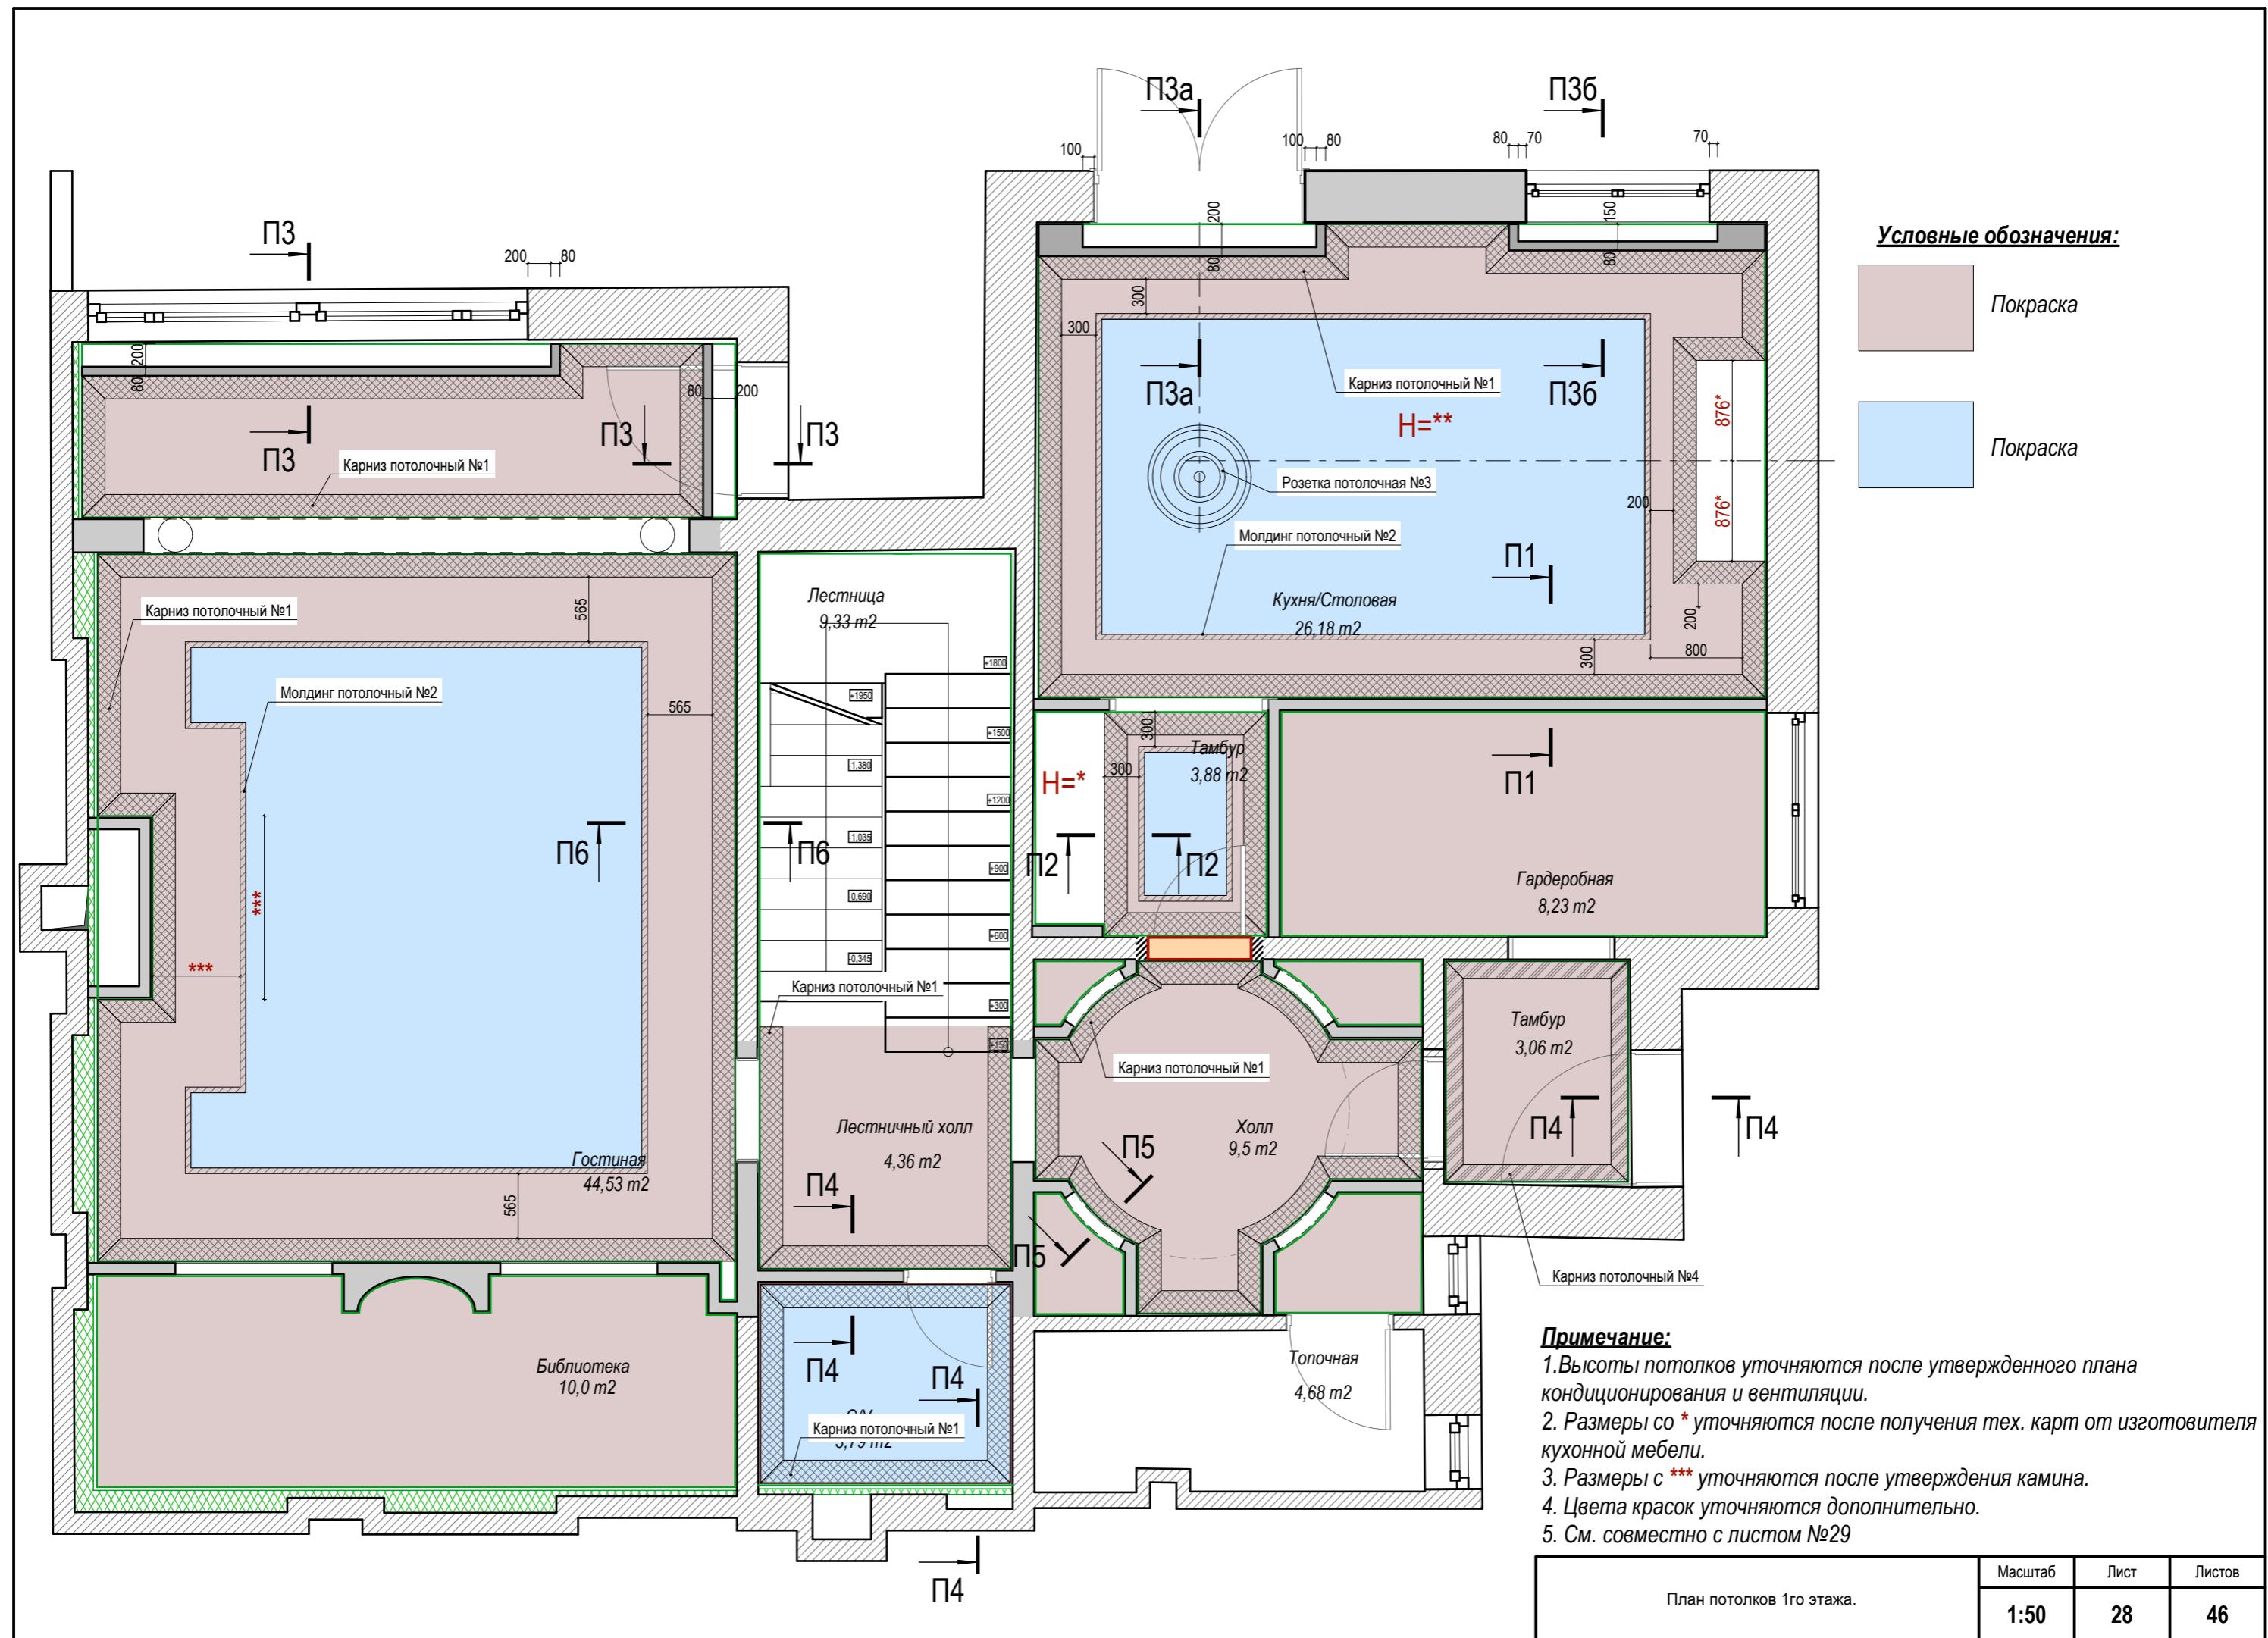


П1-П1

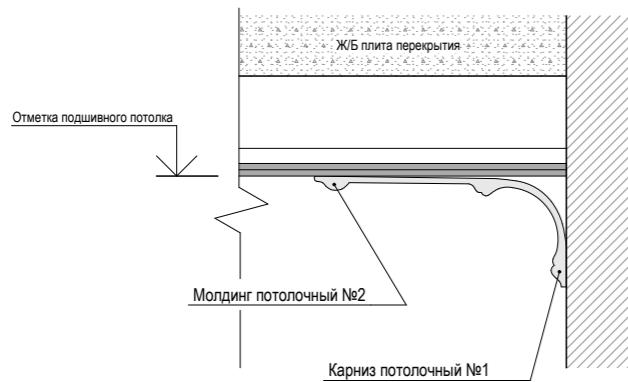


П2-П2




П3-П3

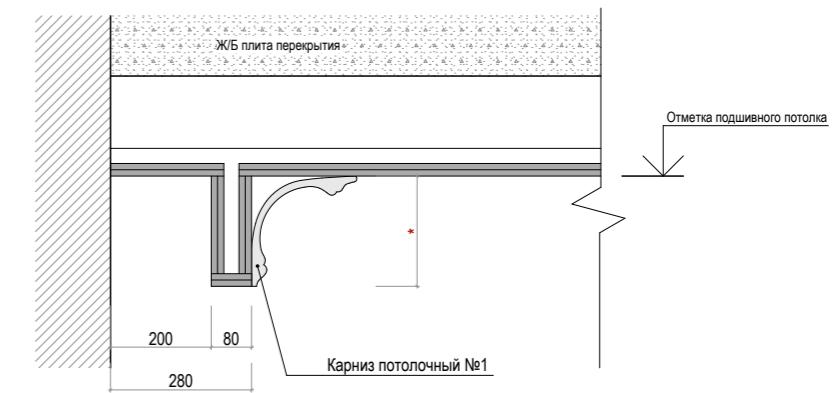


П3а-П3а

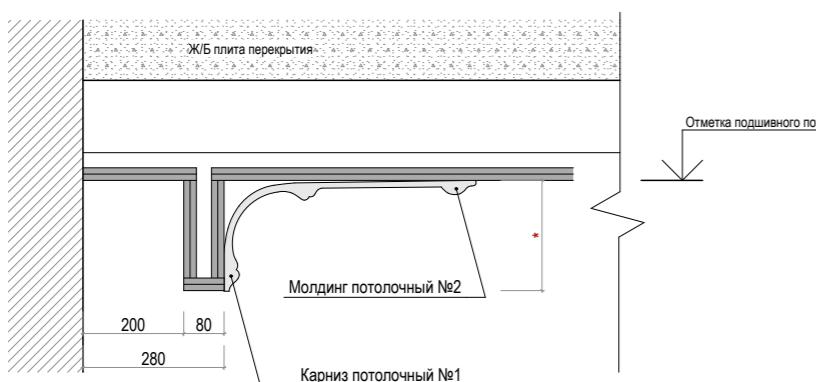


П3б-П3б

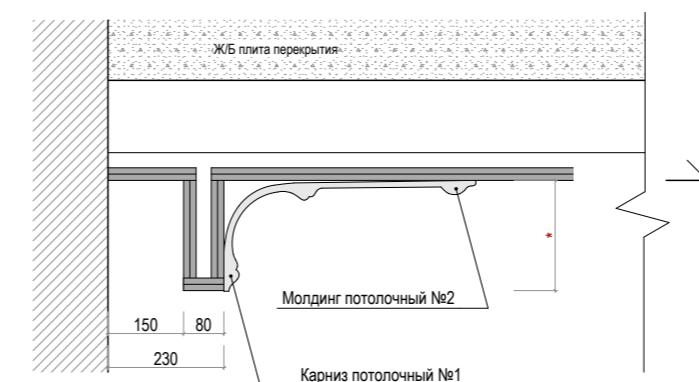


П4-П4

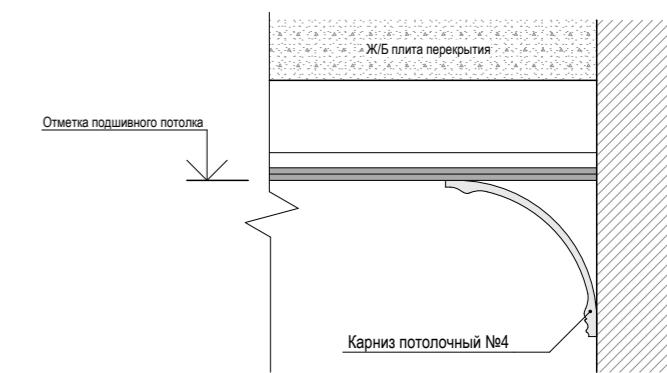

П5-П5

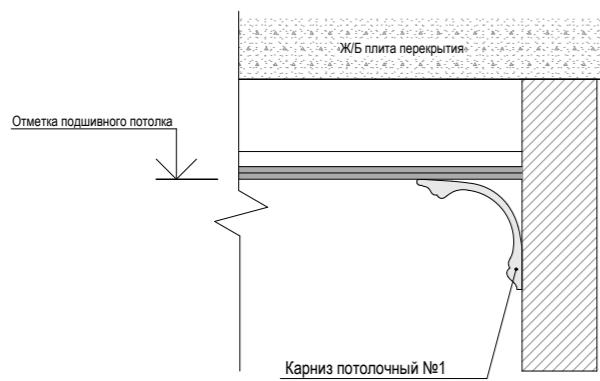


П6-П6

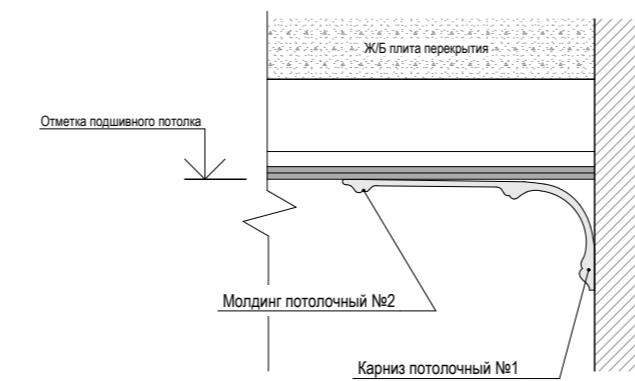

Примечание:

1. Высоты потолков уточняются после утвержденного плана кондиционирования и вентиляции.
2. См. совместно с листом №28
3. Размеры * - уточнить после утверждения карнизов.

Сечение потолков 1го этажа.	Масштаб	Лист	Листов
	1:15, 00	29	46

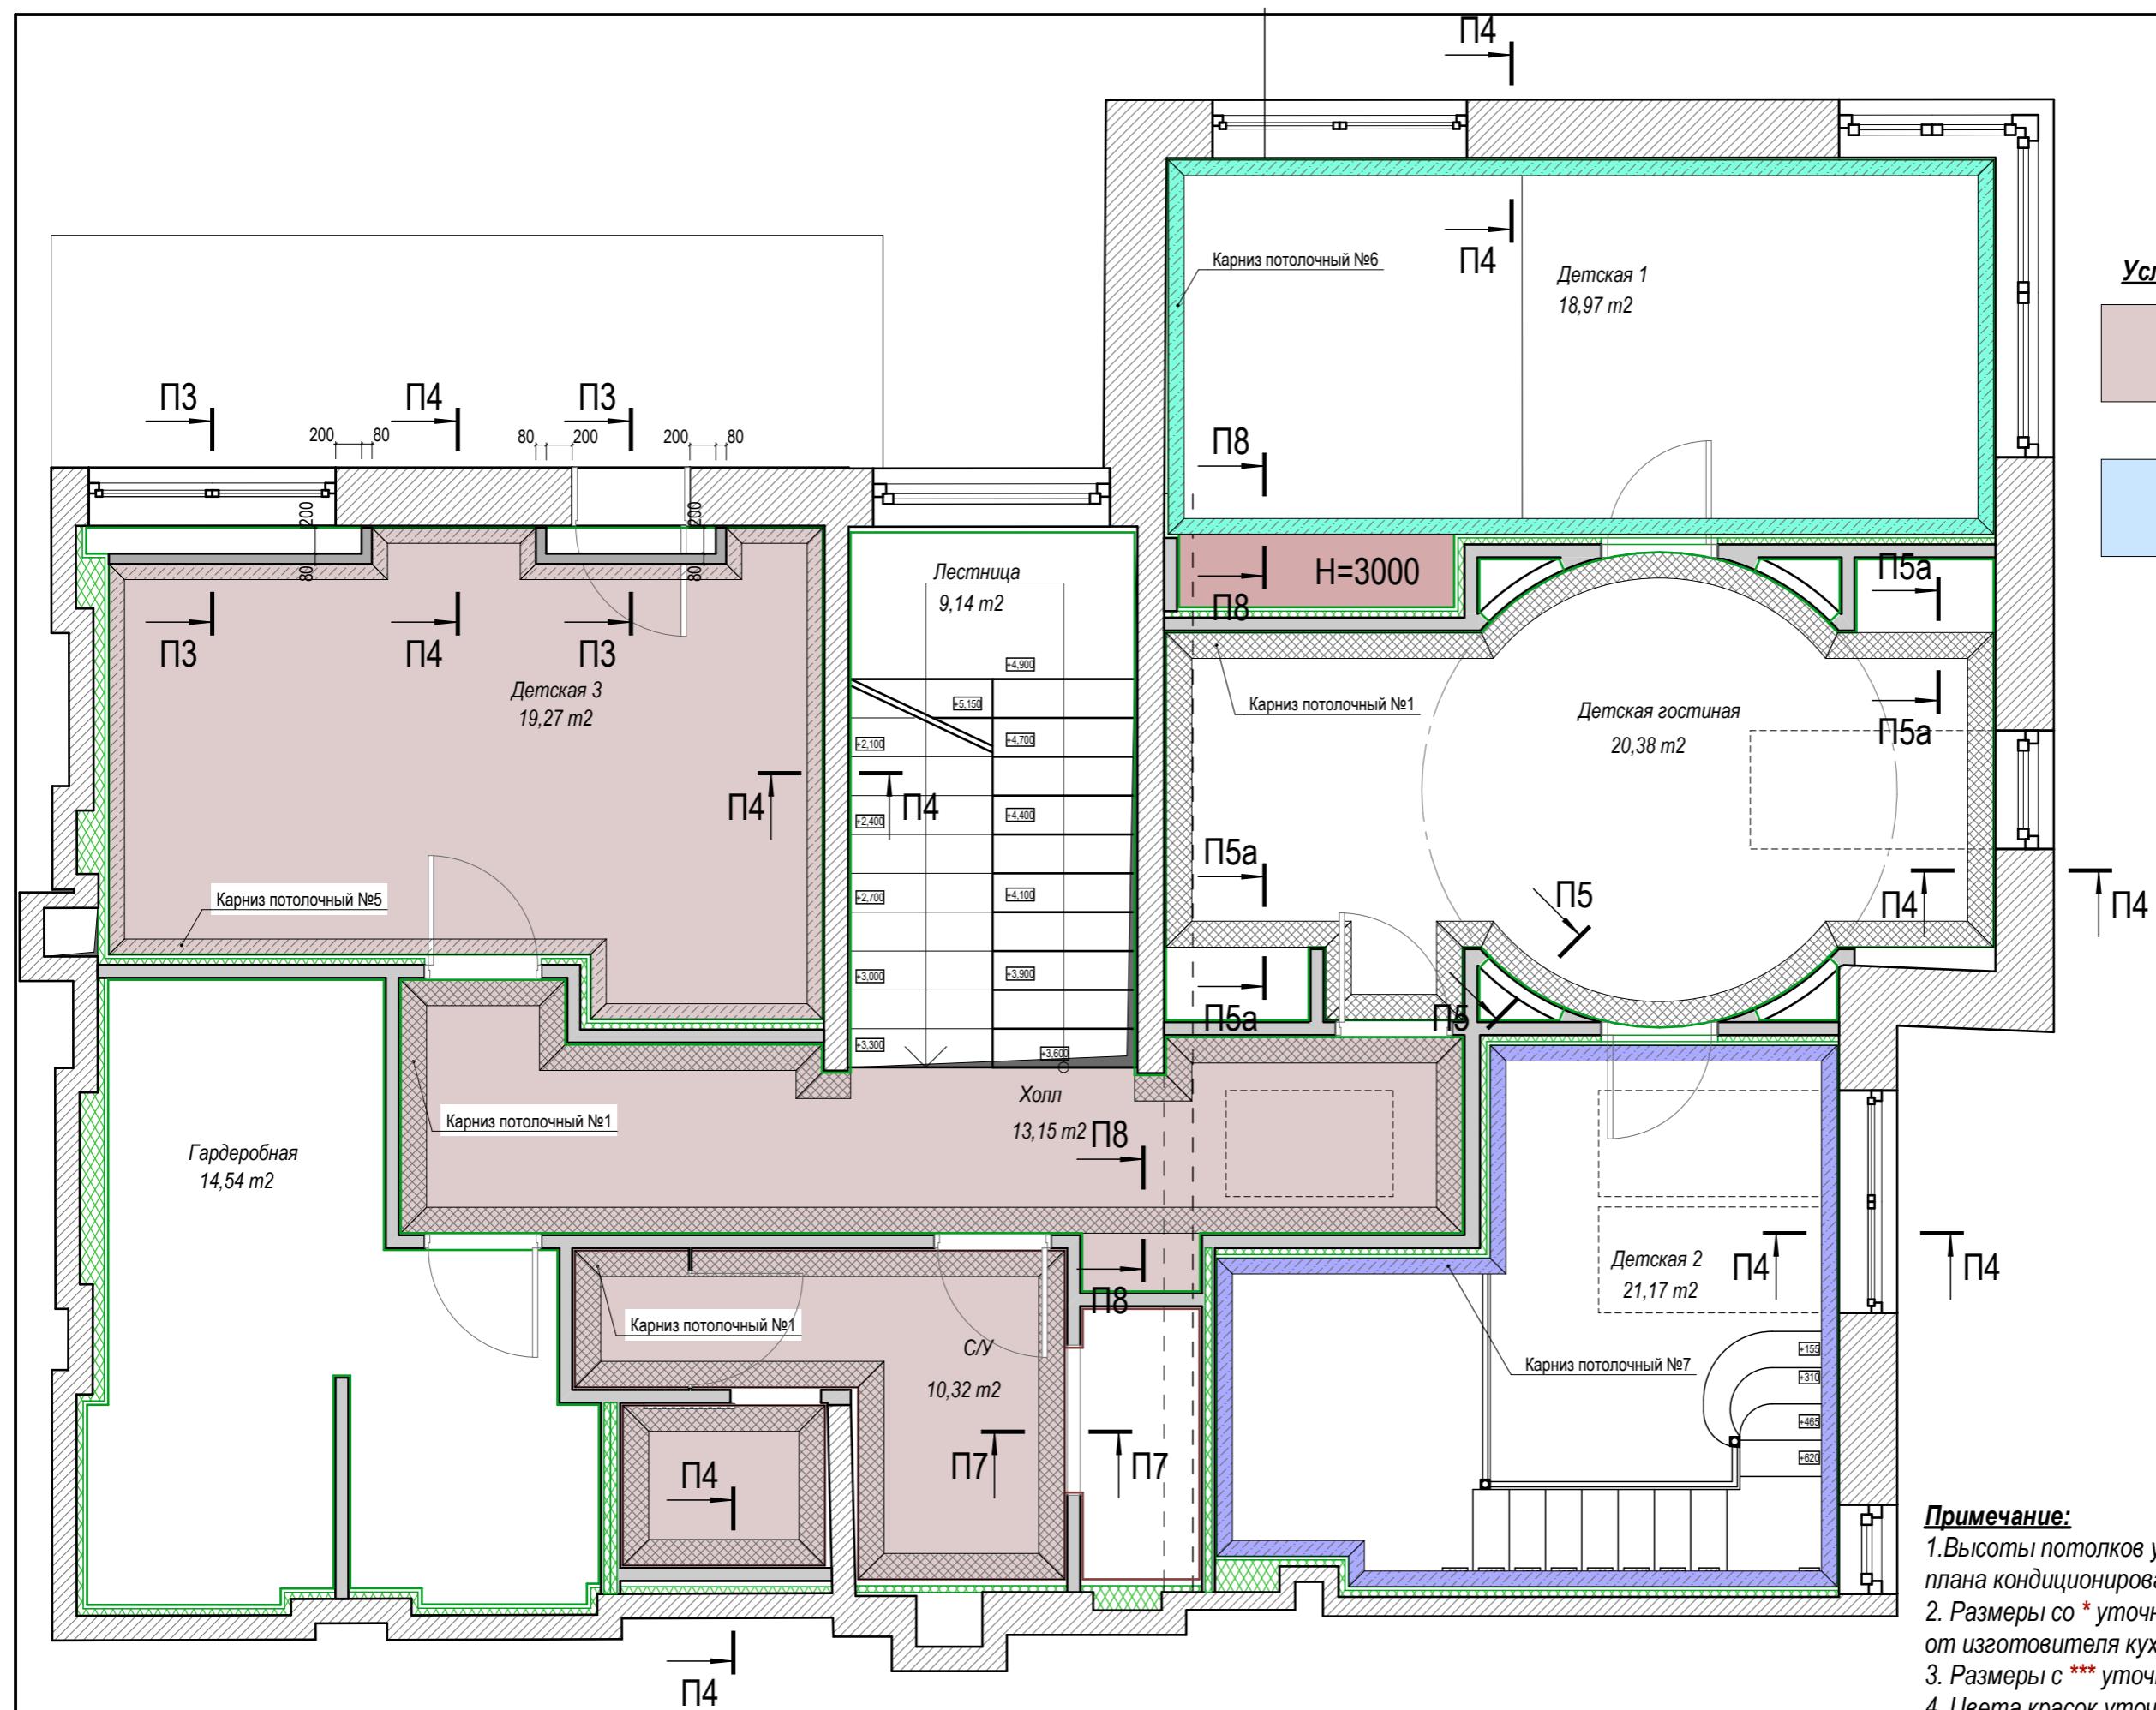

Условные обозначения:

Покраска




Примечание:

1. Высоты потолков уточняются после утвержденного плана кондиционирования и вентиляции.
 2. Размеры со * уточняются после получения тех. карт от изготовителя кухонной мебели.
 3. Размеры с *** уточняются после утверждения камина.
 4. Цвета красок уточняются дополнительно.
 5. См. совместно с листом №31

План потолков 2го этажа


План потолков 2го этажа.	Масштаб	Лист	Листов
	1:50	30	46

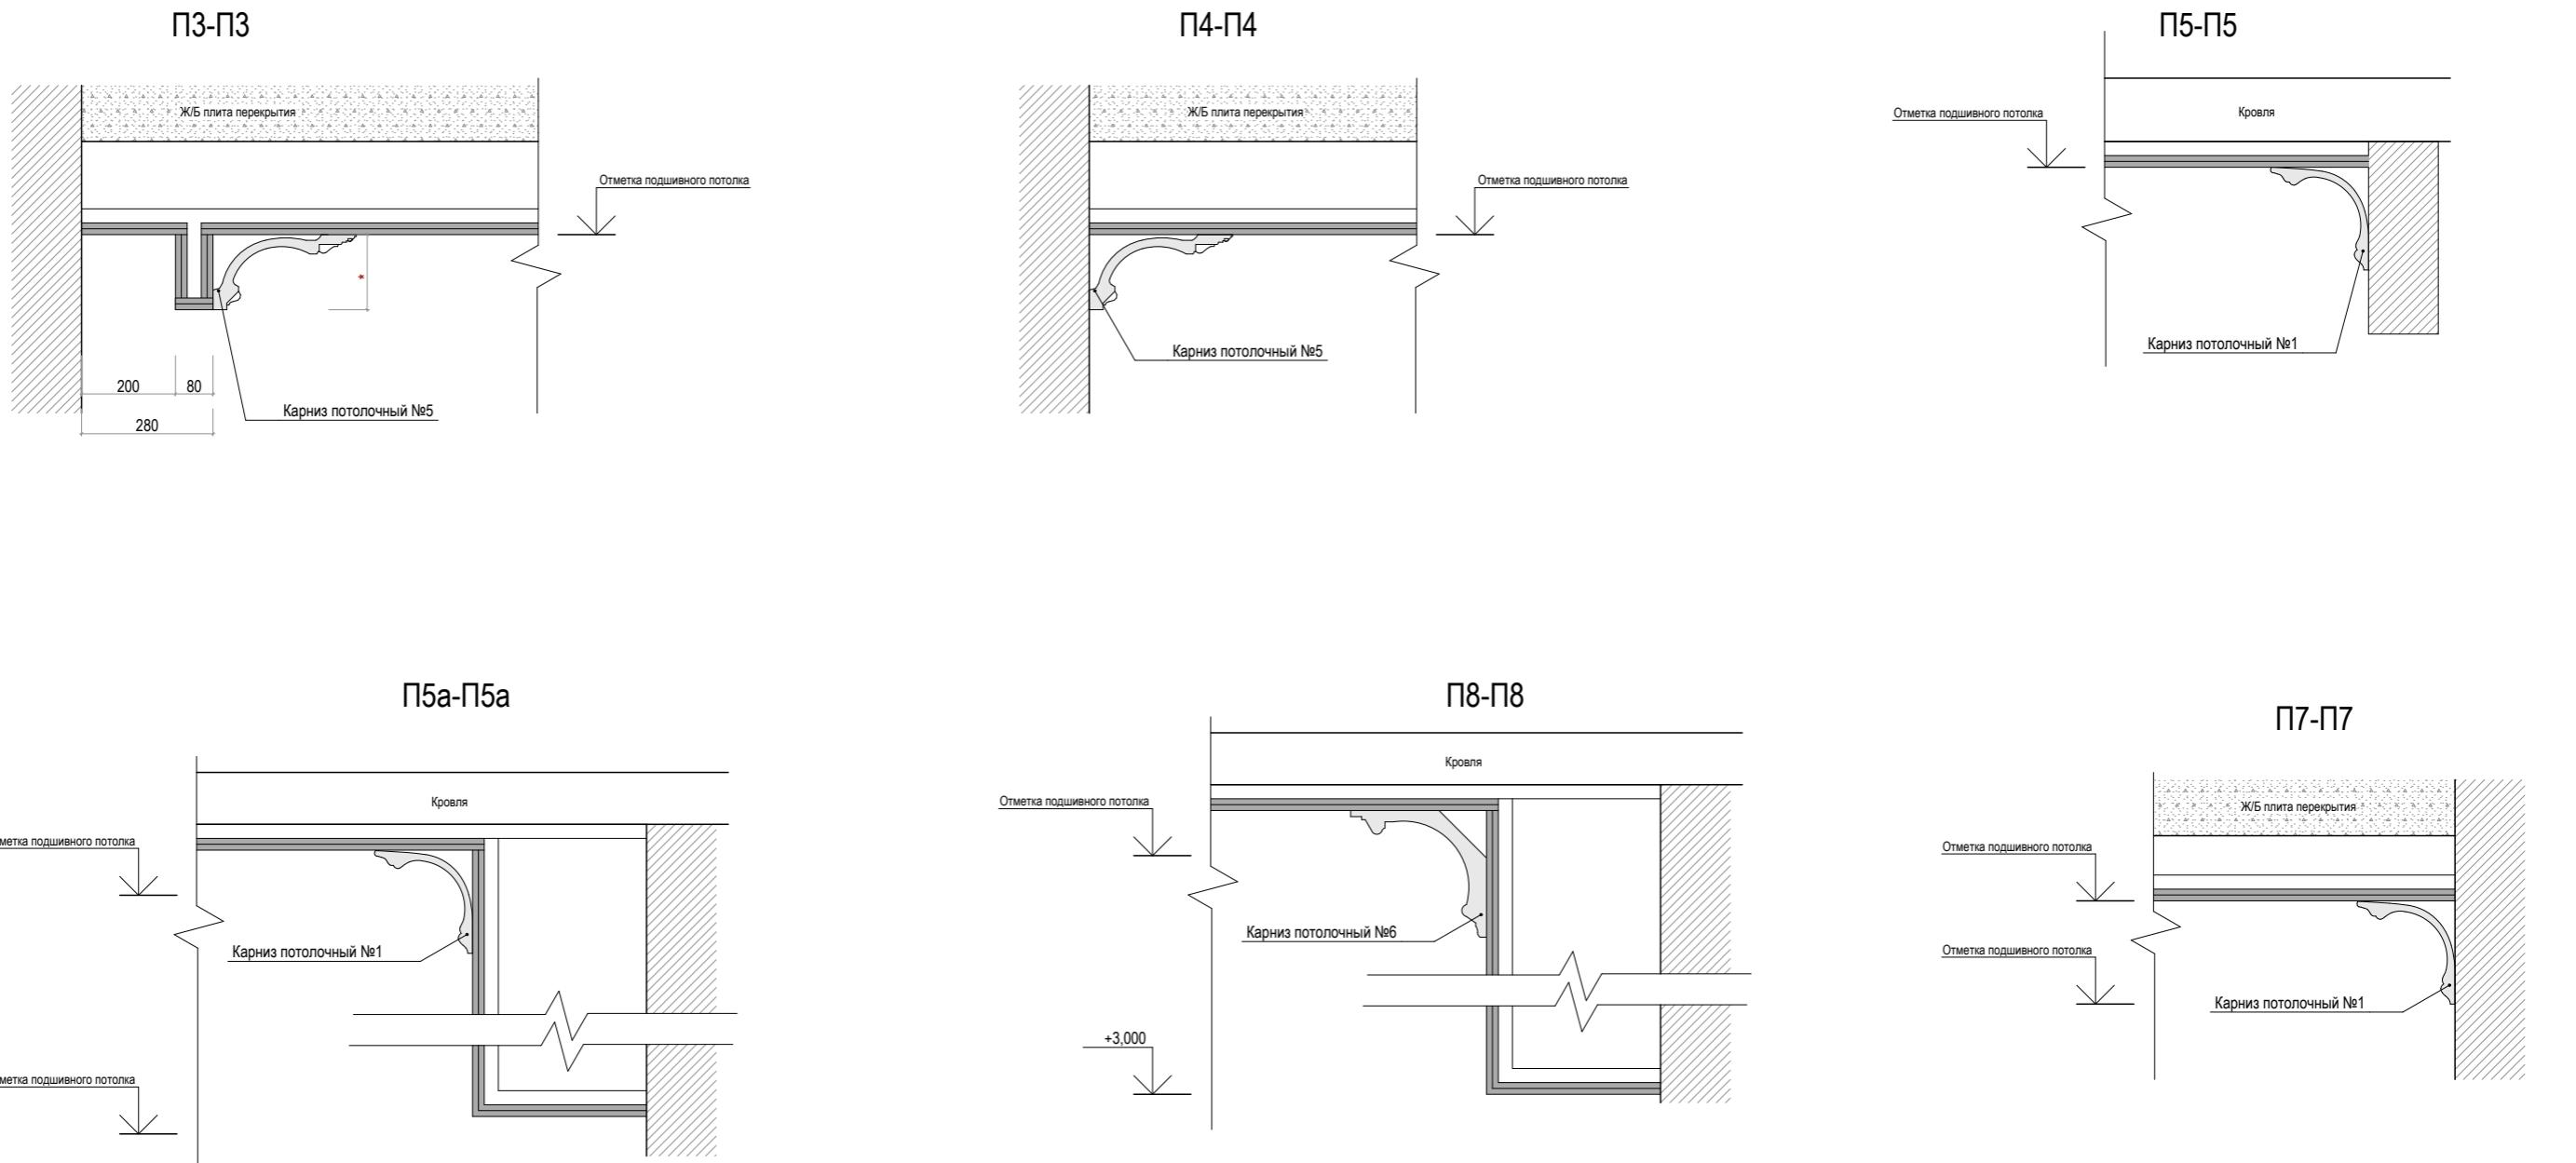

Примечание:

1. Высоты потолков уточняются после утвержденного плана кондиционирования и вентиляции.
2. См. совместно с листом №30
3. Размеры * - уточнить после утверждения карнизов.

Сечение потолков 2го этажа.	Mасштаб	Лист	Листов
	1:15, 00	31	46

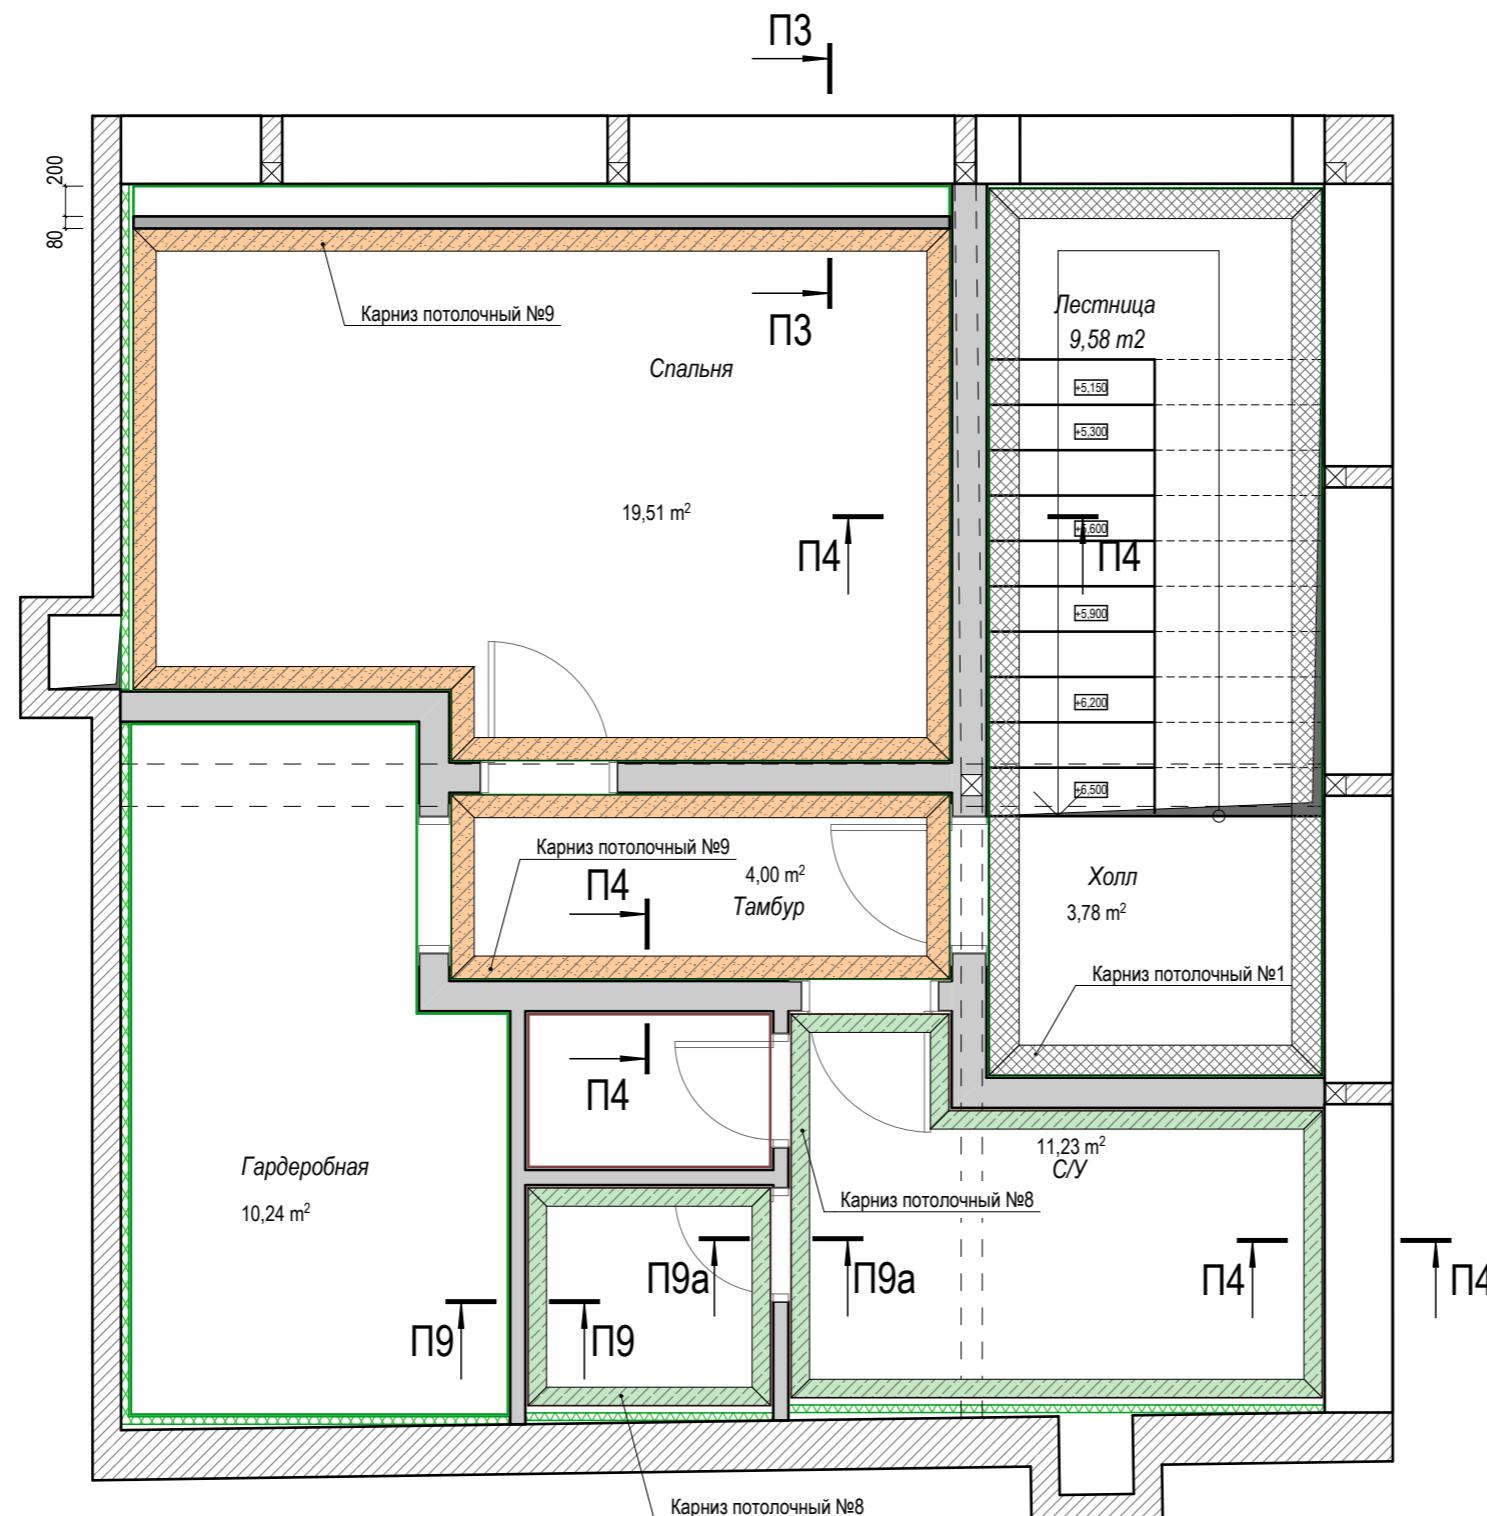

Условные обозначения:


	Покраска
	Покраска

Примечание:


- Высоты потолков уточняются после утвержденного плана кондиционирования и вентиляции.
- Размеры со * уточняются после получения тех. карт от изготовителя кухонной мебели.
- Размеры с *** уточняются после утверждения камина.
- Цвета красок уточняются дополнительно.
- См. совместно с листом №33

План потолков мансардного этажа.	Масштаб	Лист	Листов
	1:50	32	46


П3-П3

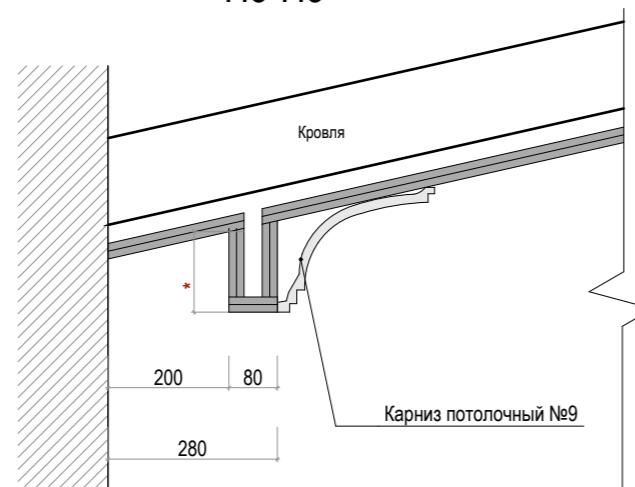


П4-П4

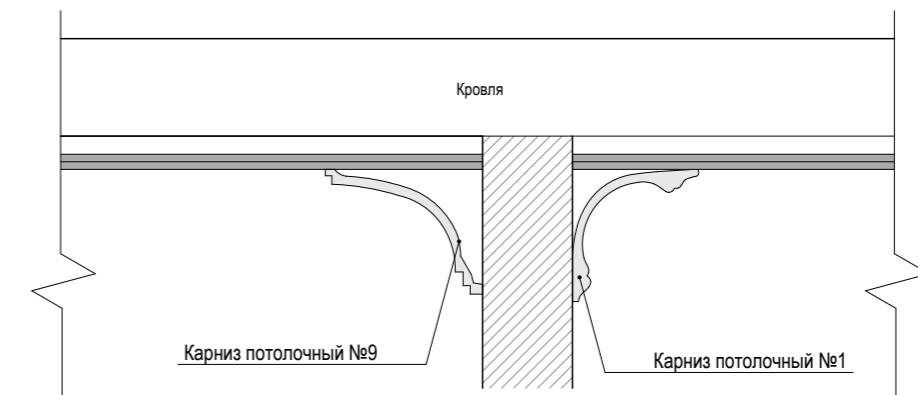

П9-П9

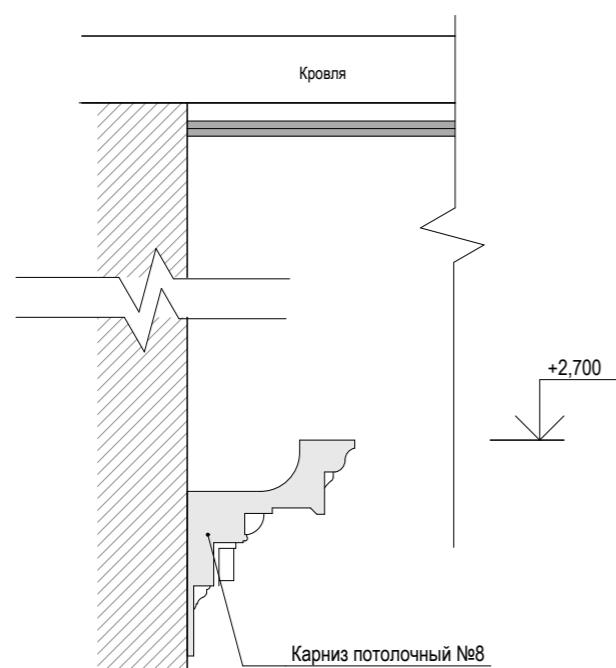

П9а-П9а

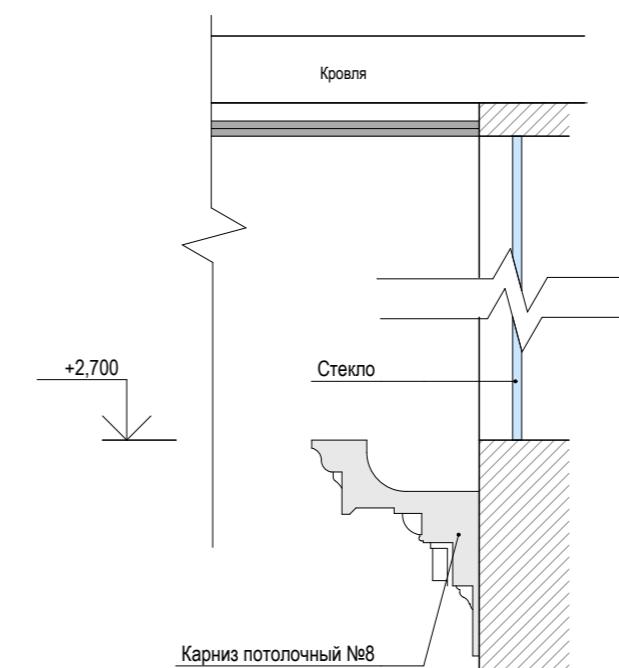


Примечание:

1. Высоты потолков уточняются после утвержденного плана кондиционирования и вентиляции.
2. См. совместно с листом №32
3. Размеры * - уточнить после утверждения карнизов.

Сечение потолков мансардного этажа.	Масштаб	Лист	Листов
	1:12, 50	33	46

Условные обозначения:


- (Светильник точечный потолочный накладной)
- (Светильник точечный потолочный влагостойкий накладной)
- (Светильник точечный потолочный включение от открывания дверок)
- Эл. вывод для бра H=1800мм от уровня чистого пола если не указано отдельно на чертеже

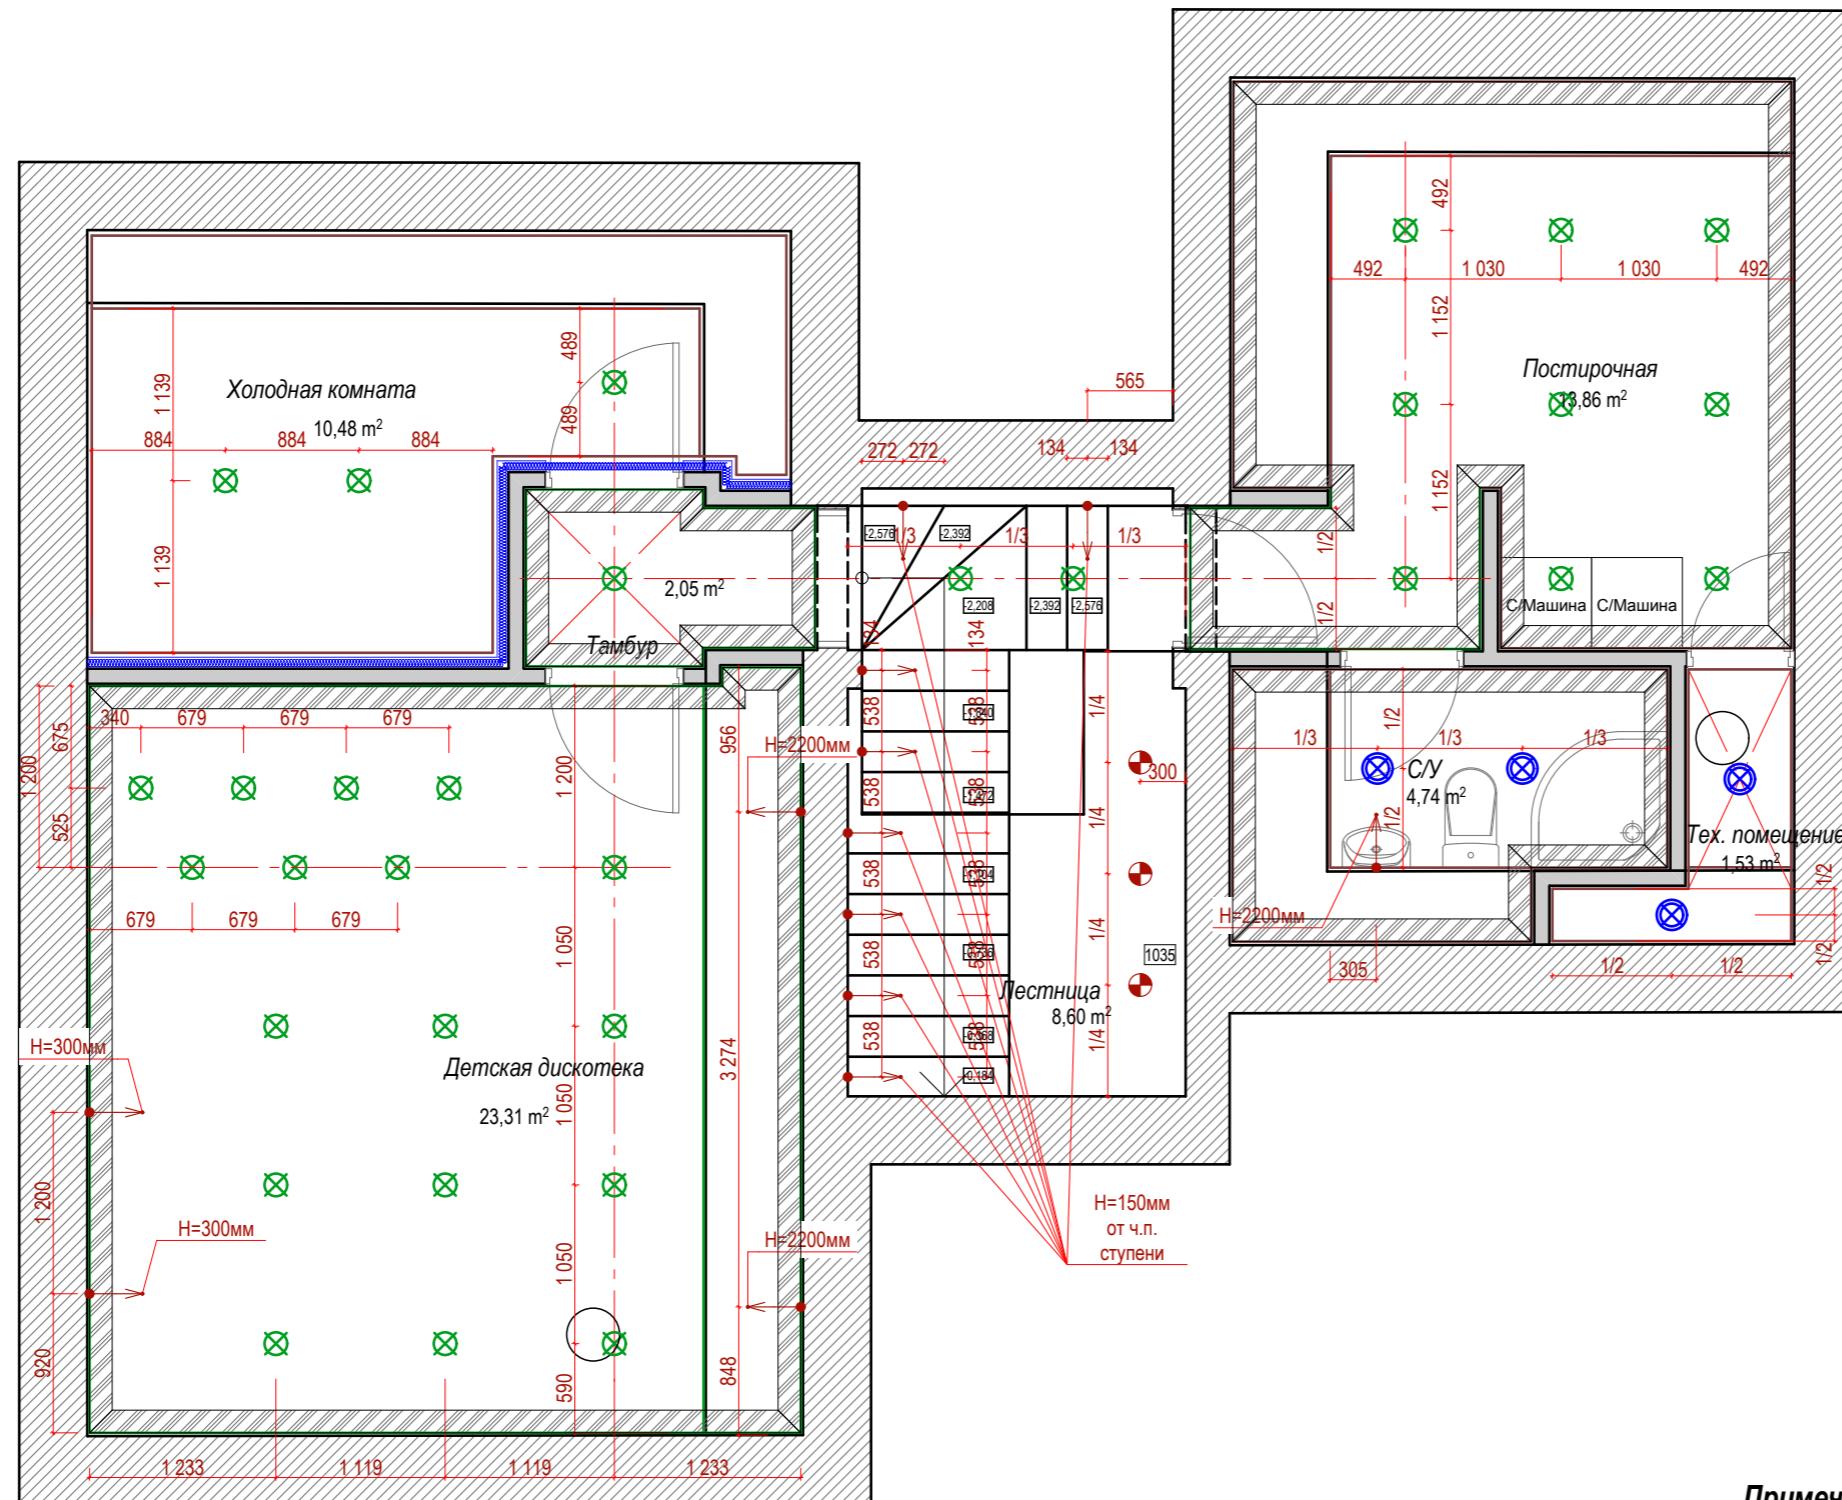

Примечание:

1. Окончательное количество потолочных светильников и точные привязки могут быть скорректированы после выбора конкретных моделей определённой мощности.
2. Привязки эл. выводов для подсветки ступеней лестницы уточнить после утверждения лестницы.

Схема размещения светильников цокольного этажа.	Масштаб	Лист	Листов
	1:50	34	46

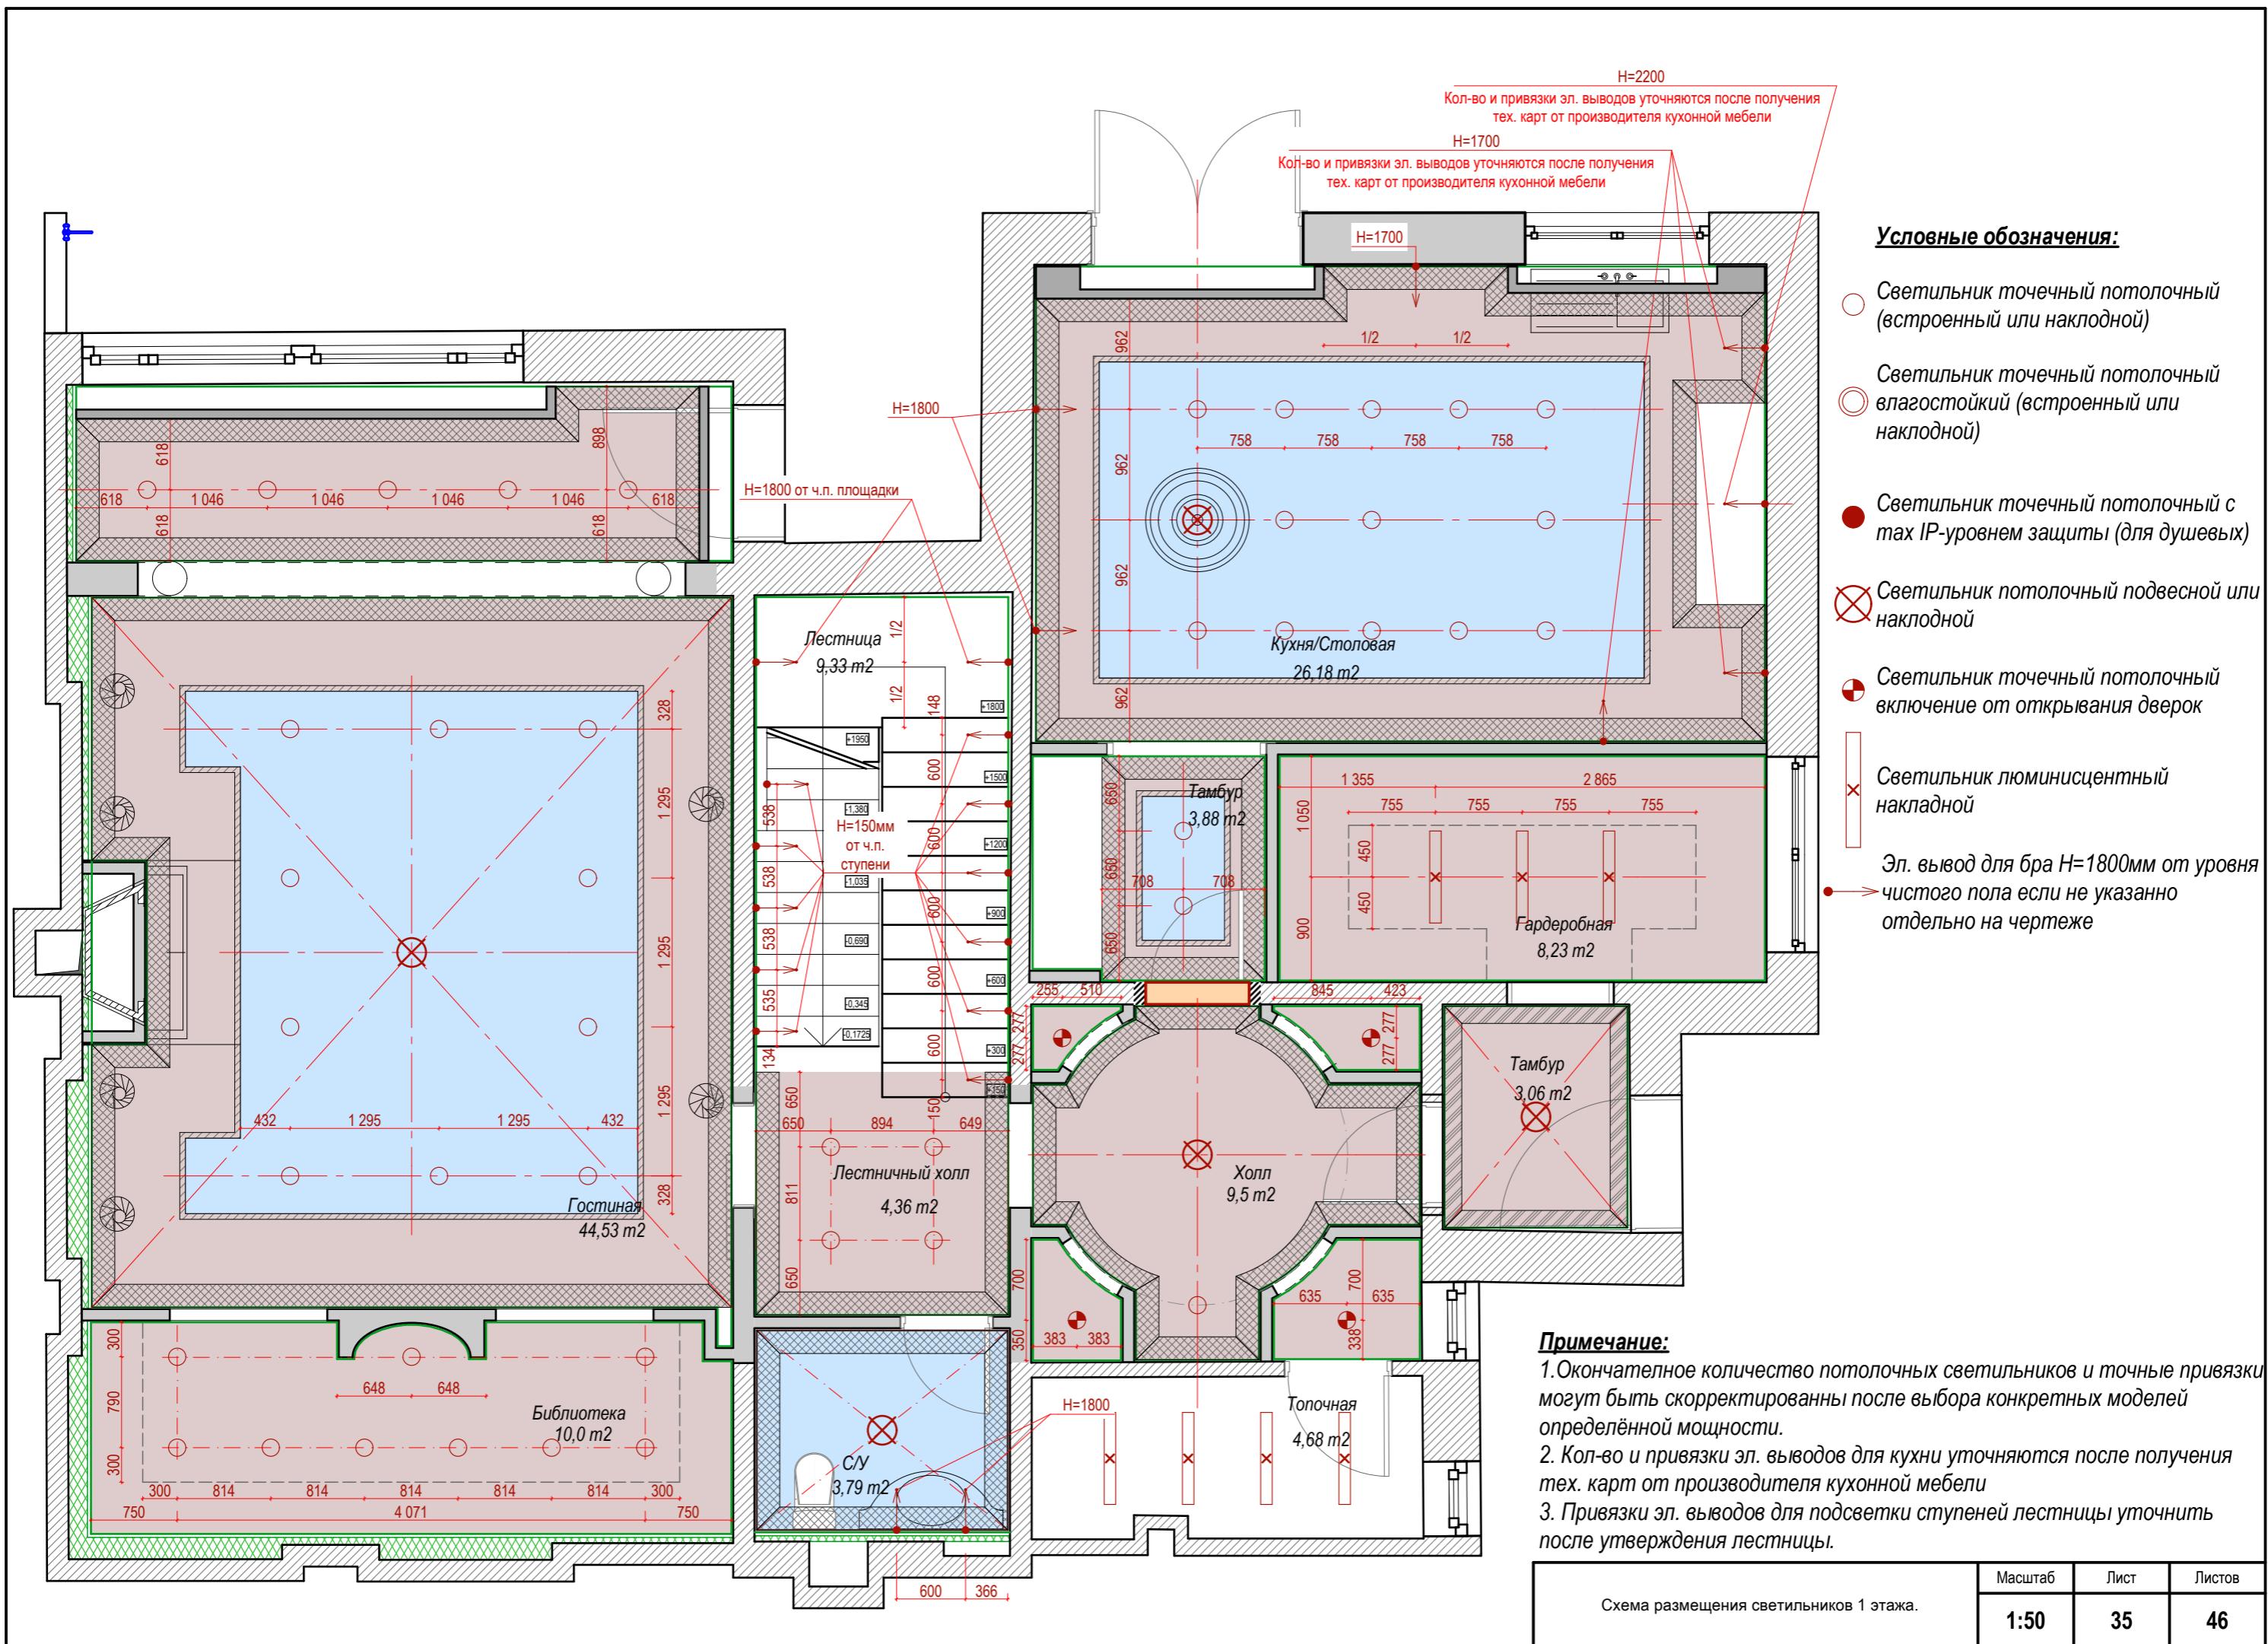


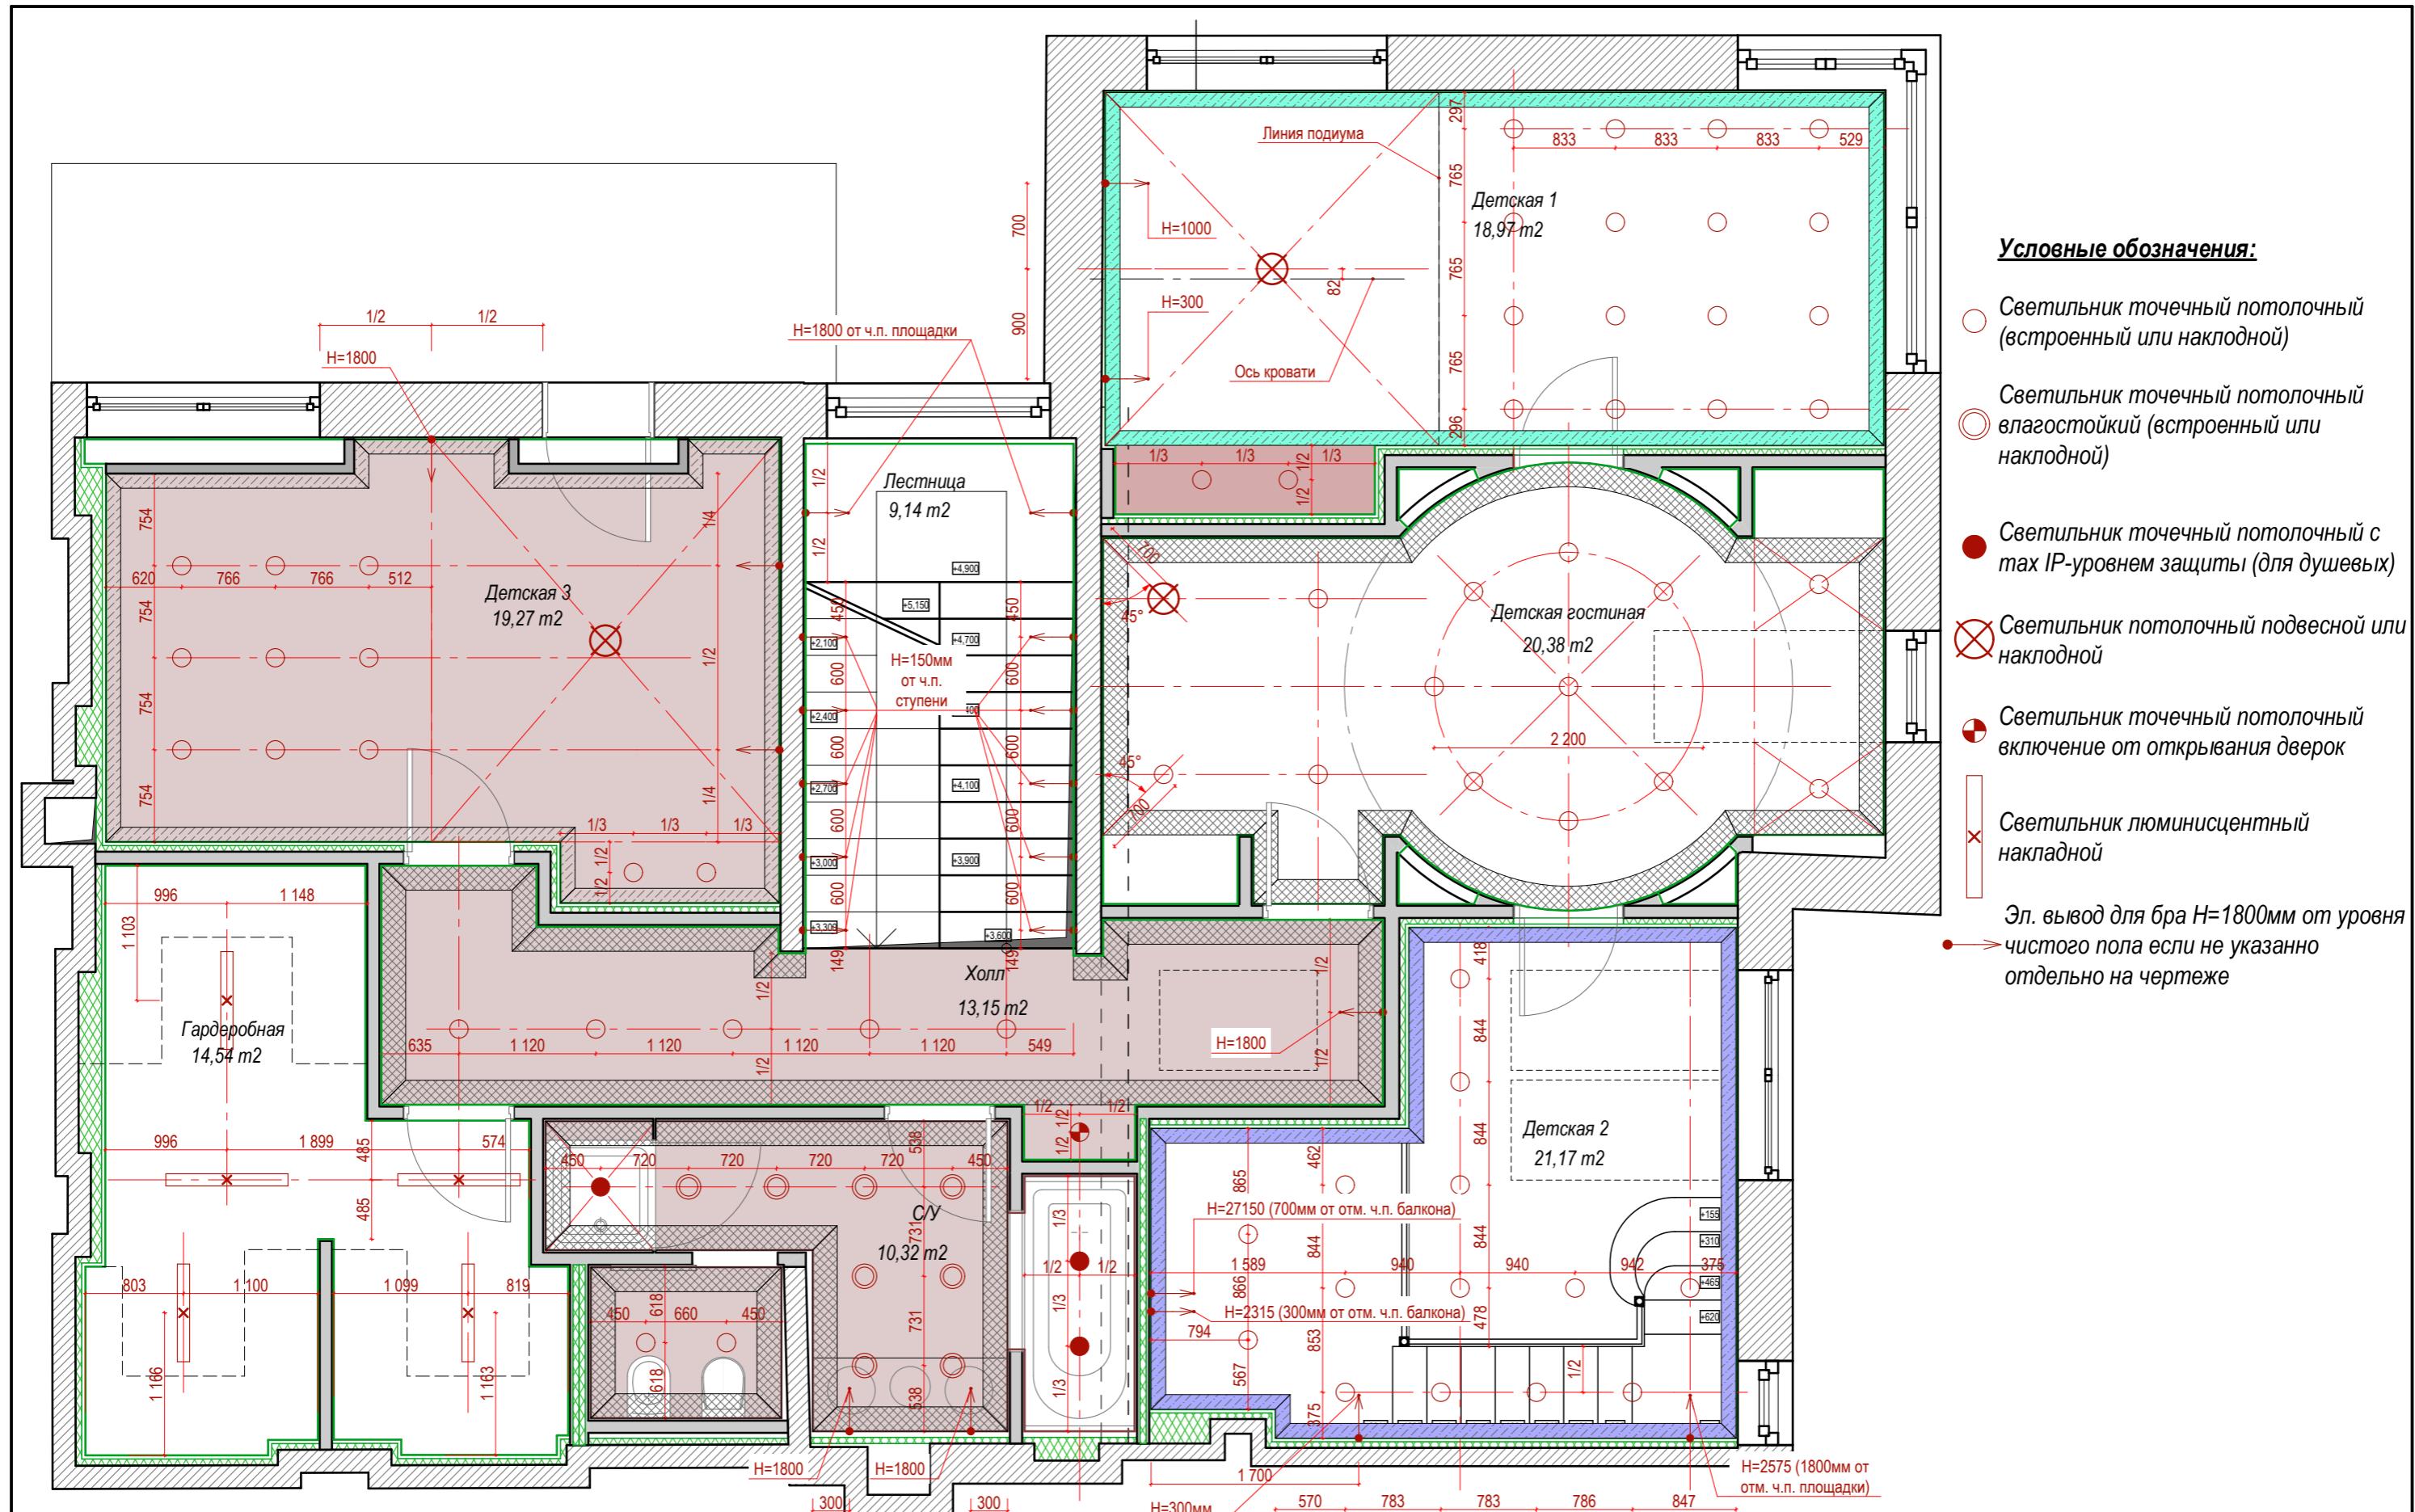


Схема размещения светильников 2 этажа.


Масштаб	Лист	Листов
1:50	36	46

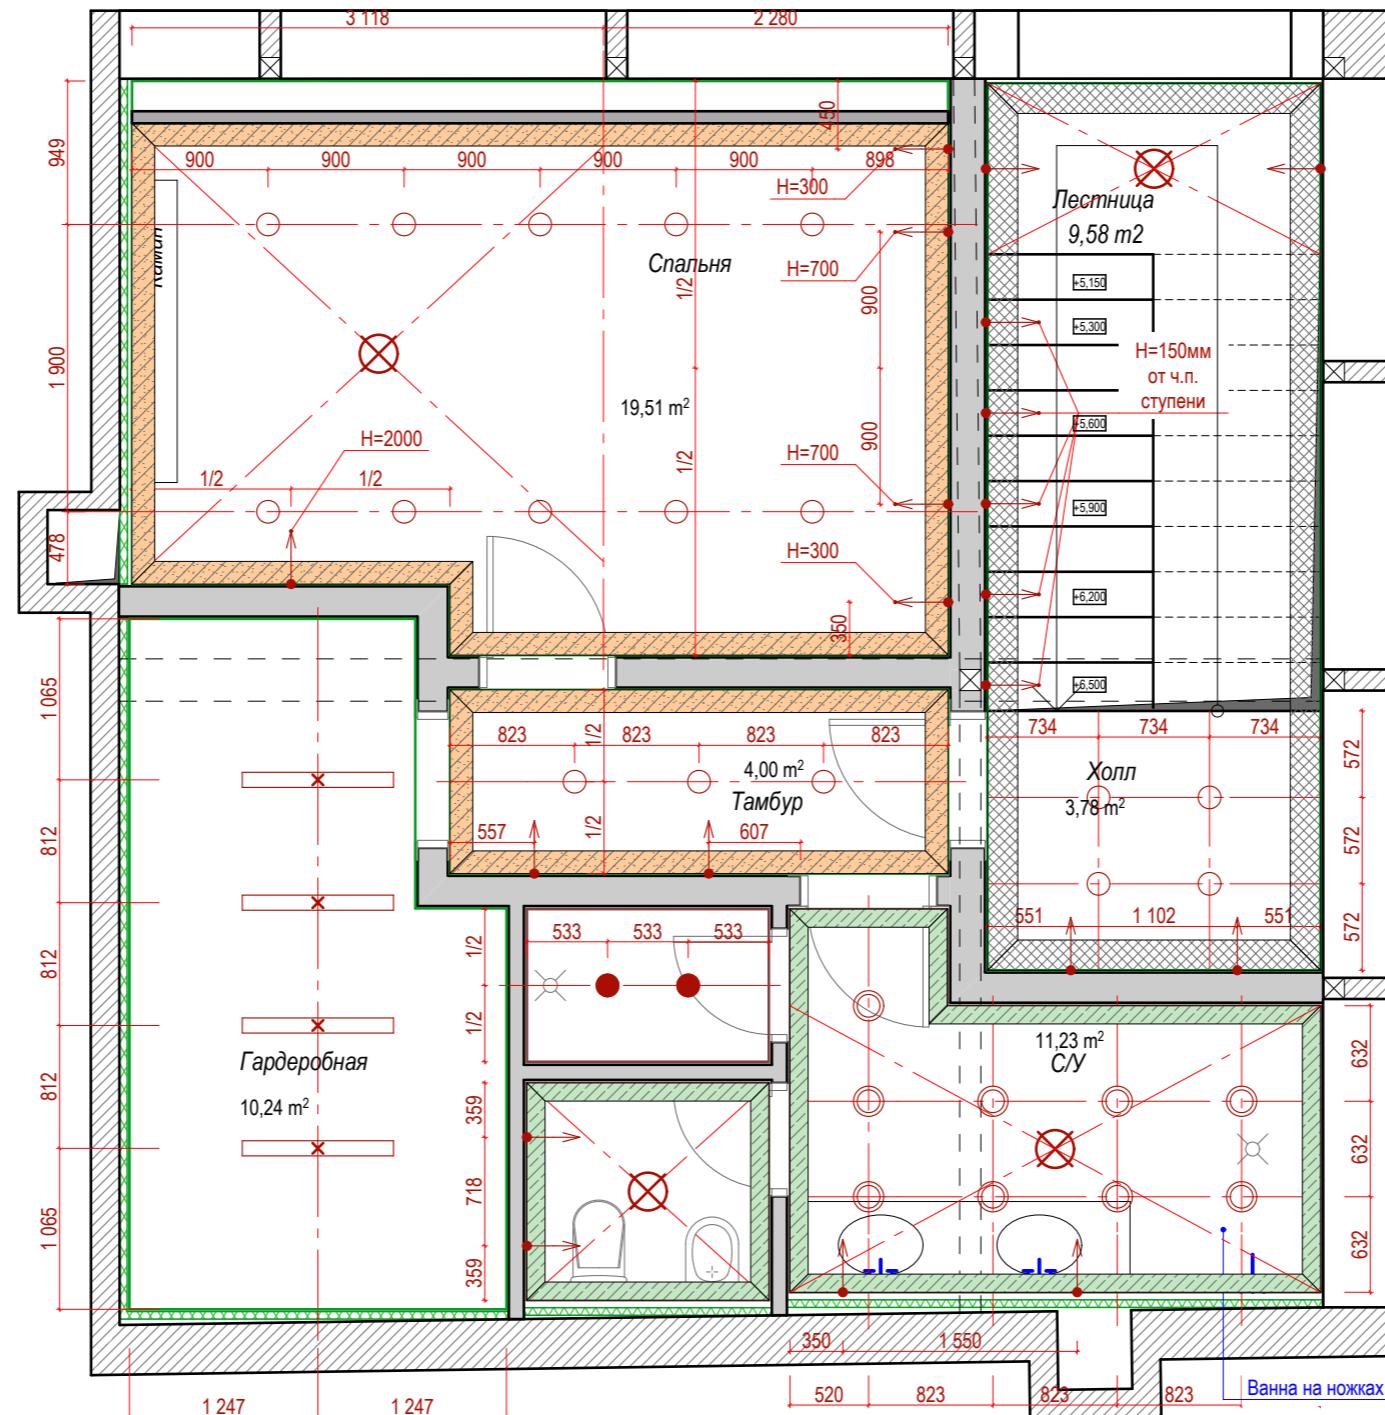

Примечание:

1. Окончательное количество потолочных светильников и точные привязки могут быть скорректированы после выбора конкретных моделей определённой мощности.
2. Привязки эл. выводов для подсветки ступеней лестницы уточнить после утверждения лестницы.

Схема размещения светильников мансардного этажа.	Масштаб	Лист	Листов
	1:50	37	46

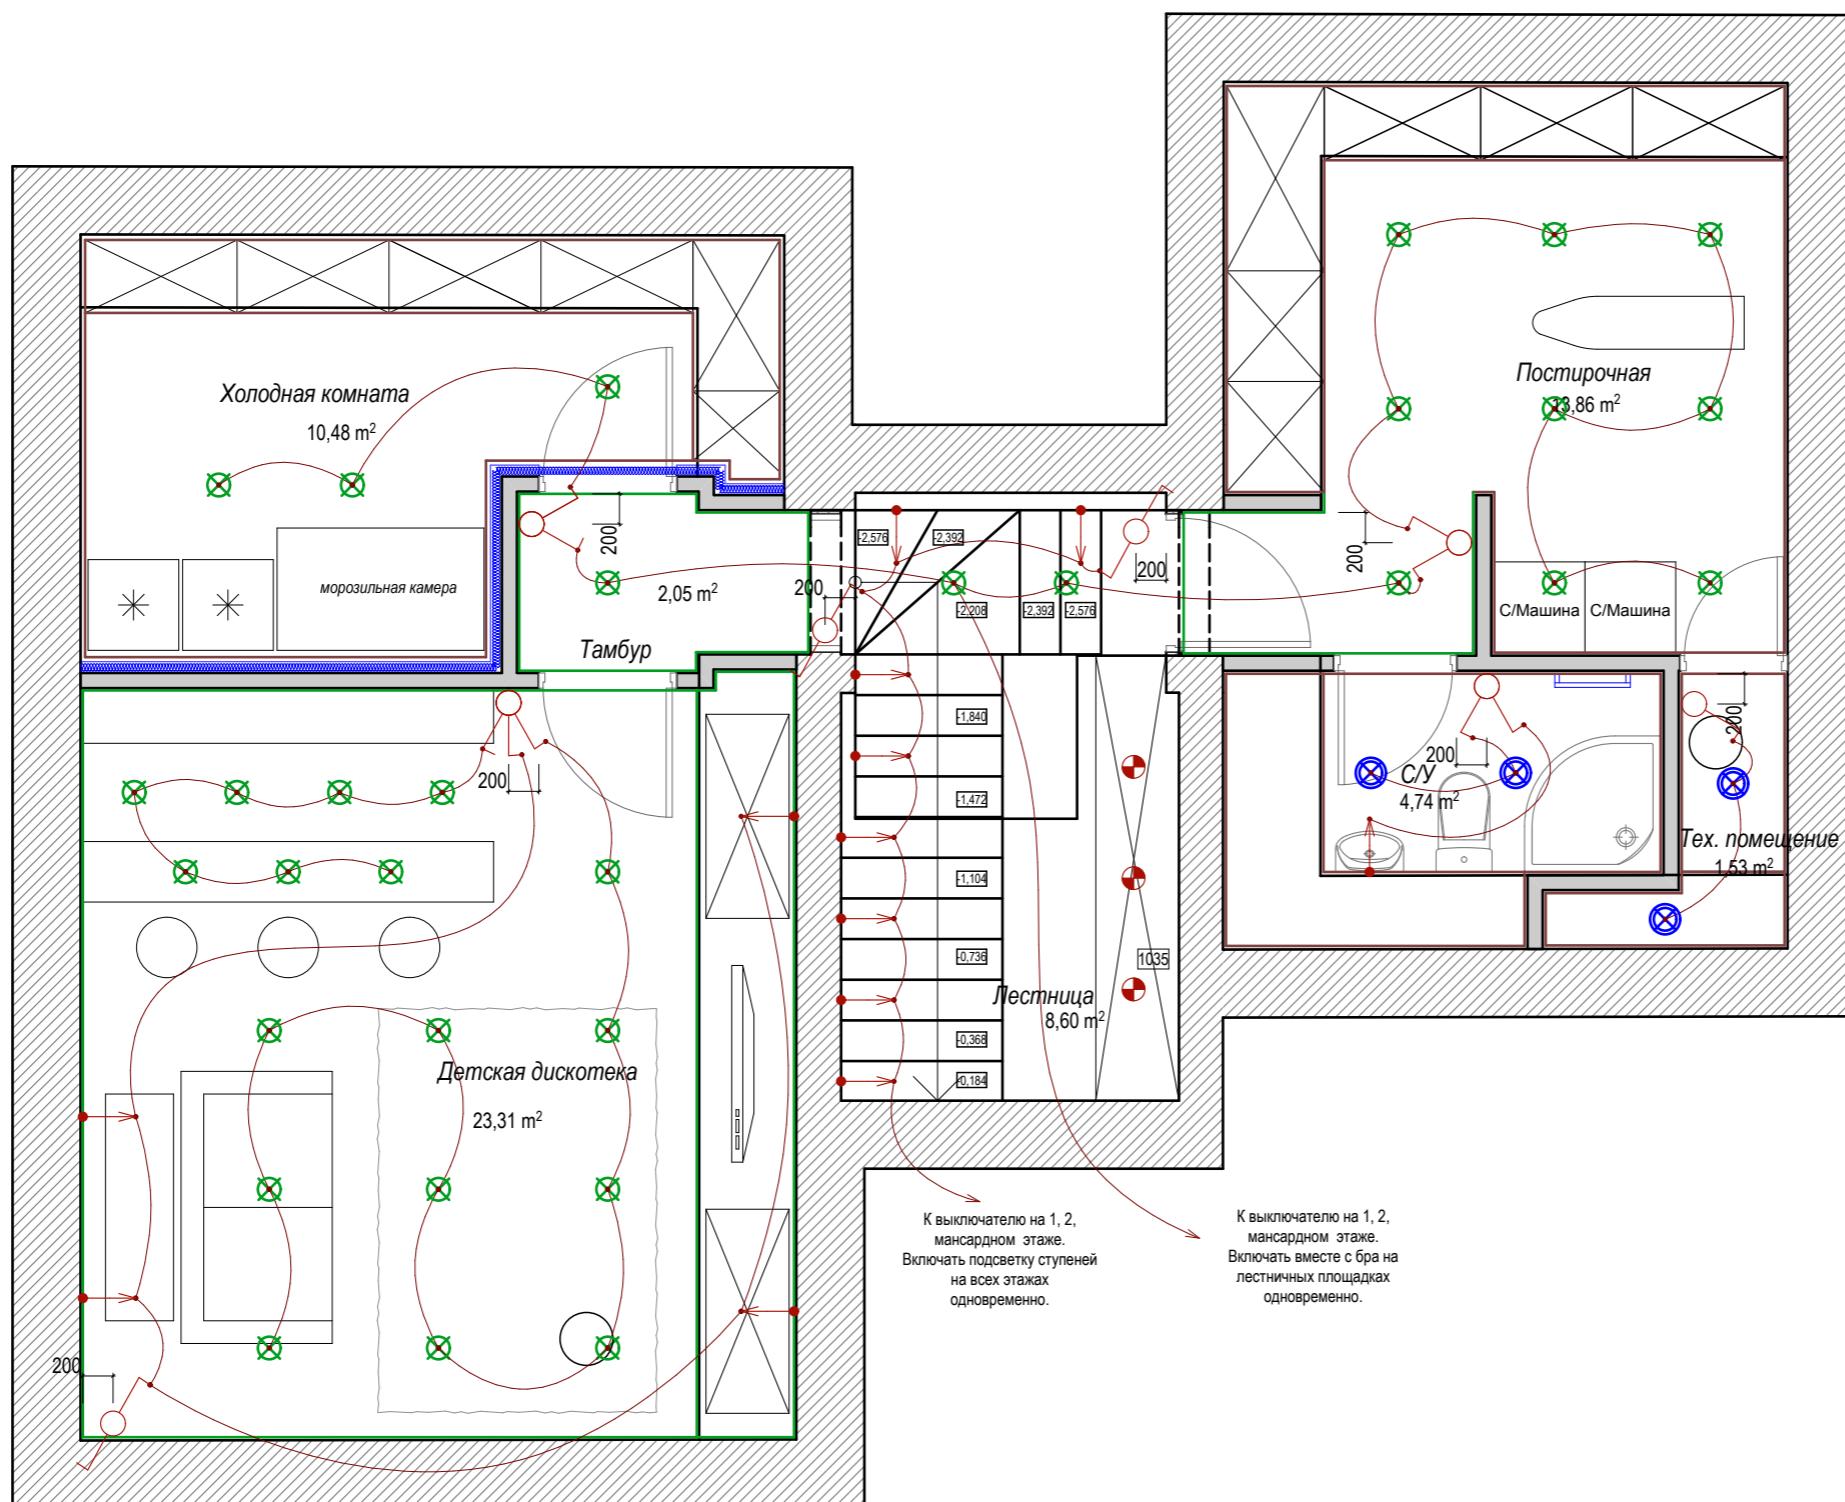


Условные обозначения:

- ✖ Светильник точечный потолочный накладной
- ✖ Светильник точечный потолочный влагостойкий накладной
- ✖ Светильник точечный потолочный включение от открывания дверок
- Эл. вывод для бра H=1800мм от уровня чистого пола если не указано отдельно на чертеже
- Выкл. одноклавишный
- Выкл. двухклавишный
- Выкл. трёхклавишный
- Выкл. одноклавишный проходной
- Выкл. двухклавишный проходной
- Выкл. трёхклавишный проходной

Примечание:

1. Выключатели устанавливать на высоте 900мм от уровня чистого пола.
2. Выключатели устанавливать на расстоянии 200мм от края проёма или угла стены если нет специальных отмечек на чертеже.

Условные обозначения:

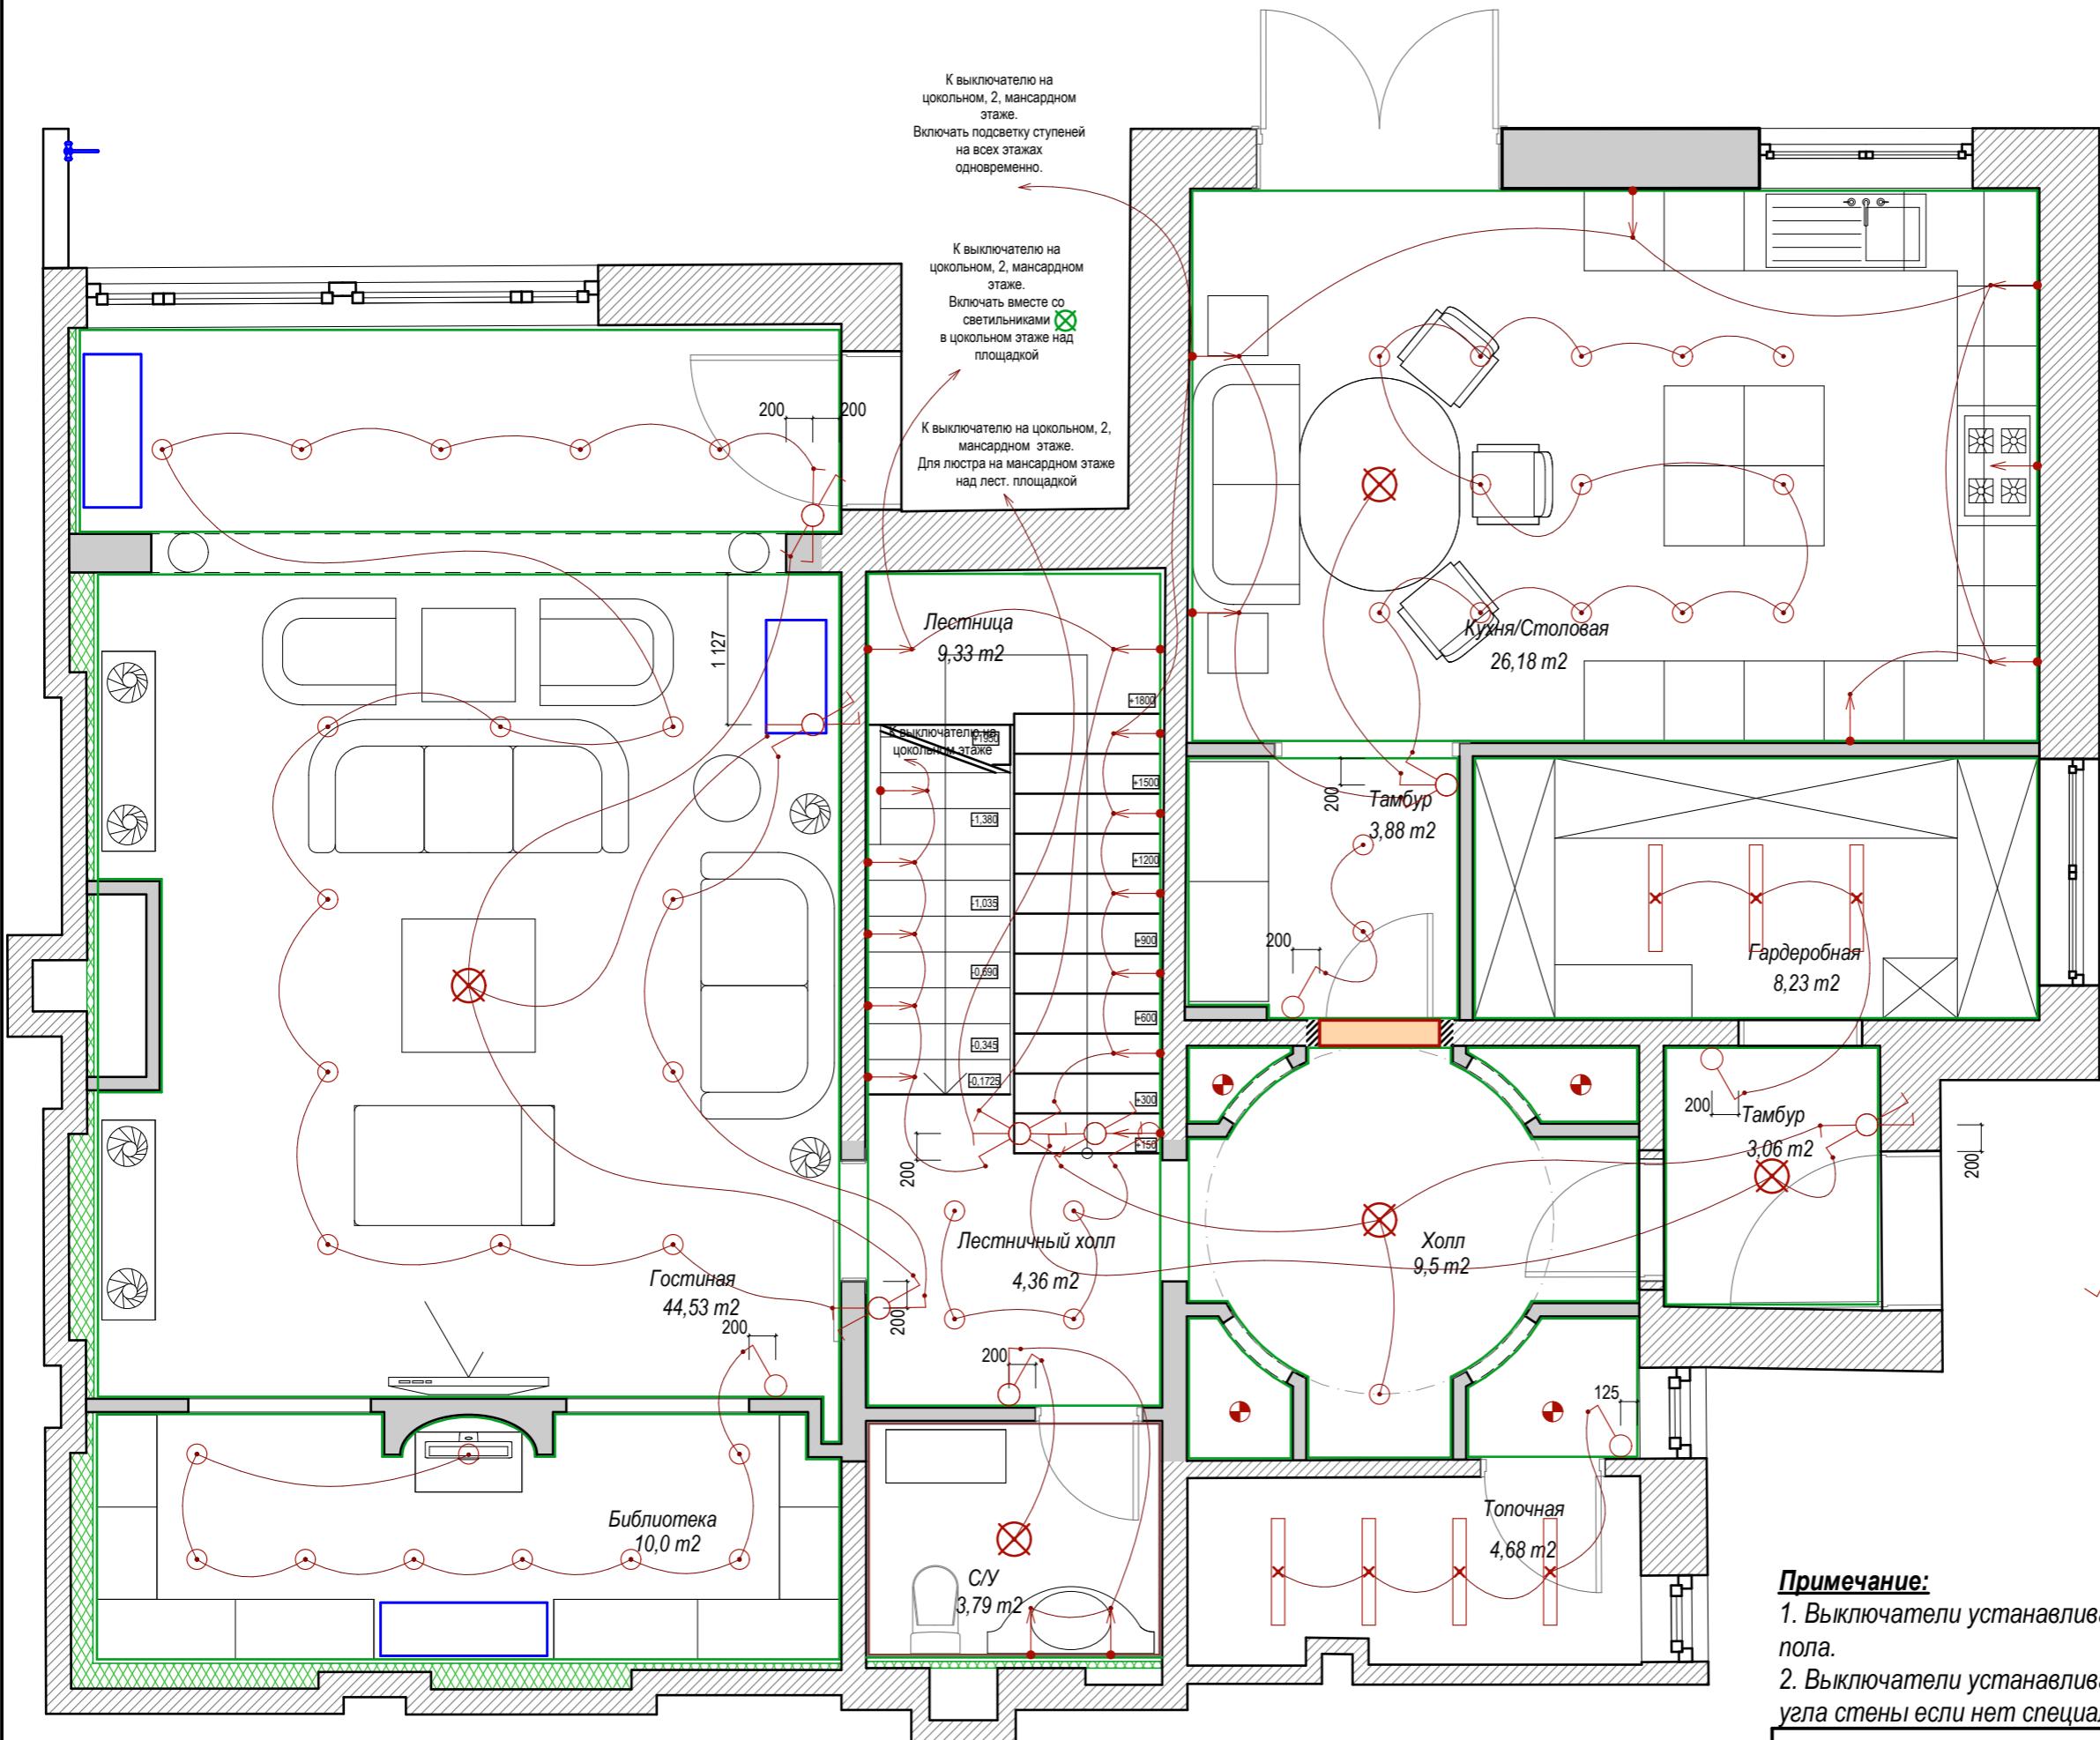

- Светильник точечный потолочный (встроенный или накладной)
 - Светильник точечный потолочный влагостойкий (встроенный или накладной)
 - Светильник точечный потолочный с max IP-уровнем защиты (для душевых)
 - ✖ Светильник потолочный подвесной или накладной
 - Светильник точечный потолочный включение от открывания дверок
 - ✖ Светильник люминисцентный накладной
 - → Эл. вывод для бра H=1800мм от уровня чистого пола если не указано отдельно на чертеже
 -  Выкл. одноклавишный
 -  Выкл. двухклавишный
 -  Выкл. трёхклавишный
 -  Выкл. одноклавишный проходной
 -  Выкл. двухклавишный проходной
 -  Выкл. трёхклавишный проходной

Примечание:


1. Выключатели устанавливать на высоте 900мм от уровня чистого пола.
 2. Выключатели устанавливать на расстоянии 200мм от края проёма или угла стены если нет специальных отметок на чертеже.

Схема размещения выключателей с привязкой к светильникам 1го этажа.

Масштаб	Лист	Листов
1:50	39	46

Условные обозначения:

- (○) Светильник точечный потолочный (встроенный или накладной)
- (○) Светильник точечный потолочный влагостойкий (встроенный или накладной)
- (●) Светильник точечный потолочный с max IP-уровнем защиты (для душевых)
- (✗) Светильник потолочный подвесной или накладной
- (●) Светильник точечный потолочный включение от открывания дверок
- (—) Светильник люминесцентный накладной
- Эл. вывод для бра H=1800мм от уровня чистого пола если не указано отдельно на чертеже
- (○) Выкл. одноклавишный
- (○) Выкл. двухклавишный
- (○) Выкл. трёхклавишный
- (○) Выкл. одноклавишный проходной
- (○) Выкл. двухклавишный проходной
- (○) Выкл. трёхклавишный проходной

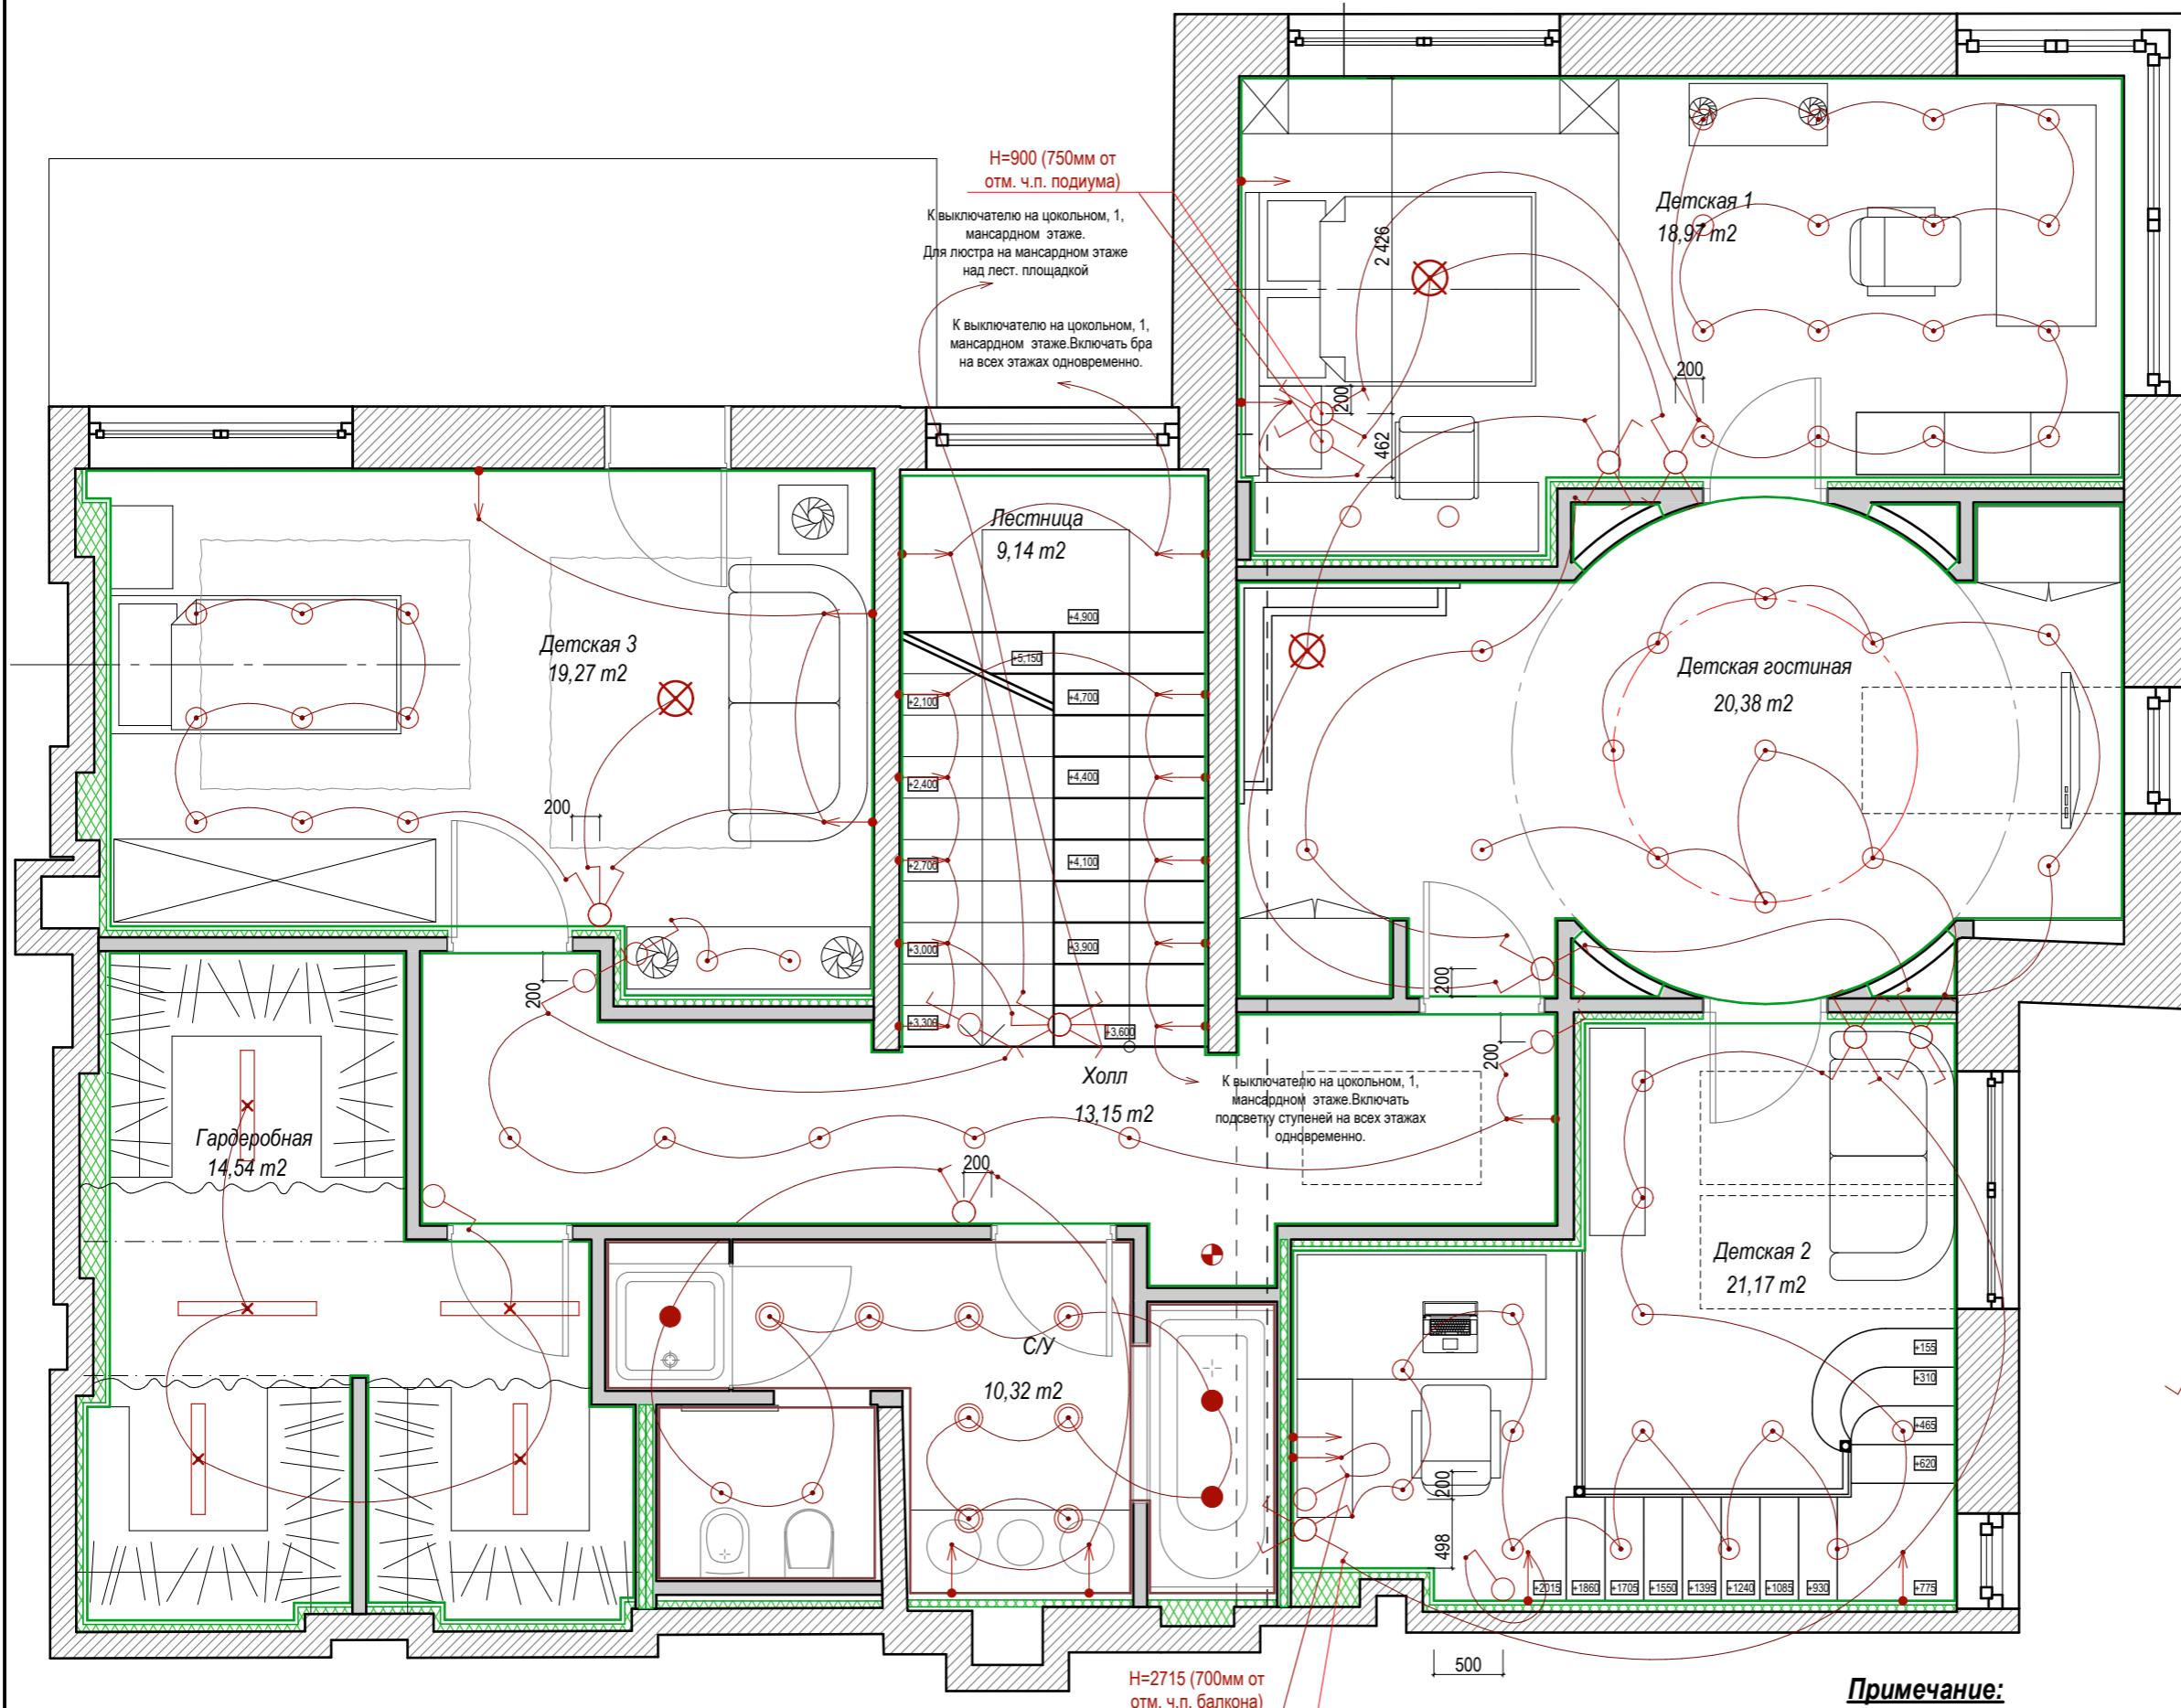


Примечание:

- Выключатели устанавливать на высоте 900мм от уровня чистого пола.
- Выключатели устанавливать на расстоянии 200мм от края проёма или угла стены если нет специальных отметок на чертеже.

Схема размещения выключателей с привязкой к светильникам 2го этажа.

Масштаб	Лист	Листов
1:50	40	46

Условные обозначения:

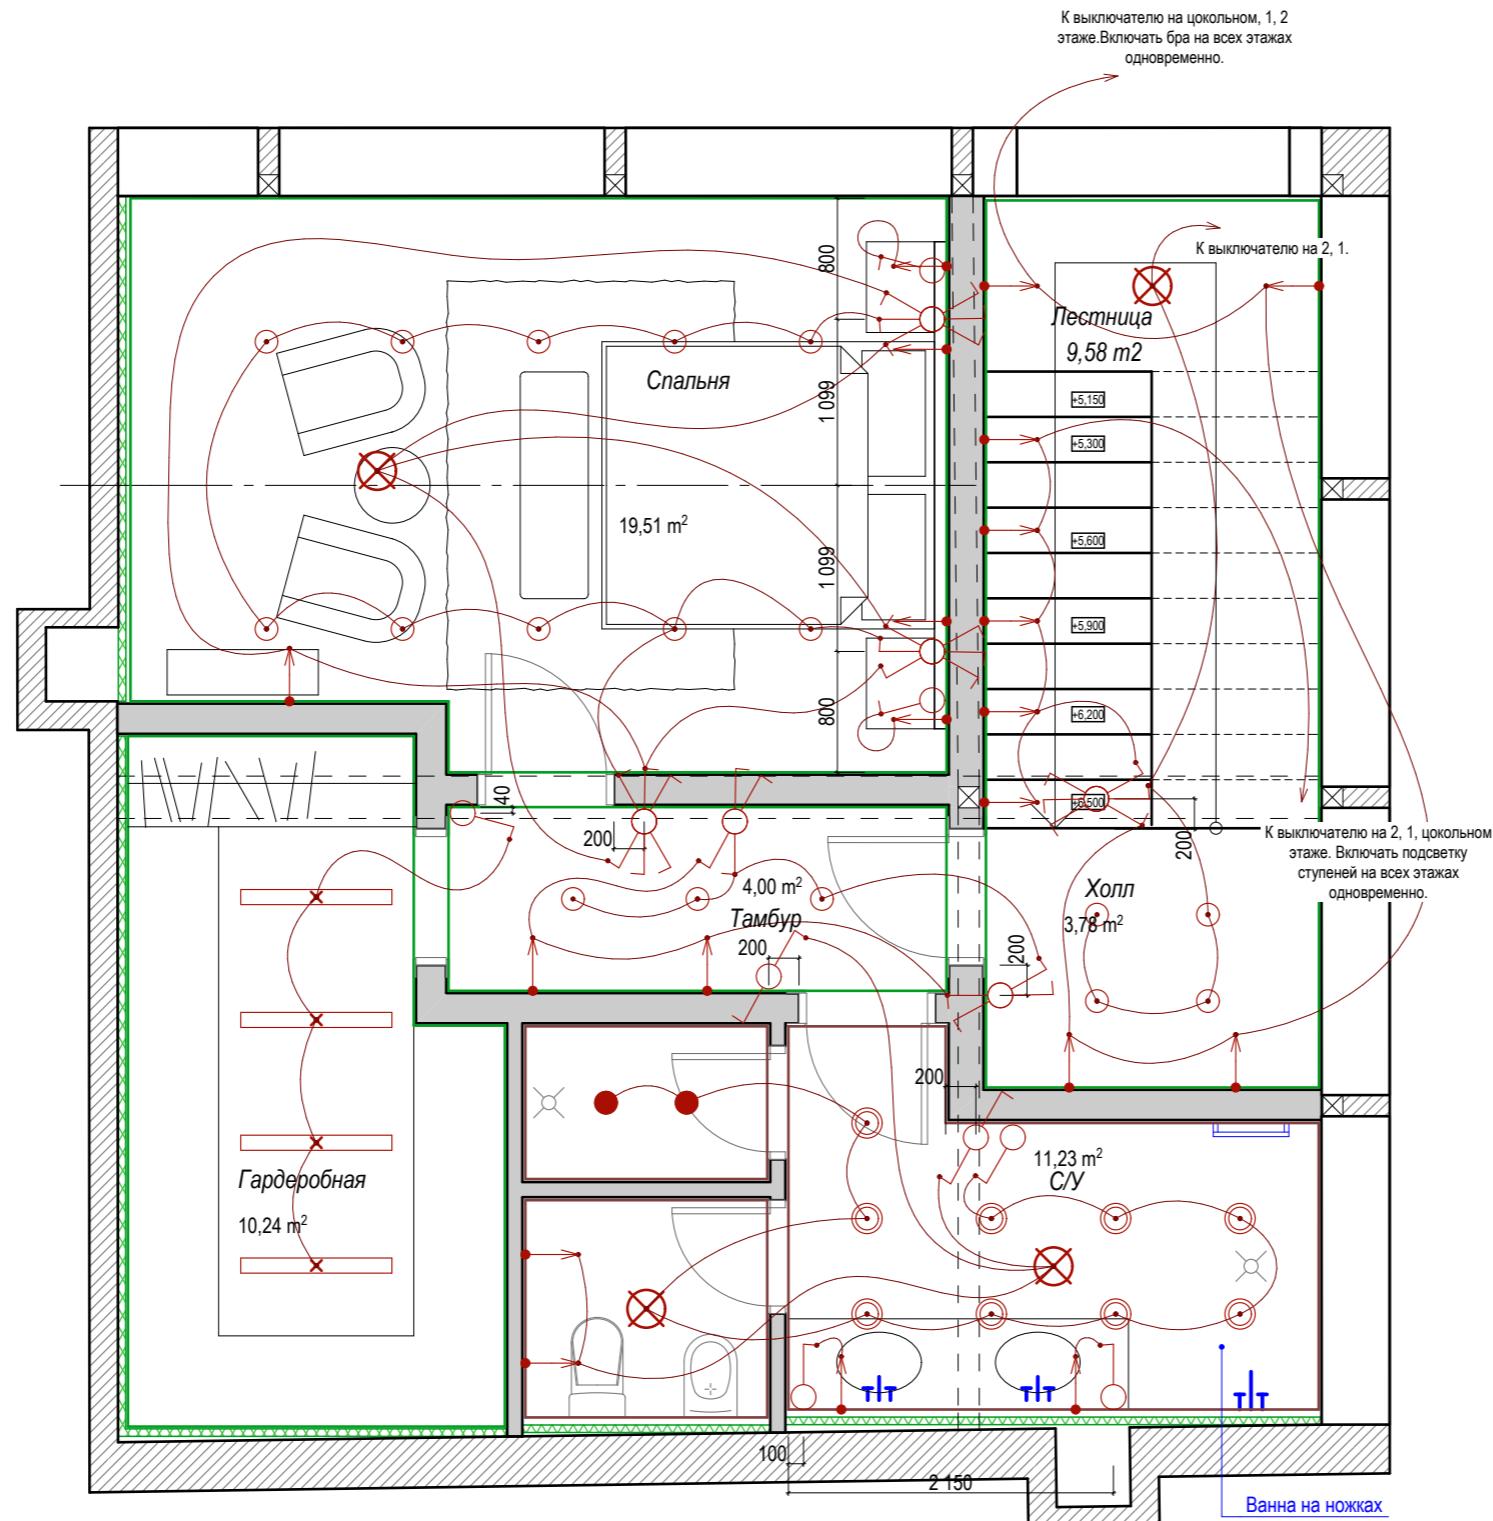

- Светильник точечный потолочный (встроенный или накладной)
- Светильник точечный потолочный влагостойкий (встроенный или накладной)
- Светильник точечный потолочный с max IP-уровнем защиты (для душевых)
- ✖ Светильник потолочный подвесной или накладной
- Светильник точечный потолочный включение от открывания дверок
- ✖ Светильник люминесцентный накладной
- Эл. вывод для бра H=1800мм от уровня чистого пола если не указано отдельно на чертеже
- Выкл. одноклавишный
- Выкл. двухклавишный
- Выкл. трёхклавишный
- Выкл. одноклавишный проходной
- Выкл. двухклавишный проходной
- Выкл. трёхклавишный проходной


Примечание:

1. Выключатели устанавливать на высоте 900мм от уровня чистого пола.
2. Выключатели устанавливать на расстоянии 200мм от края проёма или угла стены если нет специальных отметок на чертеже.

Схема размещения выключателей с привязкой к светильникам мансардного этажа.	Масштаб	Лист	Листов
	1:50	41	46

Условные обозначения:

- Эл. вывод
 - ↗ Розетка 220в
 - ↗ Розетка 220в. Точные привязки будут выданы после выдачи тех.карт производителем кухонной техники.
 - Розетка 220в уличная, накладная.
 - Розетка 220в влагозащищённая.
 - TF Розетка телефонная
 - TV Розетка телевизионная
 - Int Розетка интернет
 - Калонки потолочные

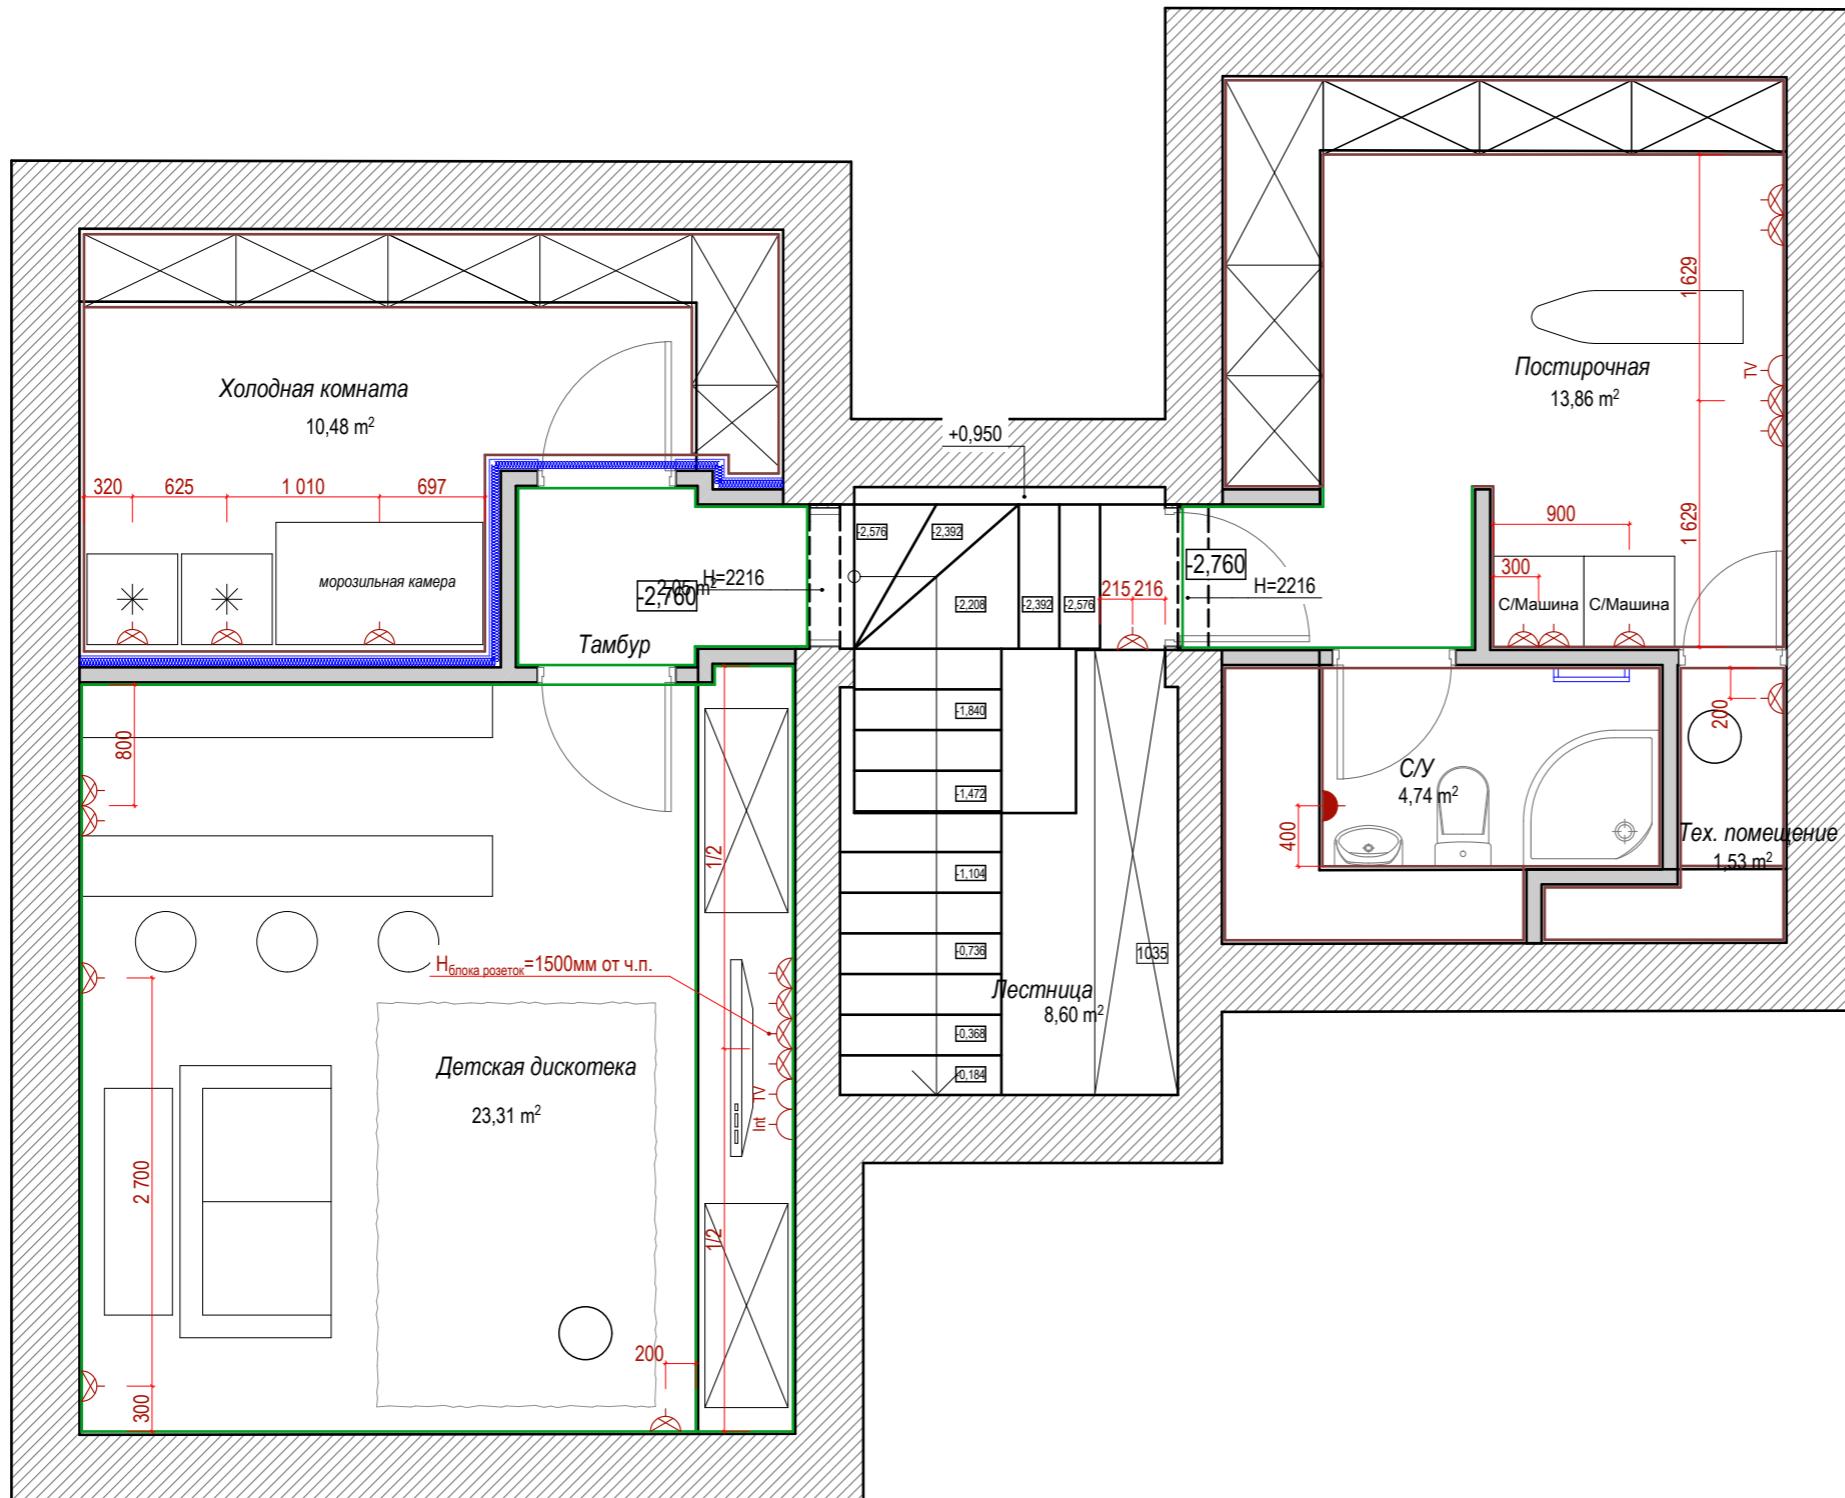


Примечание:

1. Розетки устанавливать на высоте 300мм от уровня чистого пола если нет специальных отметок на чертеже.
 2. Выключатели устанавливать на расстоянии 200мм от края проёма или угла стены если нет специальных отметок на чертеже.

	Масштаб	Лист	Листов
Схема размещения розеток и эл. выводов цокольного этажа.	1:50	42	46

Условные обозначения:

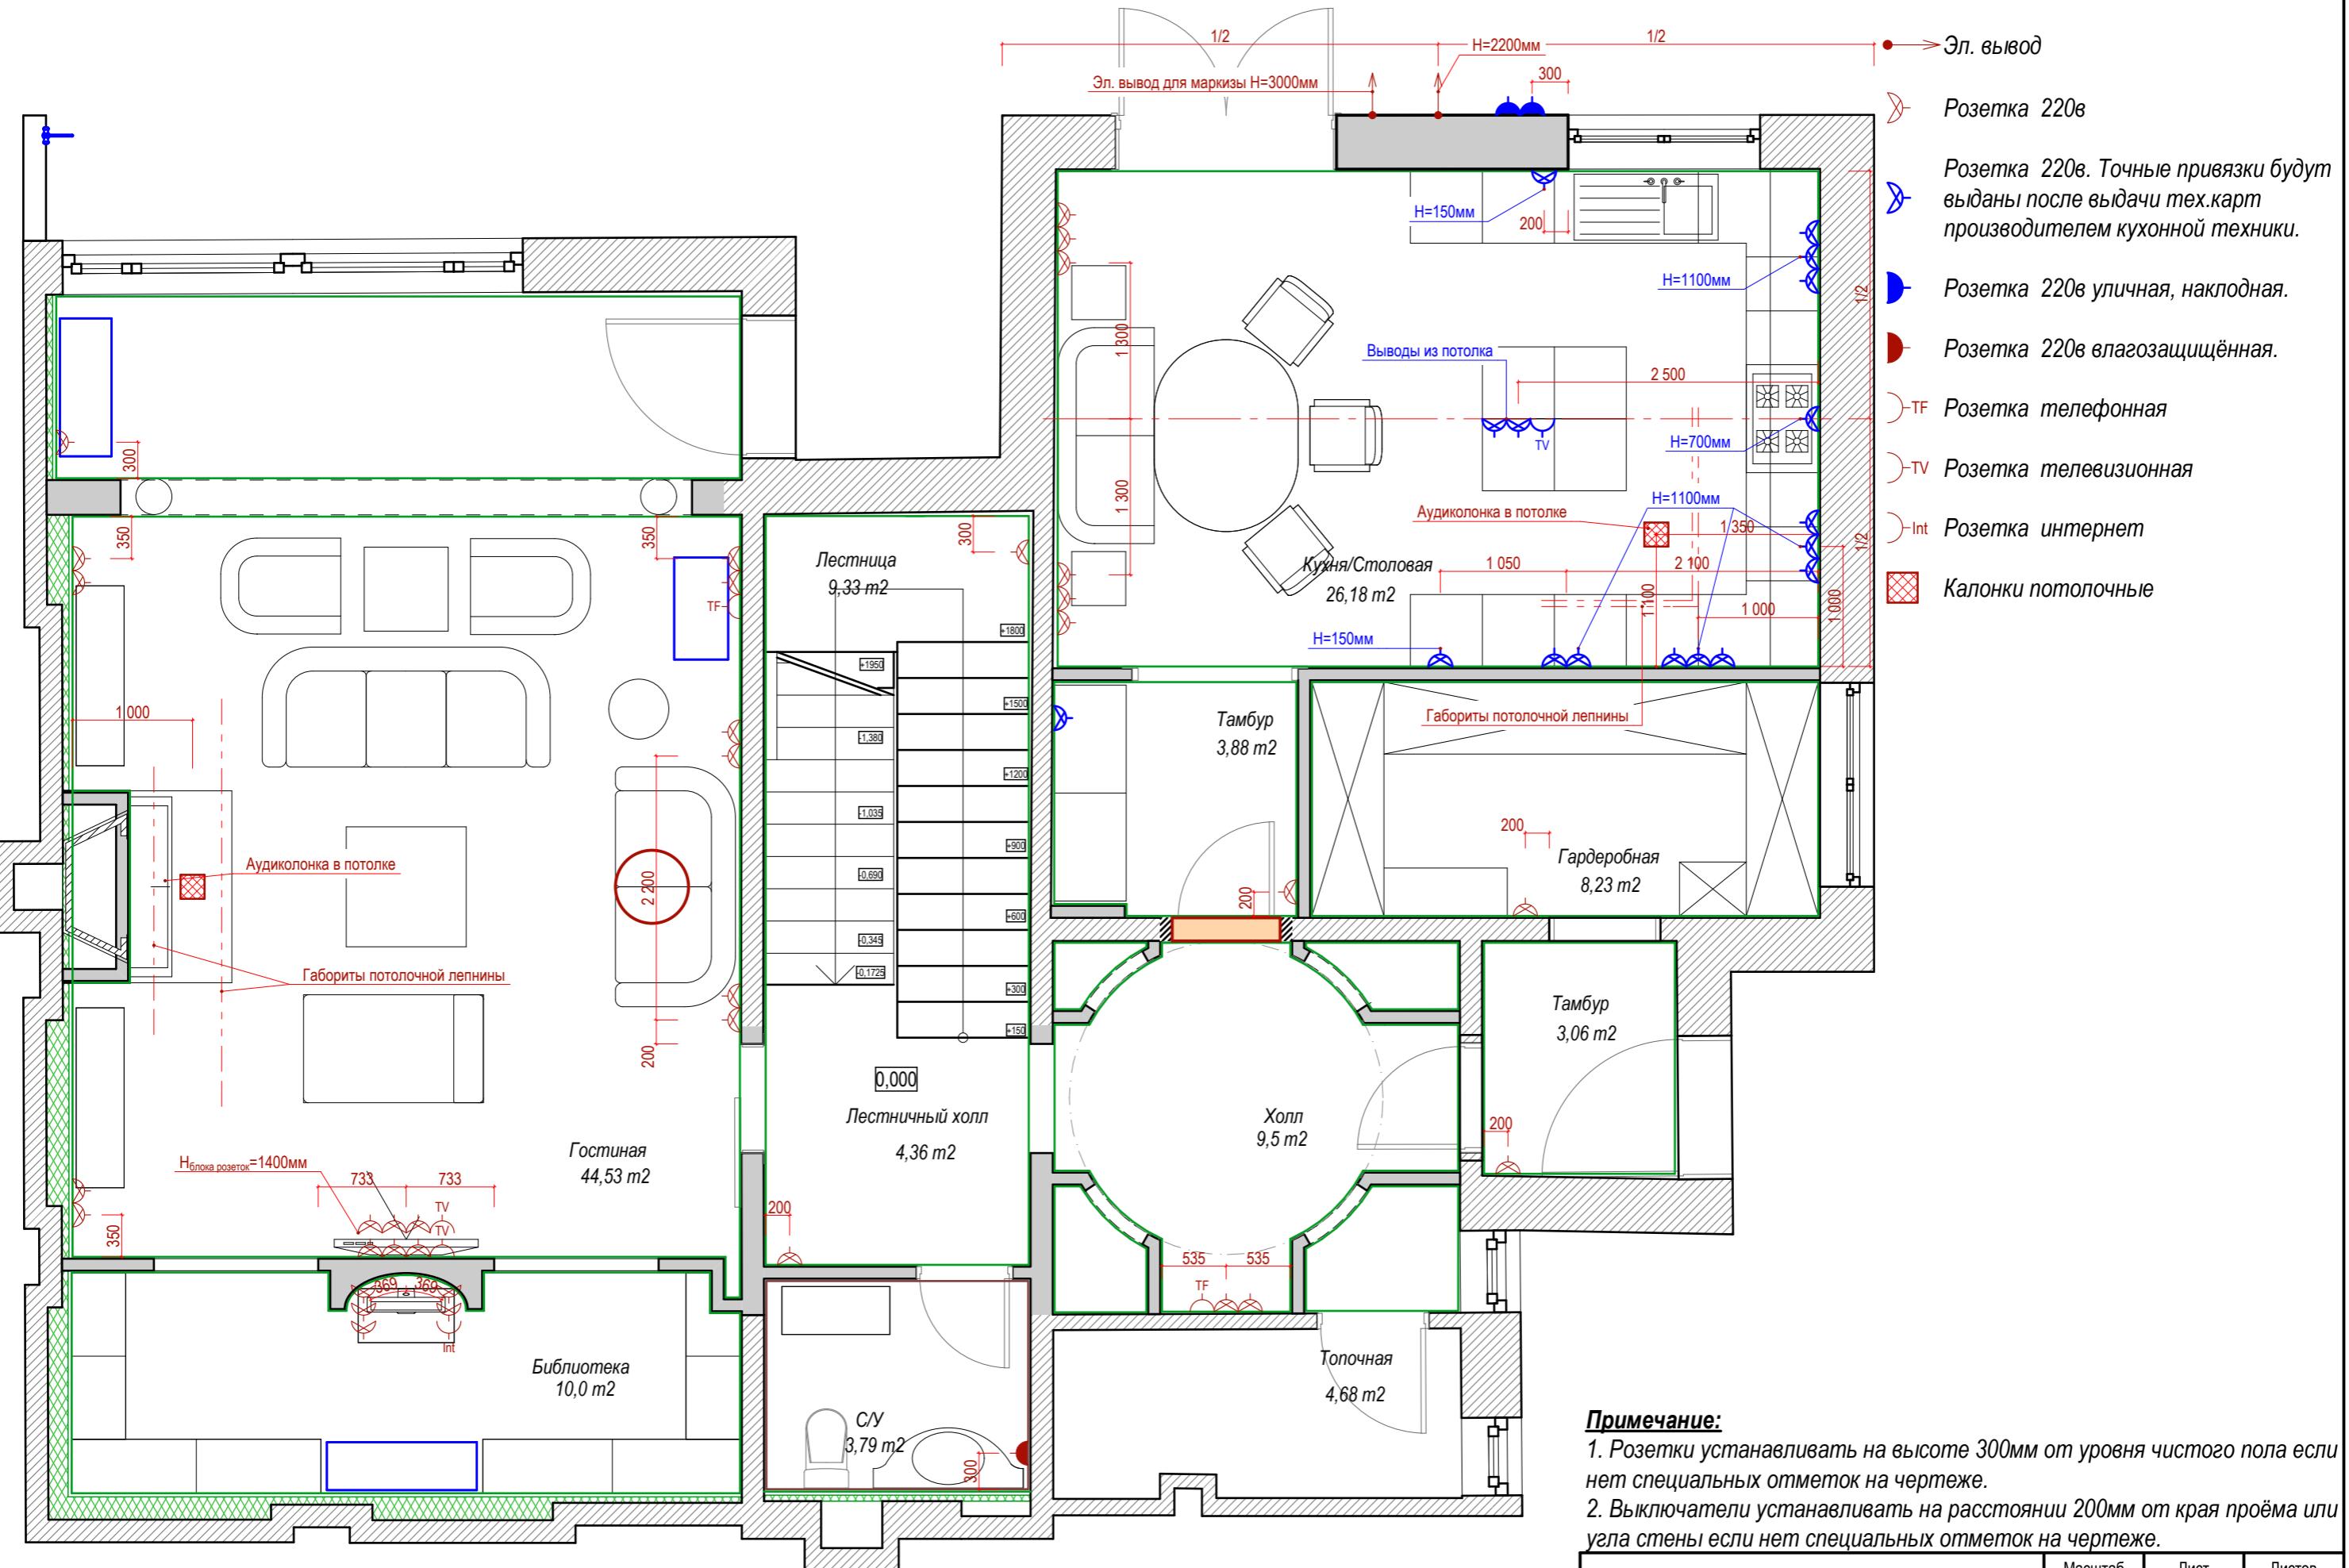

Примечание.


- Правила установки**

 1. Розетки устанавливать на высоте 300мм от уровня чистого пола если нет специальных отметок на чертеже.
 2. Выключатели устанавливать на расстоянии 200мм от края проёма или угла стены если нет специальных отметок на чертеже.

	Масштаб	Лист	Листов
Схема размещения розеток и эл. выводов 1го этажа.	1:50	43	46


Условные обозначения:

- Эл. вывод
- ☒ Розетка 220в
- ☒ Розетка 220в. Точные привязки будут выданы после выдачи тех.карт производителем кухонной техники.
- Розетка 220в влагозащищённая.
- TF Розетка телефонная
- TV Розетка телевизионная
- Int Розетка интернет
- ▨ Калонки потолочные

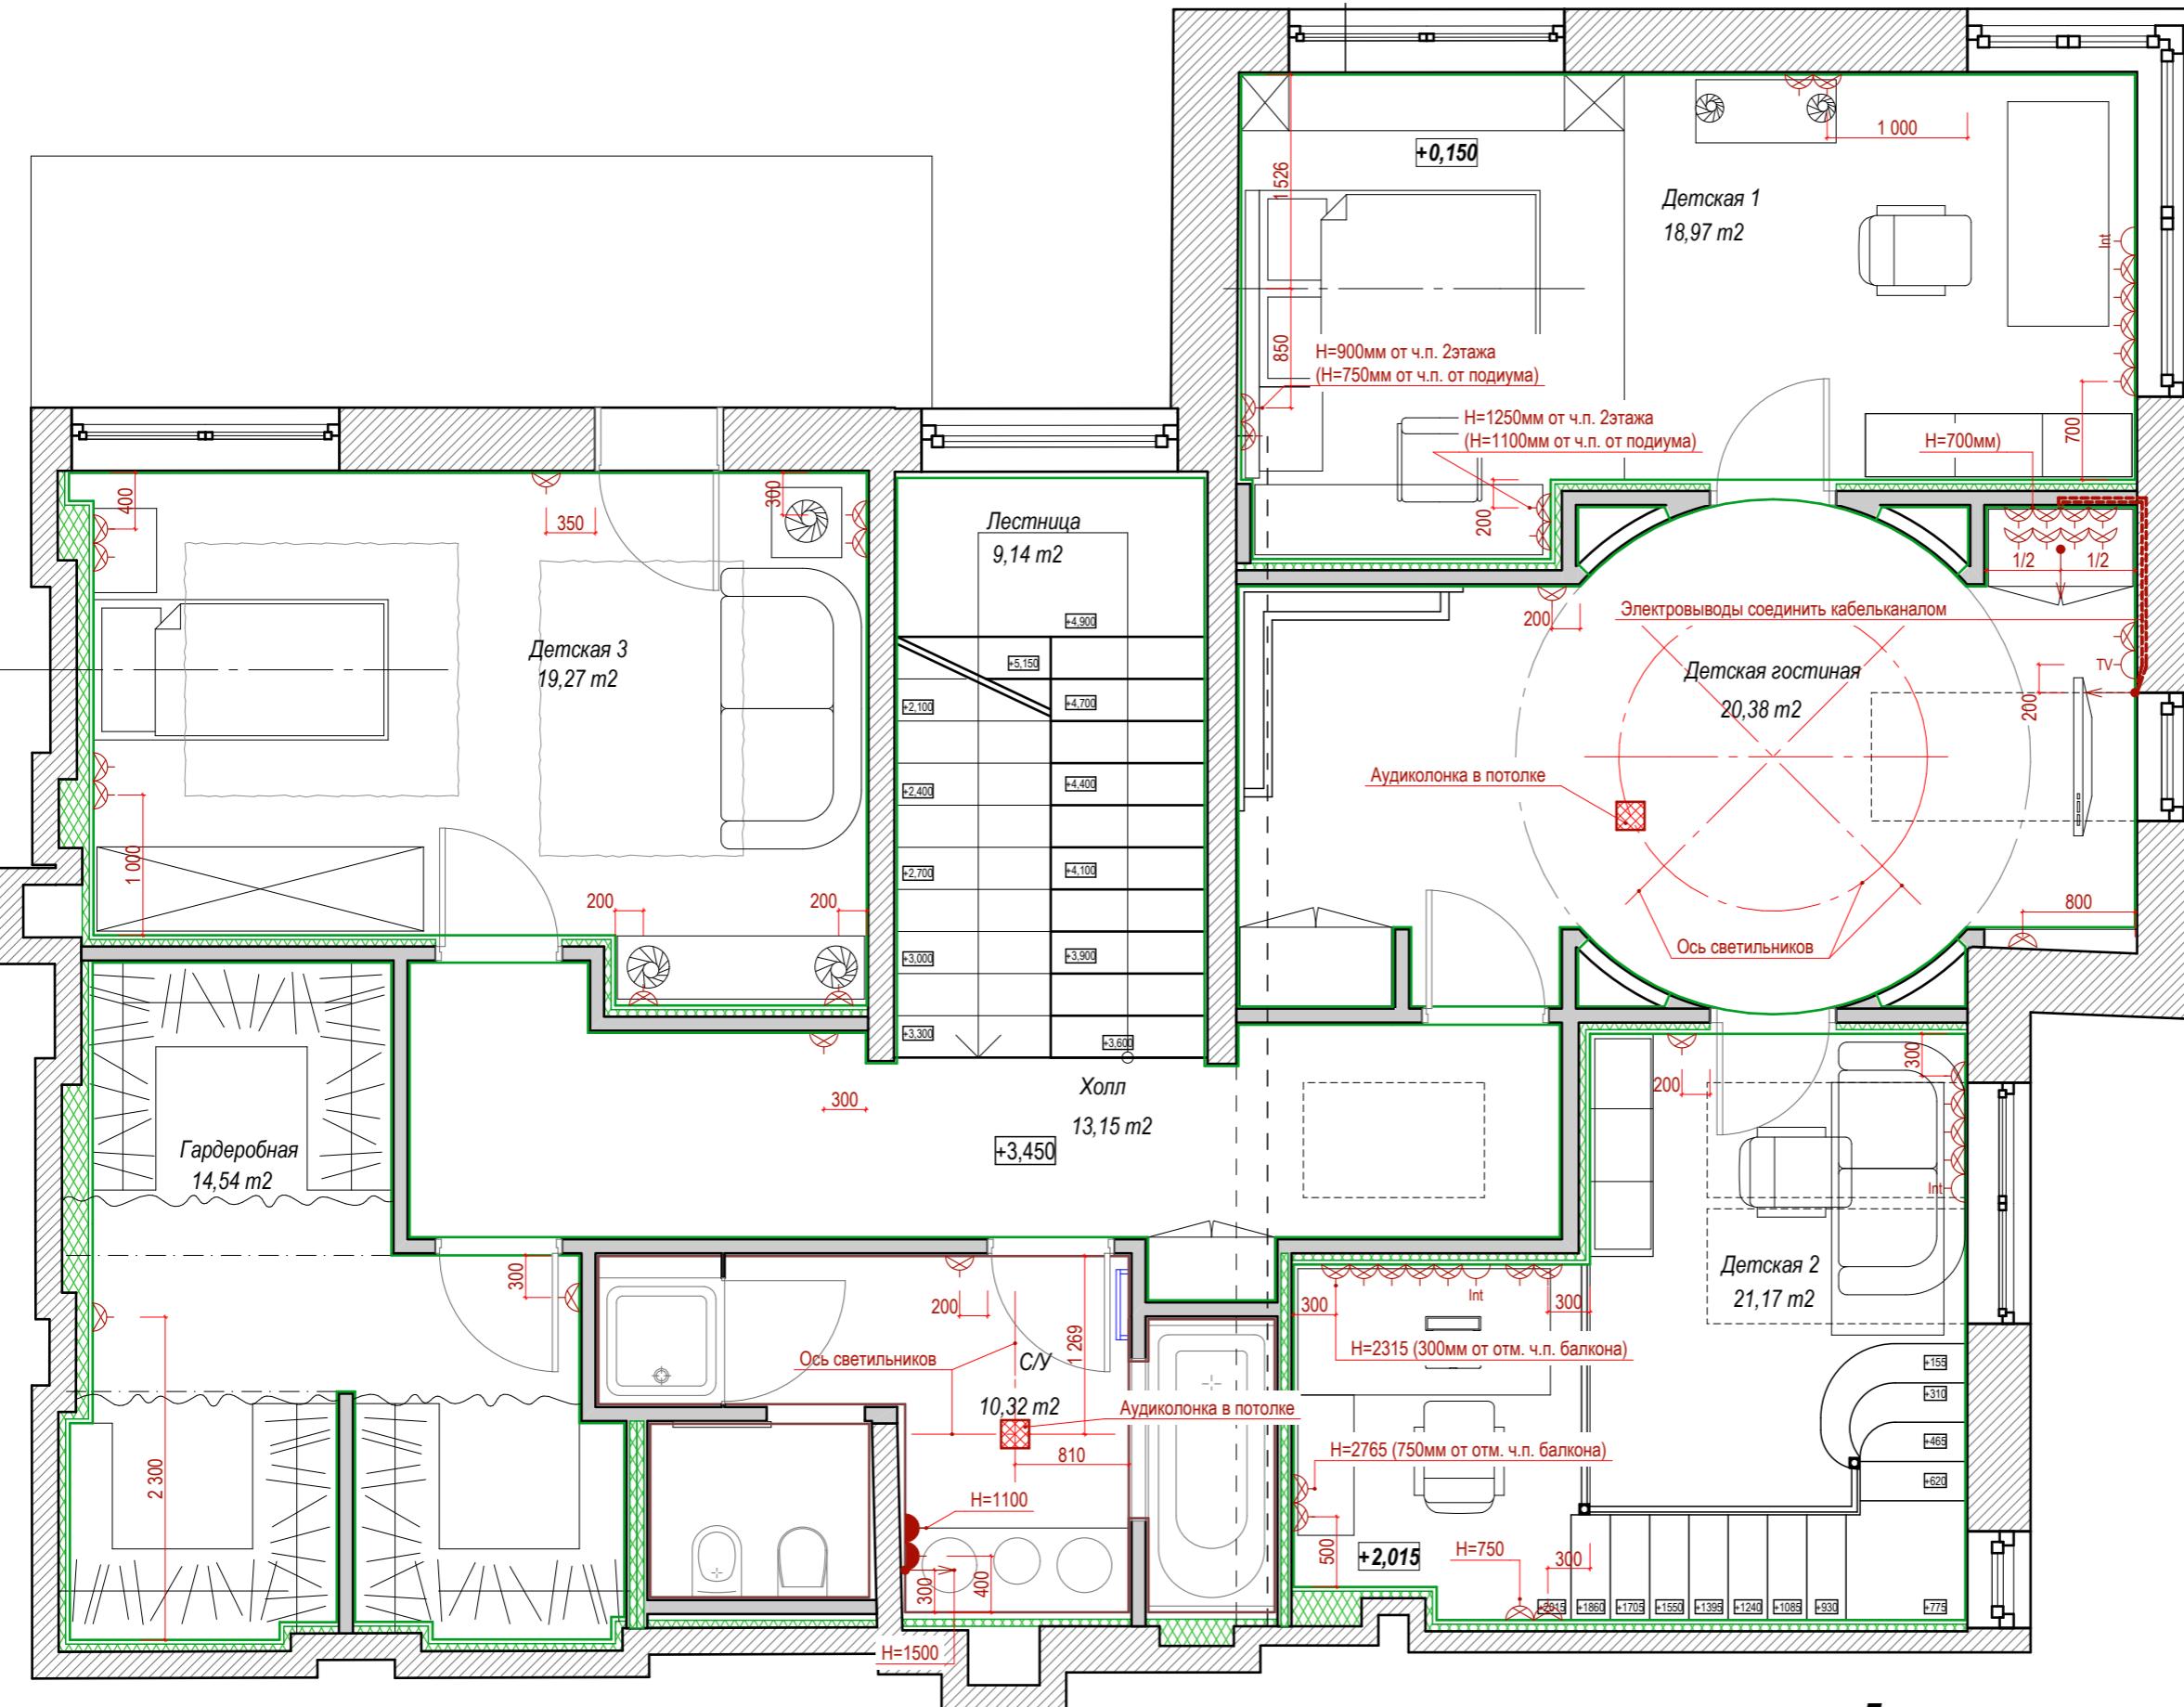

Условные обозначения:

- → Эл. вывод
- Розетка 220в
- Розетка 220в. Точные привязки будут выданы после выдачи тех.карт производителем кухонной техники.
- Розетка 220в влагозащищённая.
- TF Розетка телефонная
- TV Розетка телевизионная
- Int Розетка интернет
- Калонки потолочные

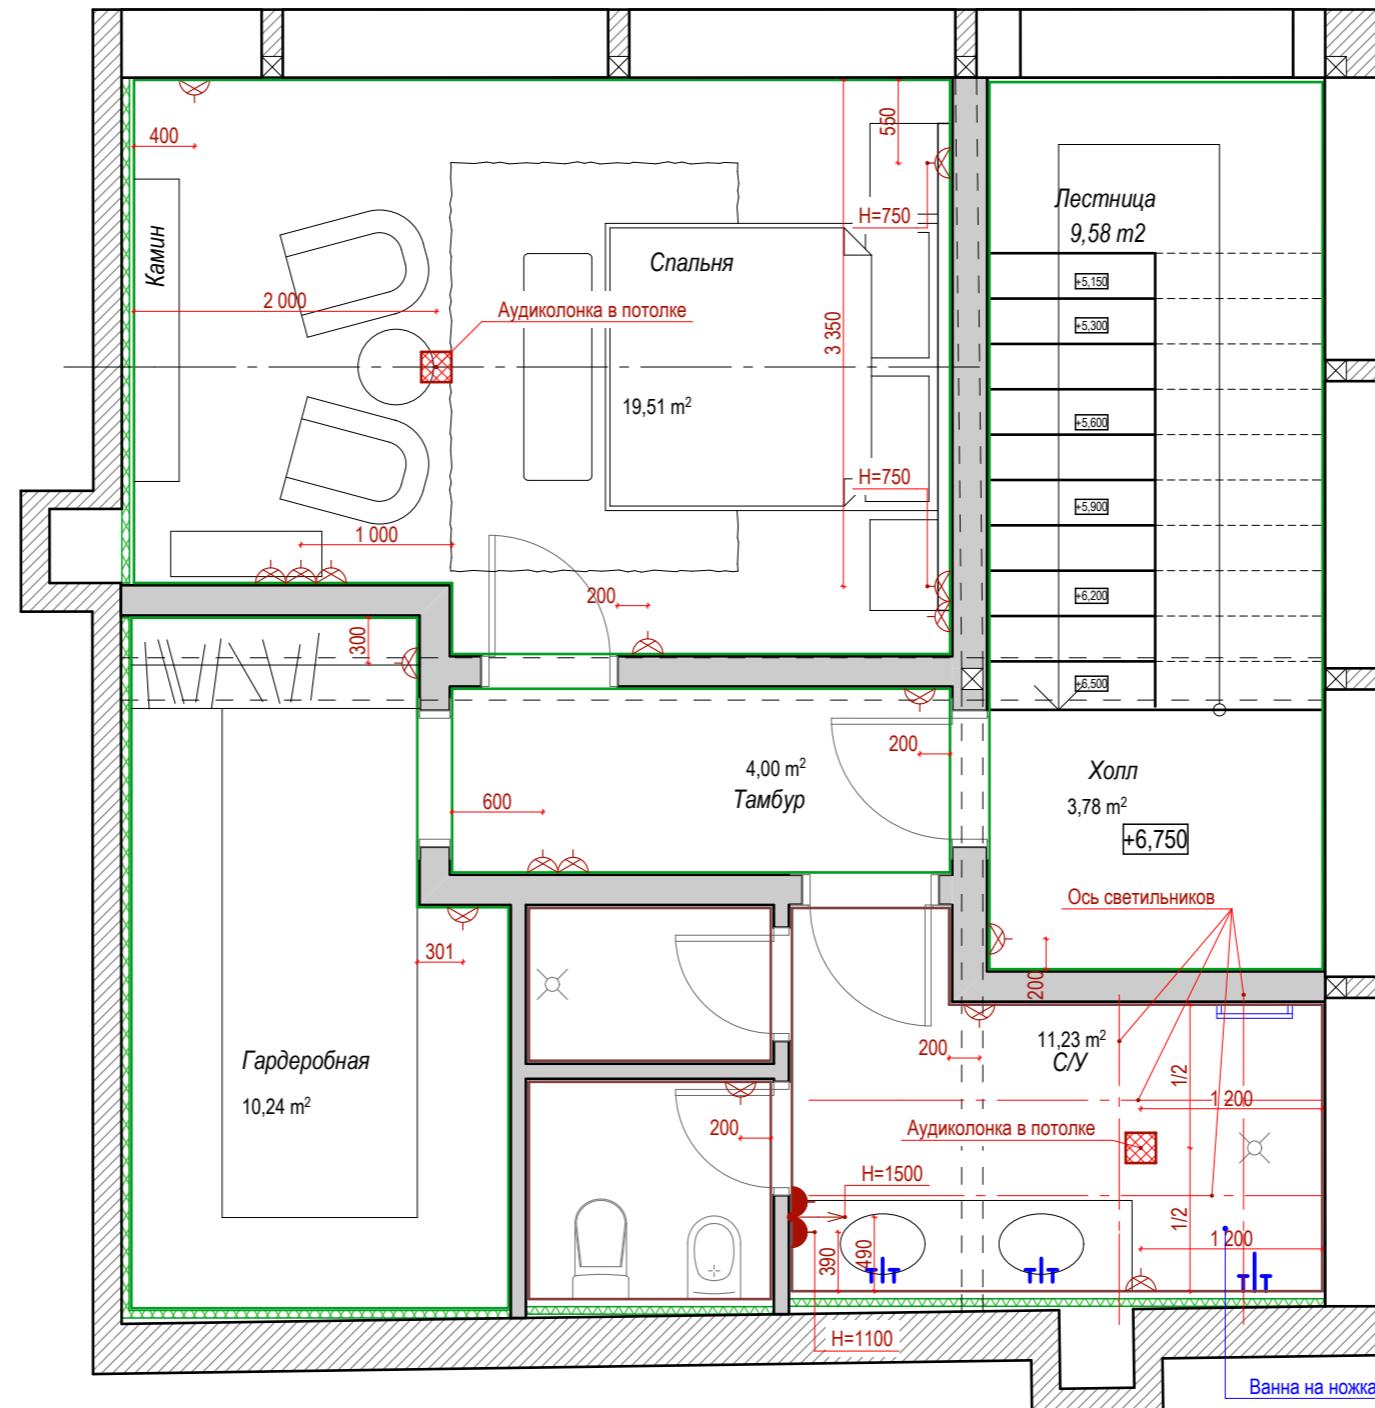

Примечание:

1. Розетки устанавливать на высоте 300мм от уровня чистого пола если нет специальных отметок на чертеже.
2. Выключатели устанавливать на расстоянии 200мм от края проёма или угла стены если нет специальных отметок на чертеже.

Схема размещения розеток и эл. выводов мансардного этажа.

Масштаб	Лист	Листов
1:50	45	46

